


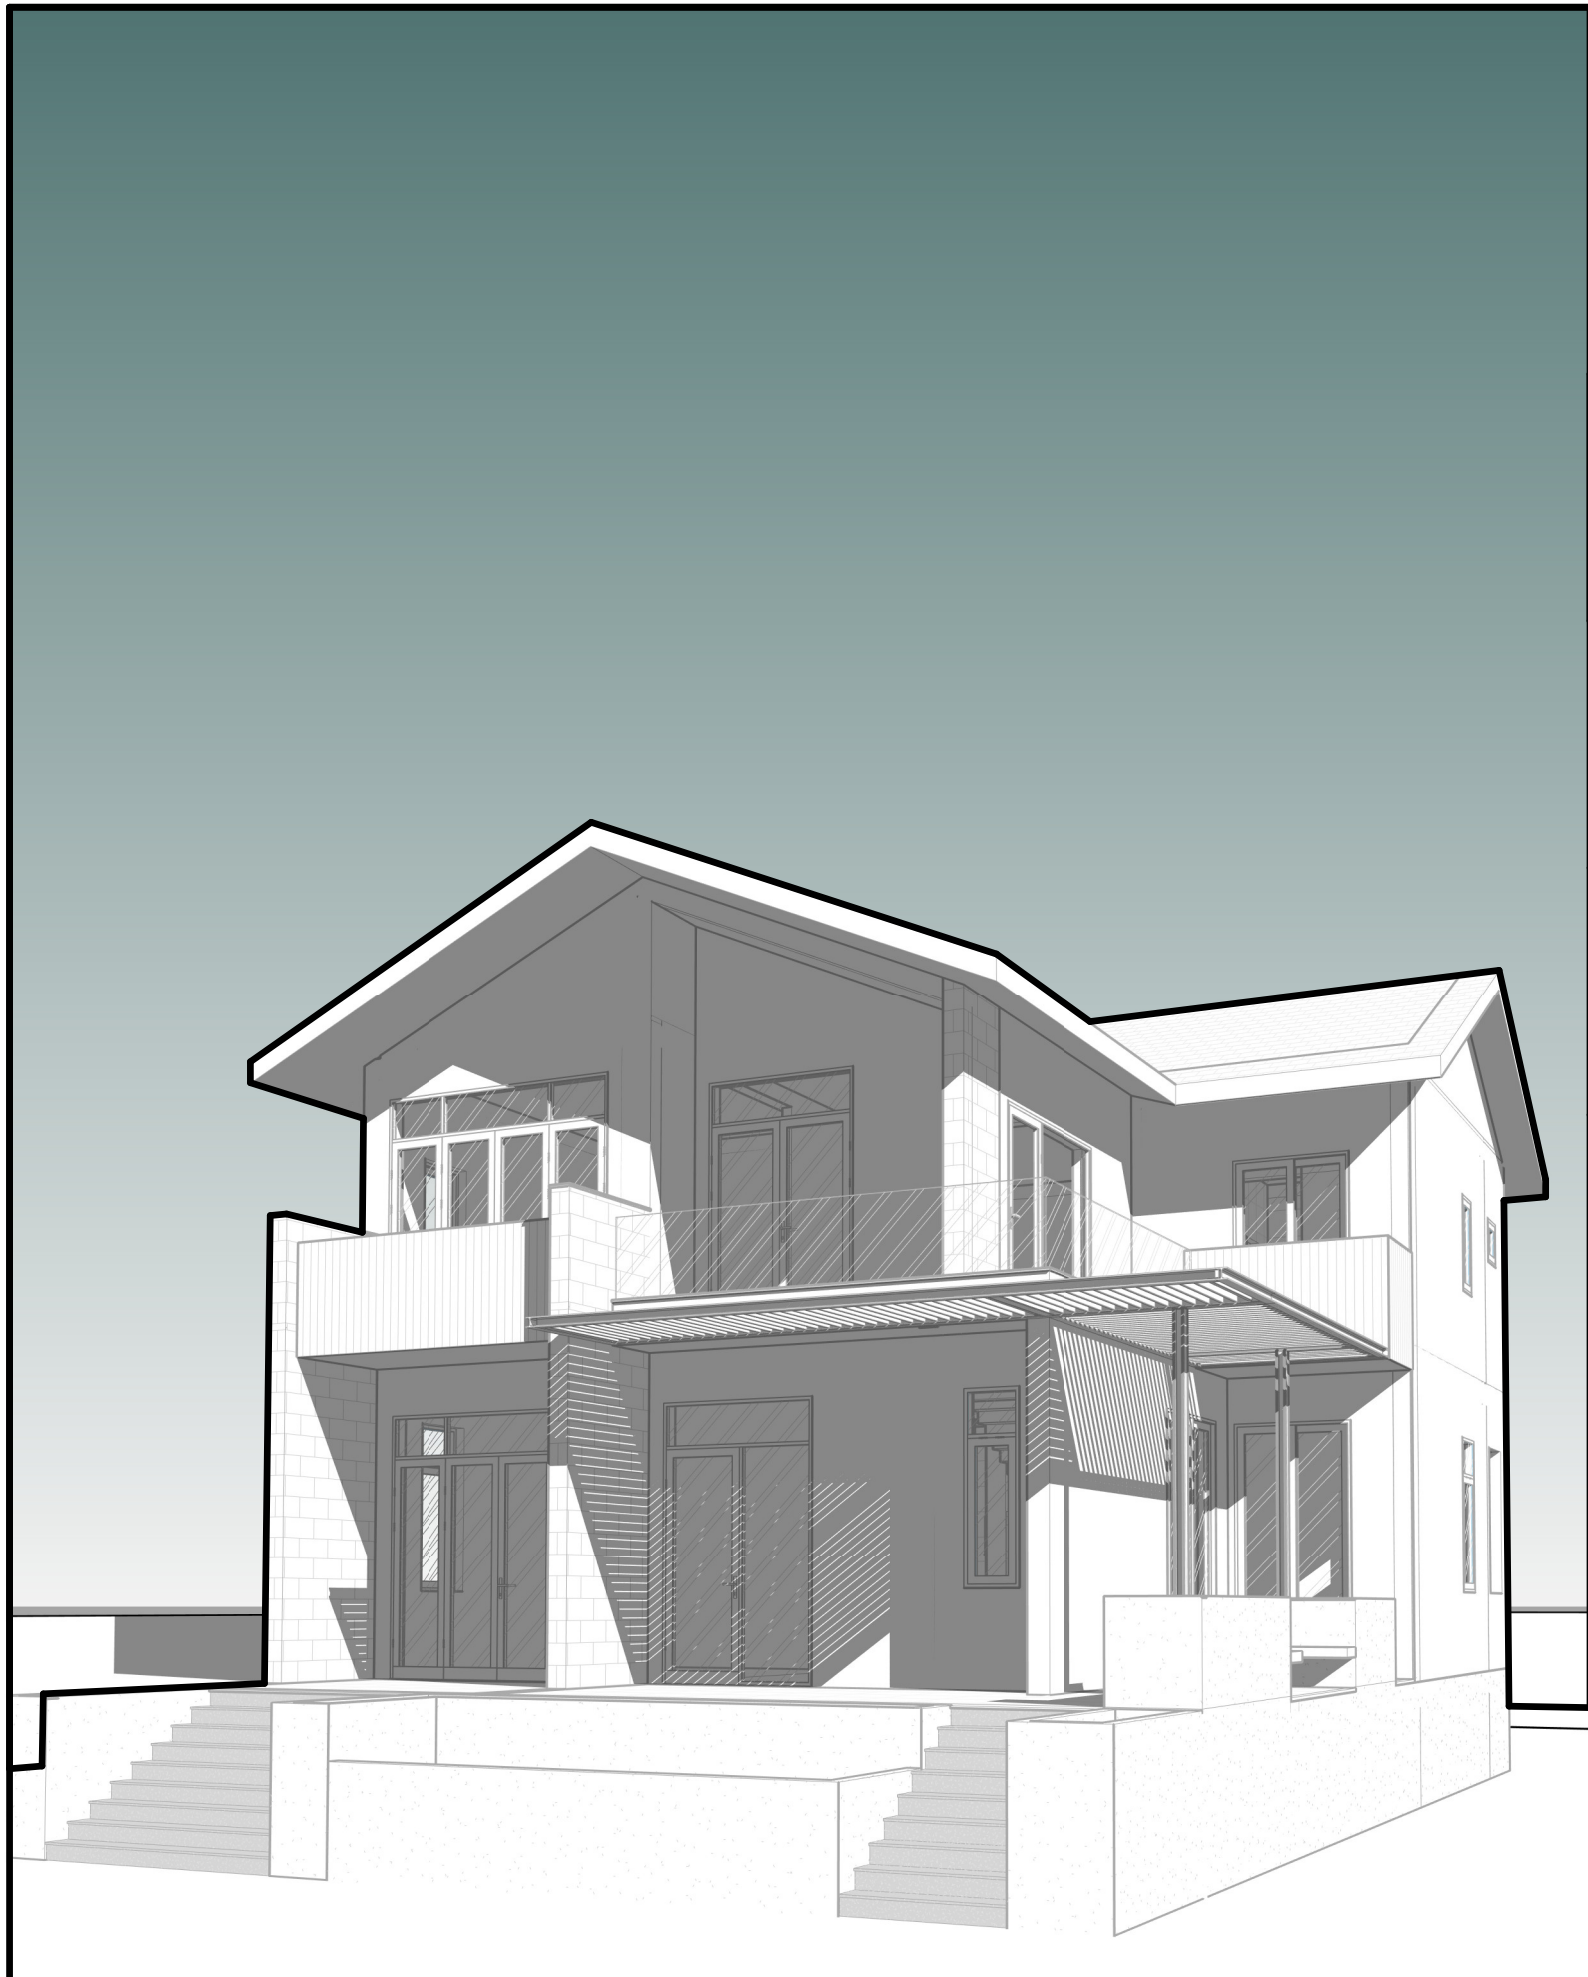

HỒ SƠ THIẾT KẾ










DANH MỤC BẢN VẼ KIẾN TRÚC		
STT	KÝ HIỆU	TÊN BẢN VẼ
1	A000	BÌA HỒ SƠ
2	A001	DANH SÁCH BẢN VẼ
3	A002	CHI CHÚ-KÝ HIỆU TRONG BẢN VẼ
4	A003	CẤU TẠO TƯỜNG ĐIỂN HÌNH
5	A004	CẤU TẠO TƯỜNG ĐIỂN HÌNH
6	A006	CẤU TẠO SÀN ĐIỂN HÌNH
7	A007	CHI TIẾT CẤU TẠO ĐIỂN HÌNH
8	A008	MẶT BẰNG VỊ TRÍ KHU ĐẤT
9	A101	MB KÍCH THƯỚC TẦNG 1
10	A102	PHỐI CẢNH TẦNG 1
11	A103	MB KÍCH THƯỚC TẦNG 2
12	A104	PHỐI CẢNH TẦNG 2
13	A105	MB KÍCH THƯỚC MÁI
14	A106	PHỐI CẢNH CẤU TẠO MÁI
15	A107	MẶT ĐỨNG TRỤC A-D
16	A108	MẶT ĐỨNG TRỤC D-A
17	A109	MẶT ĐỨNG TRỤC 1-3
18	A110	MẶT ĐỨNG TRỤC 3-1
19	A111	MẶT CẮT A-A
20	A112	MẶT CẮT B-B
21	A113	MẶT CẮT C-C
22	A114	PHỐI CẢNH CHUNG
23	A115	PHỐI CẢNH CHUNG
24	A201	MB BỐ TRÍ VẬT DỤNG TẦNG 1
25	A202	MB HOÀN THIỆN SÀN TẦNG 1
26	A203	MB BỐ TRÍ VẬT DỤNG TẦNG 2
27	A204	MB HOÀN THIỆN SÀN TẦNG 2
28	A301	CHI TIẾT CẦU THANG
29	A302	CHI TIẾT CẦU THANG
30	A303	CHI TIẾT BẬC CẤP 01
31	A304	CHI TIẾT BẬC CẤP 01
32	A305	CHI TIẾT BẬC CẤP 02
33	A306	CHI TIẾT BẬC CẤP 03
34	A401	CHI TIẾT VS 1
35	A402	CHI TIẾT VS 1
36	A403	CHI TIẾT VS 1

DANH MỤC BẢN VẼ KIẾN TRÚC		
STT	KÝ HIỆU	TÊN BẢN VẼ
37	A404	CHI TIẾT VS 2
38	A405	CHI TIẾT VS 2
39	A406	CHI TIẾT VS 2
40	A407	CHI TIẾT VS 3
41	A408	CHI TIẾT VS 3
42	A409	CHI TIẾT VS 3
43	A501	THỐNG KÊ CỬA ĐI VÀ CỬA SỔ
44	A502	CHI TIẾT CỬA ĐI
45	A503	CHI TIẾT CỬA ĐI
46	A504	CHI TIẾT CỬA ĐI
47	A505	CHI TIẾT CỬA ĐI
48	A506	CHI TIẾT CỬA ĐI
49	A507	CHI TIẾT CỬA SỔ
50	A508	CHI TIẾT CỬA SỔ
51	A601	CHI TIẾT HỆ LAM TRANG TRÍ
52	A602	CHI TIẾT LAN CAN 01
53	A603	CHI TIẾT BỒN HOA
54	A701	MẶT BẰNG TRẦN TẦNG 1
55	A702	MẶT BẰNG TRẦN TẦNG 2
58	A703	CHI TIẾT CẤU TẠO TRẦN
59	A801	MẶT BẰNG HÀNG RÀO VÀ CỔNG
60	A802	CHI TIẾT CỔNG
61	A803	CHI TIẾT HÀNG RÀO ĐIỂN HÌNH

NHỮNG QUY ĐỊNH CHUNG


- 01 - TẤT CẢ KÍCH THƯỚC ĐƯA RA LÀ KÍCH THƯỚC HOÀN THIỆN, ĐƠN VỊ MILIMET(MM) TRỪ MỘT SỐ TRƯỜNG HỢP KHÁC
- 02 - NHÀ THẦU PHẢI KIỂM TRA TẤT CẢ CÁC KÍCH THƯỚC THỰC TẾ TRÊN CÔNG TRƯỜNG TRƯỚC KHI TIẾN HÀNH THI CÔNG. NẾU CÓ BẤT KỲ SỰ KHÔNG ĐỒNG NHẤT GIỮA BẢN VẼ CỦA CÁC BỘ MÔN VỚI THỰC TẾ CÔNG TRƯỜNG ĐỀU PHẢI ĐƯỢC TRÌNH CHO ĐẠI DIỆN CỦA CHỦ ĐẦU TƯ VÀ ĐƠN VỊ TƯ VẤN THIẾT KẾ XEM XÉT ĐỂ ĐIỀU CHỈNH TRƯỚC KHI BẮT ĐẦU CÔNG VIỆC.
- 03 - NHÀ THẦU PHẢI THEO NHỮNG CHI TIẾT VÀ PHƯƠNG PHÁP LẮP ĐẶT CỦA NHÀ SẢN XUẤT VÀ BẢO HÀNH TỐT NHẤT. SỰ KHÁC BIỆT VỚI CHI TIẾT CỦA NHÀ SẢN XUẤT ĐỀU PHẢI ĐƯỢC TRÌNH CHO ĐẠI DIỆN CỦA CHỦ ĐẦU TƯ VÀ ĐƠN VỊ TƯ VẤN THIẾT KẾ XEM XÉT.
- 04 - CHI TIẾT VÀ SẢN PHẨM MÀ THEO KINH NGHIỆM CỦA NHÀ THẦU LÀ KHÔNG TỐT, NHỮNG CHI TIẾT KHÔNG RÕ RÀNG HOẶC KHÔNG CHÍNH XÁC PHẢI TRÌNH CHO ĐƠN VỊ TƯ VẤN VÀ ĐẠI DIỆN CHỦ ĐẦU TƯ TRONG THỜI GIAN SỚM NHẤT ĐỂ GIẢI QUYẾT.
- 05 - NHÀ THẦU PHẢI CUNG CẤP MÔ HÌNH HOÀN THIỆN VÀ MẪU THỦ NHƯ HỢP ĐỒNG THẦU CHO ĐẠI DIỆN CỦA ĐẦU TƯ PHÊ DUYỆT TRƯỚC KHI LẮP ĐẶT.
- 06 - ĐƠN VỊ TƯ VẤN KHÔNG CÓ TRÁCH NHIỆM ĐỐI VỚI THÔNG TIN KHU ĐẤT VÀ ĐIỀU KIỆN HIỆN TRẠNG THEO BẢN VẼ KHẢO SÁT ĐỊA CHẤT ĐƯỢC CHỦ ĐẦU TƯ CUNG CẤP.
- 07 - TẤT CẢ MÁI CHE VÀ LÁT ĐƯỜNG PHẢI ĐÁNH DỐC CHẢY VỀ MƯƠNG THÓAT NƯỚC ĐỂ TRÁNH ỌNG NƯỚC, Ứ NƯỚC ...
- 08 - TẤT CẢ CAO ĐỘ TRONG BẢN VẼ LÀ CAO ĐỘ SÀN HOÀN THIỆN TRỪ KHI CÓ NHỮNG CHI TIẾT ĐẶC BIỆT KHÁC.
- 09 - NHÀ THẦU PHẢI KHẢO SÁT, VÀ ĐO VẼ LẠI TẤT CẢ ĐƯỜNG THÓAT NƯỚC, CẤP NƯỚC, KHOAN KHẢO SÁT, MỐC CAO ĐỘ... TRƯỚC KHI TIẾN HÀNH XÂY DỰNG ĐỂ ĐẢM BẢO RẰNG CHÚNG ĐƯỢC BẢO VỆ TRONG KHI THI CÔNG. TRƯỜNG HỢP XẢY RA HƯ HẠI, NHÀ THẦU PHẢI CHỊU TRÁCH NHIỆM SỬA CHỮA LẠI GIỐNG NHƯ BAN ĐẦU. MỌI CHI PHÍ PHÁT SINH DO NHÀ THẦU XÂY DỰNG CHI TRẢ.
- 10 - NHÀ THẦU BẢO ĐẢM THÓAT NƯỚC MẶT TRONG QUÁ TRÌNH THI CÔNG TẠI CÔNG TRƯỜNG, HỆ THOÁT NƯỚC MẶT TẠM THỜI CÓ THỂ ĐƯỢC XÂY NẾU THỰC SỰ CẦN THIẾT.
- 11 - BẢN VẼ PHẢI ĐƯỢC XEM VỚI SỰ LIÊN KẾT VỚI TẤT CẢ CÁC BẢN VẼ LIÊN QUAN KHÁC VÀ SPEC.

DIỄN GIẢI HỆ THỐNG KÝ HIỆU

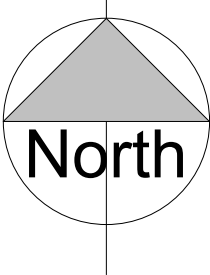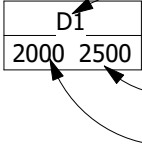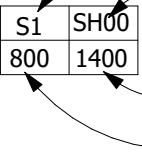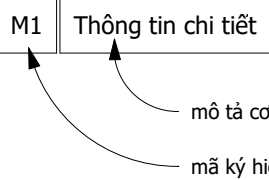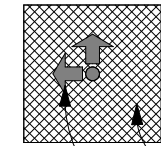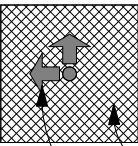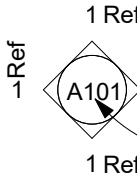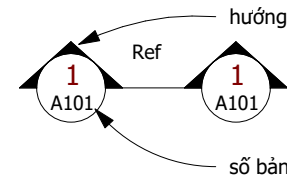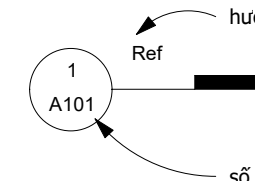
	KÝ HIỆU HƯỚNG BẮC	TÊN PHÒNG 150 m2	KÝ HIỆU TÊN PHÒNG diện tích phòng
	KÝ HIỆU CỬA ĐI	tên cửa chiều cao cửa chiều rộng cửa	
	KÝ HIỆU CỬA SỐ	tên cửa chiều cao bộ cửa chiều cao cửa chiều rộng cửa	
	KÝ HIỆU SÀN		
	KÝ HIỆU MÃ VẬT LIỆU		
	KÝ HIỆU MÁI	mô tả cơ bản mã ký hiệu	
	KÝ HIỆU CẦU THANG		
	KÝ HIỆU GẠCH LÁT ĐỊNH VỊ	viên định vị hướng lát	
	KÝ HIỆU TRẦN	loại trần cao độ trần	
	KÝ HIỆU MẶT ĐỨNG (TỔNG QUAN & CHI TIẾT)		
	KÝ HIỆU MẶT CẮT		
	KÝ HIỆU MẶT CẮT CHI TIẾT		
	KÝ HIỆU TRÍCH DẪN		

THỐNG KÊ CẤU TẠO TƯỜNG ĐIỂN HÌNH


TẦNG	LOẠI TƯỜNG	CHIỀU DÀY	THỂ TÍCH	MÔ TẢ CHI TIẾT
SÂN VƯỜN	T14	130	9.904 m³	TƯỜNG XÂY BỒN HOA, XÂY GẠCH DÀY 100, CHỐNG THẤM 2 MẶT, TÔ HOÀN THIỆN VÀ SƠN GIẢ BÊ TÔNG
SÂN VƯỜN	T15	215	15.175 m³	TƯỜNG MÓNG, XÂY ĐÁ CHÉ, TÔ HOÀN THIỆN MẶT NGOÀI VÀ SƠN GIẢ BÊ TÔNG
TẦNG 1	T1	230	18.545 m³	TƯỜNG BAO NGOÀI CÔNG TRÌNH, XÂY GẠCH DÀY 200, LỚP TÔ HOÀN THIỆN 2 MẶT DÀY 15mm, CHỐNG THẤM MẶT NGOÀI
TẦNG 1	T2	230	6.037 m³	TƯỜNG BAO NGOÀI CÔNG TRÌNH, XÂY GẠCH 200, MẶT NGOÀI TÔ HOÀN THIỆN DÀY 15, MẶT TRONG ỐP GẠCH CERAMIC, CHỐNG THẤM 2 MẶT
TẦNG 1	T3	130	2.521 m³	TƯỜNG BAO NGOÀI CÔNG TRÌNH, XÂY GẠCH DÀY 100, LỚP TÔ HOÀN THIỆN 2 MẶT DÀY 15mm, CHỐNG THẤM MẶT NGOÀI
TẦNG 1	T4	115	0.295 m³	TƯỜNG BAO HỘP KỸ THUẬT TẠI VỊ TRÍ KHO
TẦNG 1	T5	230	9.429 m³	TƯỜNG NGẮN TRONG NHÀ, XÂY GẠCH DÀY 200, LỚP TÔ HOÀN THIỆN 15mm Ở 2 MẶT
TẦNG 1	T6	130	3.101 m³	TƯỜNG NGẮN TRONG NHÀ, XÂY GẠCH DÀY 100, LỚP TÔ HOÀN THIỆN 15mm Ở 2 MẶT
TẦNG 1	T7	130	1.875 m³	TƯỜNG NGẮN PHÒNG VỆ SINH, XÂY GẠCH DÀY 100, ỐP GẠCH CERAMIC VÀ CHỐNG THẤM 2 MẶT TƯỜNG
TẦNG 1	T8	115	0.363 m³	TƯỜNG NGẮN PHÒNG VỆ SINH, XÂY GẠCH DÀY 100, TÔ HOÀN THIỆN MẶT NGOÀI, ỐP GẠCH CERAMIC MẶT TRONG VÀ CHỐNG THẤM 2 MẶT TƯỜNG
TẦNG 1	T9	230	2.482 m³	TƯỜNG TRANG TRÍ, XÂY GẠCH DÀY 200, ỐP ĐÁ CHÉ VÀ CHỐNG THẤM 2 MẶT TƯỜNG
TẦNG 2	T1	230	15.882 m³	TƯỜNG BAO NGOÀI CÔNG TRÌNH, XÂY GẠCH DÀY 200, LỚP TÔ HOÀN THIỆN 2 MẶT DÀY 15mm, CHỐNG THẤM MẶT NGOÀI
TẦNG 2	T2	230	8.774 m³	TƯỜNG BAO NGOÀI CÔNG TRÌNH, XÂY GẠCH 200, MẶT NGOÀI TÔ HOÀN THIỆN DÀY 15, MẶT TRONG ỐP GẠCH CERAMIC, CHỐNG THẤM 2 MẶT
TẦNG 2	T3	130	0.268 m³	TƯỜNG BAO NGOÀI CÔNG TRÌNH, XÂY GẠCH DÀY 100, LỚP TÔ HOÀN THIỆN 2 MẶT DÀY 15mm, CHỐNG THẤM MẶT NGOÀI
TẦNG 2	T5	230	2.413 m³	TƯỜNG NGẮN TRONG NHÀ, XÂY GẠCH DÀY 200, LỚP TÔ HOÀN THIỆN 15mm Ở 2 MẶT
TẦNG 2	T6	130	3.667 m³	TƯỜNG NGẮN TRONG NHÀ, XÂY GẠCH DÀY 100, LỚP TÔ HOÀN THIỆN 15mm Ở 2 MẶT
TẦNG 2	T7	130	0.701 m³	TƯỜNG NGẮN PHÒNG VỆ SINH, XÂY GẠCH DÀY 100, ỐP GẠCH CERAMIC VÀ CHỐNG THẤM 2 MẶT TƯỜNG
TẦNG 2	T8	115	0.799 m³	TƯỜNG NGẮN PHÒNG VỆ SINH, XÂY GẠCH DÀY 100, TÔ HOÀN THIỆN MẶT NGOÀI, ỐP GẠCH CERAMIC MẶT TRONG VÀ CHỐNG THẤM 2 MẶT TƯỜNG
TẦNG 2	T9	230	1.356 m³	TƯỜNG TRANG TRÍ, XÂY GẠCH DÀY 200, ỐP ĐÁ CHÉ VÀ CHỐNG THẤM 2 MẶT TƯỜNG
TẦNG 2	T10	130	1.906 m³	TƯỜNG NGẮN GIỮA PHÒNG VỆ SINH VÀ PHÒNG NGỦ, XÂY GẠCH 100, CHỐNG THẤM 1 MẶT
TẦNG 2	T11	150	1.073 m³	TƯỜNG XÂY LÀM LAN CAN, XÂY GẠCH DÀY 120, TÔ HOÀN THIỆN VÀ ỐP CONWOOD
TẦNG 2	T12	130	0.202 m³	TƯỜNG XÂY LÀM BÊ LAN CAN KÍNH, XÂY GẠCH DÀY 100, TÔ HOÀN THIỆN 2 MẶT 15mm, CỎ MẶT ĐÁ DÀY 20mm TRÊN ĐỈNH TƯỜNG
CHÂN MÁI	T13	230	7.151 m³	TƯỜNG THU HỒI ĐỖ DÀN KÈO MÁI, XÂY GẠCH DÀY 200, LỚP TÔ HOÀN THIỆN 2 MẶT DÀY 15mm, ĐỤC LỖ THÔNG R600XC600 CHÍNH GIỮA TƯỜNG

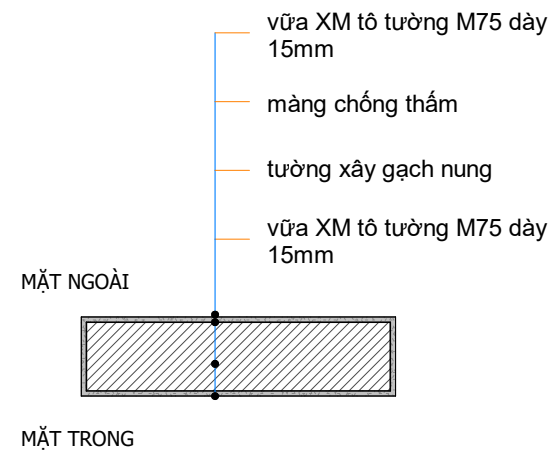


TƯỜNG T1&T3
1 : 20

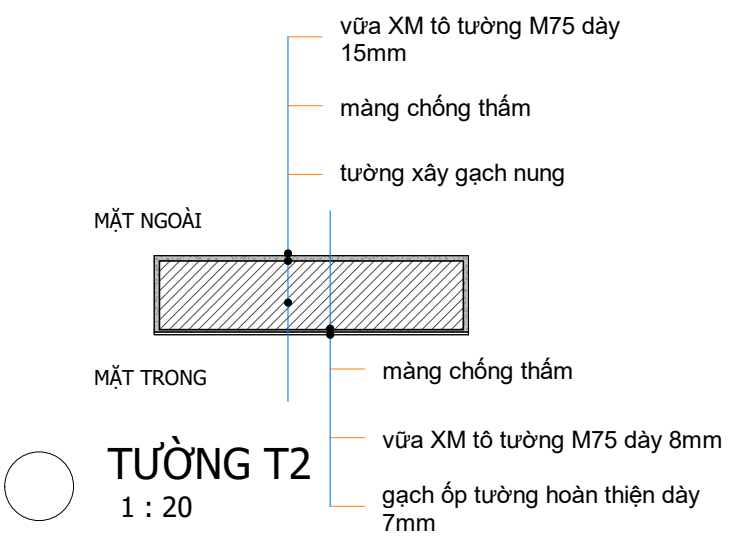


TƯỜNG T2
1 : 20

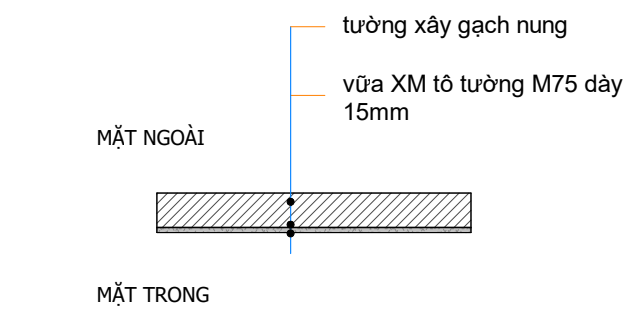


TƯỜNG T4
1 : 20

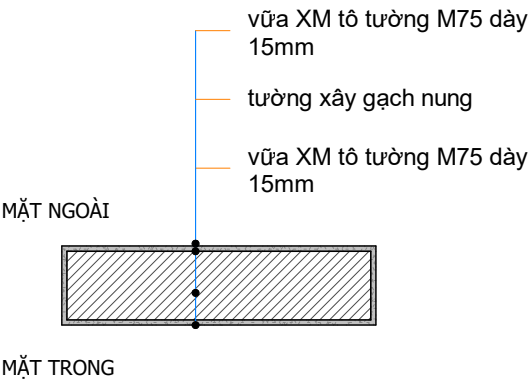


TƯỜNG T5,T6&T14
1 : 20

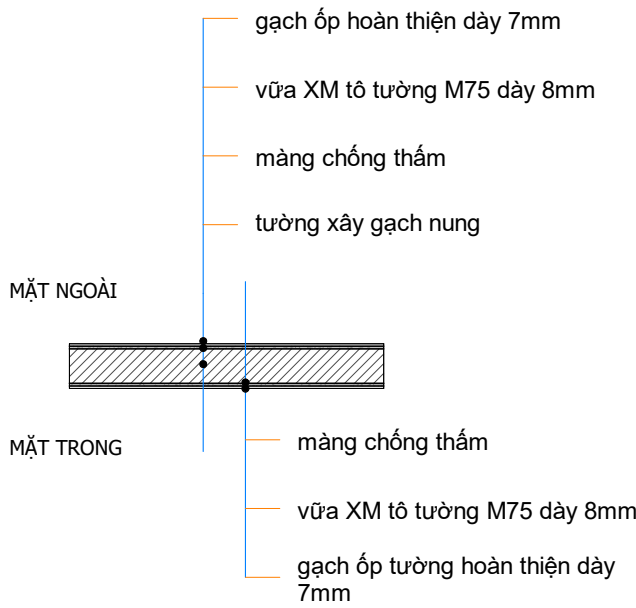


TƯỜNG T7&T11
1 : 20

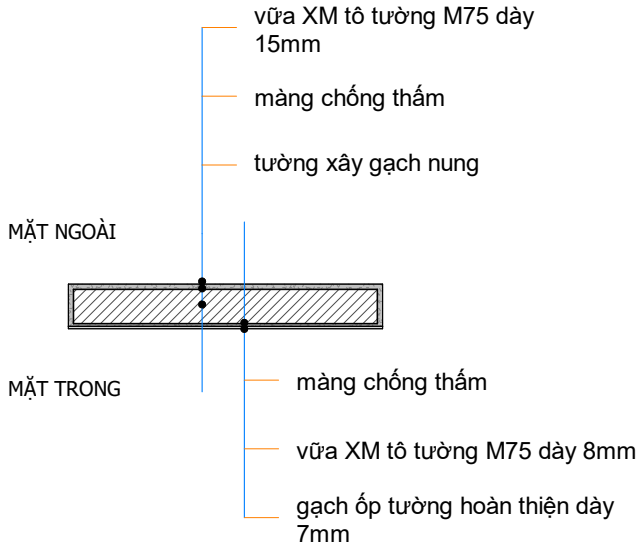


TƯỜNG T8
1 : 20

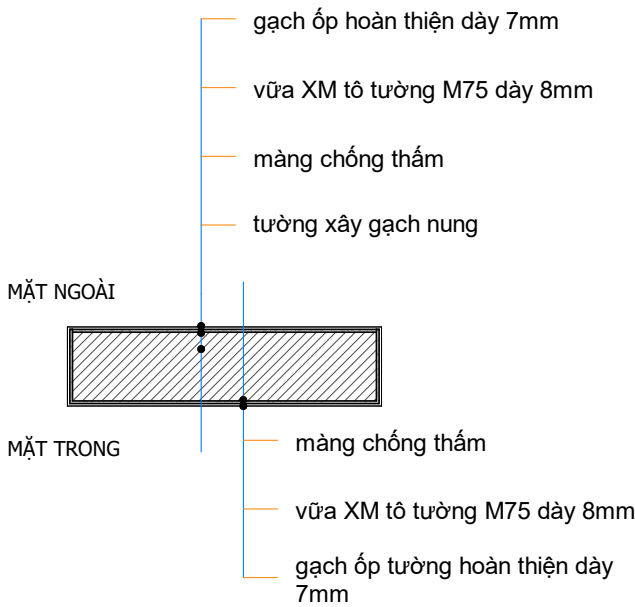


TƯỜNG T9
1 : 20

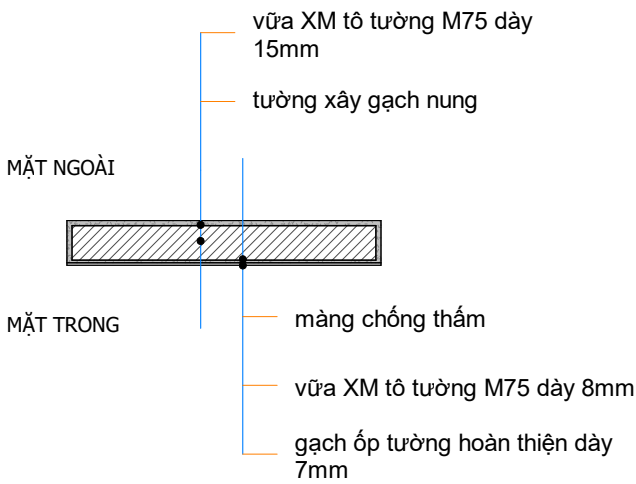


TƯỜNG T10
1 : 20

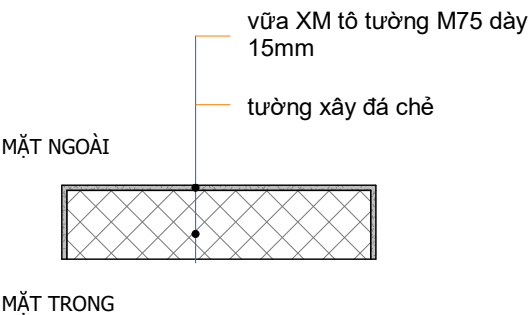

TƯỜNG T15
1 : 20

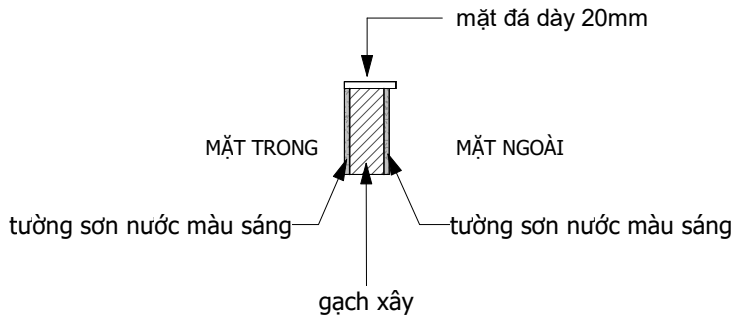


TƯỜNG T12
1 : 20

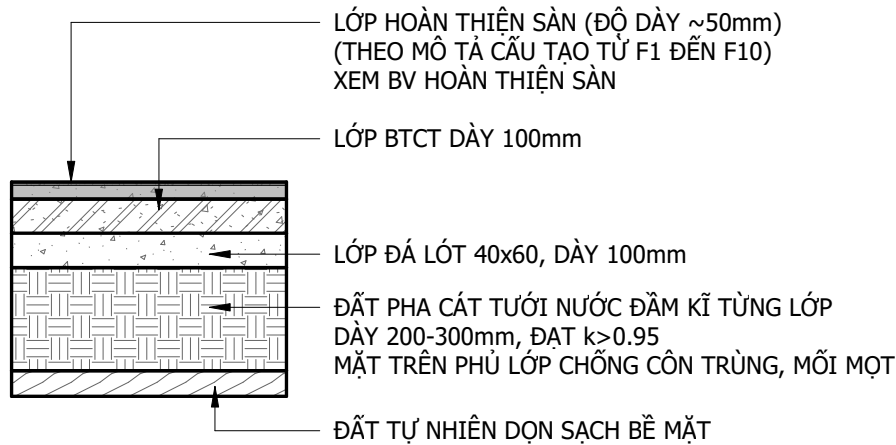

(VỊ TRÍ HIỂN, CÁC PHÒNG CHỨC NĂNG TẦNG 1)

CẤU TẠO NỀN TẦNG 1


1 : 20

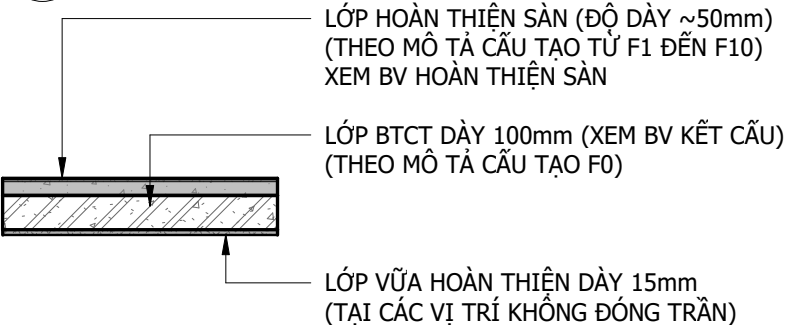

(VỊ TRÍ CÁC PHÒNG CHỨC NĂNG TẦNG 2)

CẤU TẠO SÀN TẦNG 2


1 : 20

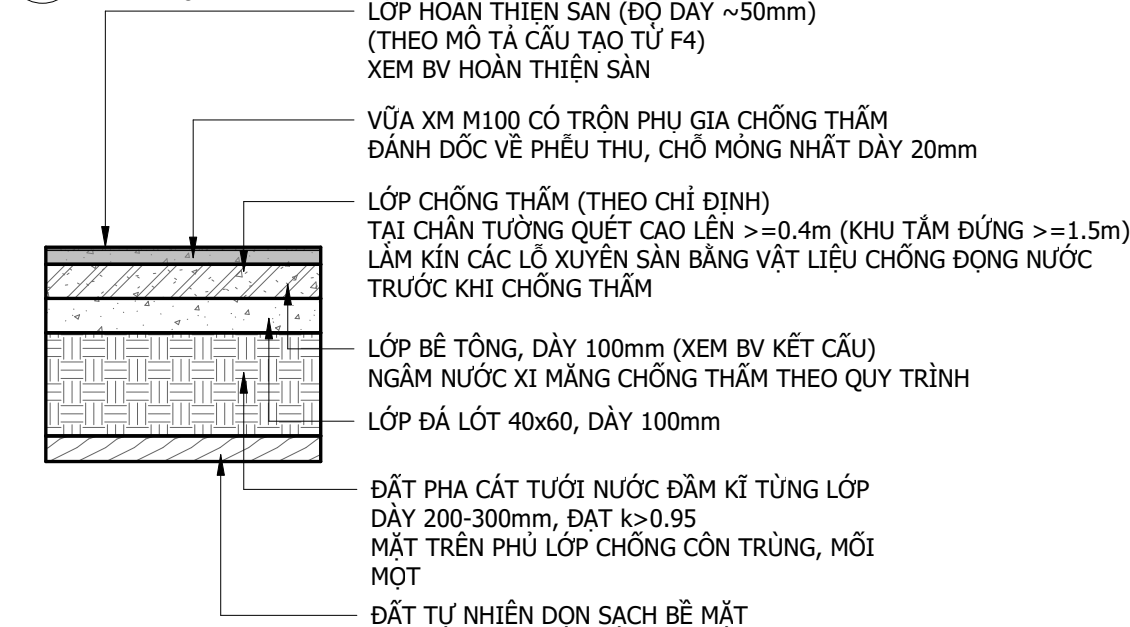

(VỊ TRÍ KHU VỆ SINH TẦNG 1)

CẤU TẠO NỀN WC TẦNG 1

1 : 20

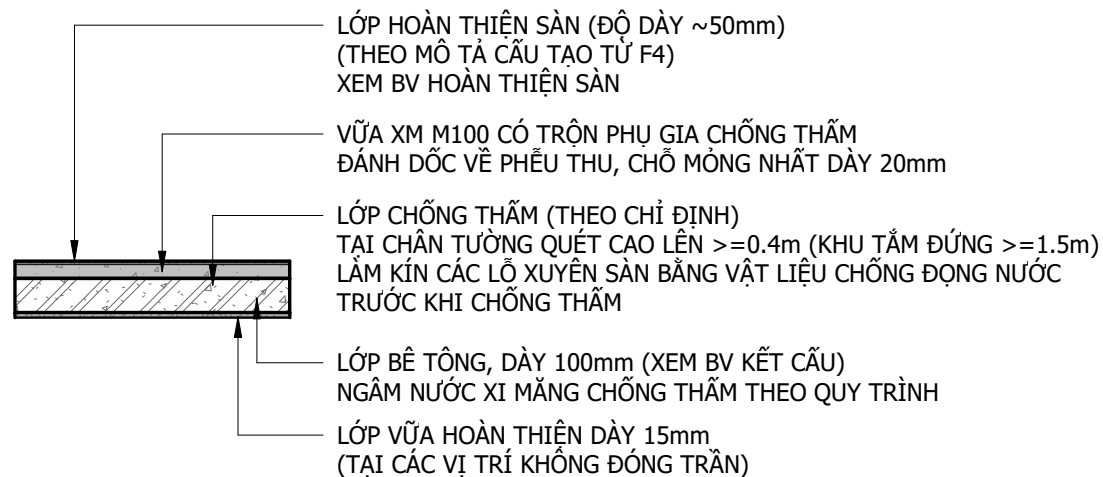

(VỊ TRÍ KHU VỆ SINH TẦNG 2)

CẤU TẠO SÀN WC TẦNG 2

1 : 20

THỐNG KÊ SÀN ĐIỂN HÌNH



TẦNG	LOẠI SÀN	DIỆN TÍCH	THỂ TÍCH	MÔ TẢ CẤU TẠO CƠ BẢN
TẦNG 1	F0	89.23 m ²	8.923 m ³	SÀN BÊ TÔNG CỐT THÉP (CẤU TẠO THEO BV KẾT CẤU)
TẦNG 1	F0-e	43.99 m ²	4.399 m ³	
TẦNG 1	F1	47.51 m ²	2.376 m ³	SÀN HOÀN THIÊN ĐÁ GRANITE 600X600, MÀU KEM SÁNG
TẦNG 1	F2	47.33 m ²	1.656 m ³	SÀN HOÀN THIÊN ĐÁ GRANITE 600X600, CHỐNG TRƯỢT
TẦNG 1	F3	25.03 m ²	1.252 m ³	SÀN GỖ CÔNG NGHIỆP, MÀU XÁM NHẠT
TẦNG 1	F4	8.98 m ²	0.449 m ³	SÀN HOÀN THIÊN GẠCH CERAMIC 400X400, CÓ LỚP CHỐNG THẤM
TẦNG 1	F5	3.15 m ²	0.103 m ³	SÀN HOÀN THIÊN GẠCH CERAMIC 400X400, CHỐNG TRƯỢT
TẦNG 1	F9	1.45 m ²	0.051 m ³	SÀN HOÀN THIÊN ĐÁ GRANITE MÀU XÁM ĐẬM, LÁT TRANG TRÍ
TẦNG 1	F10	7.94 m ²	0.397 m ³	NỀN VƯỜN TIỂU CẢNH TRONG NHÀ
TẦNG 1	F11	2.99 m ²	0.150 m ³	SÀN HOÀN THIÊN ĐÁ GRANITE MÀU XÁM ĐẬM, LÁT NGÀNH CỬA
TẦNG 2	F0	65.16 m ²	6.516 m ³	SÀN BÊ TÔNG CỐT THÉP (CẤU TẠO THEO BV KẾT CẤU)
TẦNG 2	F0-e	14.77 m ²	1.477 m ³	
TẦNG 2	F1	34.62 m ²	1.714 m ³	SÀN HOÀN THIÊN ĐÁ GRANITE 600X600, MÀU KEM SÁNG
TẦNG 2	F2	17.54 m ²	0.564 m ³	SÀN HOÀN THIÊN ĐÁ GRANITE 600X600, CHỐNG TRƯỢT
TẦNG 2	F3	29.21 m ²	1.460 m ³	SÀN GỖ CÔNG NGHIỆP, MÀU XÁM NHẠT
TẦNG 2	F4	3.17 m ²	0.158 m ³	SÀN HOÀN THIÊN GẠCH CERAMIC 400X400, CÓ LỚP CHỐNG THẤM
TẦNG 2	F5	5.34 m ²	0.186 m ³	SÀN HOÀN THIÊN GẠCH CERAMIC 400X400, CHỐNG TRƯỢT
TẦNG 2	F8	0.94 m ²	0.019 m ³	SÀN HOÀN THIÊN ĐÁ GRANITE MÀU XÁM ĐẬM, LÁT NGÀNH CỬA
TẦNG 2	F11	2.69 m ²	0.135 m ³	SÀN HOÀN THIÊN ĐÁ GRANITE MÀU XÁM ĐẬM, LÁT NGÀNH CỬA
TẦNG 2	Fn	14.51 m ²	2.901 m ³	SÀN ĐÔN NỀN BAN CÔNG (THEO BV KẾT CẤU)
CHÂN MÁI	F0	87.91 m ²	8.791 m ³	SÀN BÊ TÔNG CỐT THÉP (CẤU TẠO THEO BV KẾT CẤU)

LƯU Ý VỀ CÔNG TÁC XÂY



- 1. TẠI VỊ TRÍ TIẾP GIÁP VỚI CỘT KẾT CẤU, CỬ 5 HÀNG GẠCH ỐNG PHẢI CÓ BẮT SẮT NEO THEO CHIỀU DÀY TƯỜNG (1 VỚI TƯỜNG DÀY 100mm, 2 VỚI TƯỜNG DÀY 200mm). CHI TIẾT SẮT NEO XEM BV KẾT CẤU.
- 2. CẦU GẠCH:
 - ĐỐI VỚI TƯỜNG DÀY 200mm BAO NGOÀI QUY CÁCH 5 HÀNG GẠCH ỐNG PHẢI CẦU 1 HÀNG GẠCH ĐẶC.
 - ĐỐI VỚI TƯỜNG GẮN DÀY 200mm BÊN TRONG, 5 HÀNG GẠCH ỐNG PHẢI CẦU 1 HÀNG GẠCH (CÓ THỂ DÙNG GẠCH ỐNG HOẶC GẠCH ĐẶC)
- 3. TƯỜNG NGĂN KHU VỆ SINH: CHÂN TƯỜNG XÂY ÍT NHẤT 3 HÀNG GẠCH ĐẶC.
- 4. VỊ TRÍ CHÈN GẠCH ĐỈNH TƯỜNG: SỬ DỤNG GẠCH ĐẶC XẾP NGHIÊNG VỪA ĐỦ, CHÈN VỮA CHẶT.
- 5. VỊ TRÍ CỬA (CỬA ĐI, CỬA SỔ, LỖ THÔNG, LỖ XUYỀN TƯỜNG):
 - CÔNG TÁC XÂY ĐƯỢC THỰC HIỆN ĐẾN LANH TÔ CỬA- SAU ÍT NHẤT 12H (BÊ TÔNG LANH TÔ KHÔ) MỚI ĐƯỢC TIẾN HÀNH XÂY TIẾP.
 - BÊ CỬA SỔ XÂY BẰNG 1 HÀNG GẠCH ĐẶC.
 - TOÀN BỘ CẠNH BÊN CÁC Ô CỬA XÂY GẠCH ĐẶC.

LƯU Ý VỀ CÔNG TÁC TÔ TRÁT


- ĐÓNG LƯỚI MẶT CÁO TẠI VỊ TRÍ TIẾP GIÁP GIỮA TƯỜNG GẠCH VỚI KẾT CẤU BÊ TÔNG, CÁC VỊ TRÍ ỐNG ĐI ÂM TƯỜNG (LỖ XUYỀN ỐNG, RÃNH XẾ TƯỜNG, ...) THEO SUỐT CHIỀU DÀI.
- VỮA XI MẮNG TÔ TRÁT MÁC 75, CÁT VẮNG HẠT MỊN ĐƯỢC XỬ LÝ SẠCH.
- TRƯỚC KHI TÔ TRÁT PHẢI TƯỚI NƯỚC TẠO ẨM CHO BỀ MẶT.
- TOÀN BỘ CÁC LỖ GẠCH MẶT NGOÀI (NẾU CÓ) PHẢI ĐƯỢC BỊT KÍN TRƯỚC KHI TÔ.
- CÁC VỊ TRÍ CÓ JOINT ÂM TƯỜNG, ĐỘ DÀY LỚP TRÁT TỐI THIỂU 5mm.
- GẠCH ỐP CHÂN TƯỜNG (NẾU CÓ) PHẪNG BỀ MẶT VỚI VỮA TÔ HOÀN THIỆN TƯỜNG.
- TẠI CÁC NỀN/SÀN CÓ ĐỘ DỐC, LỚP VỮA TÔ TẠO DỐC Ở VỊ TRÍ CUỐI DỐC CÓ ĐỘ DÀY TỐI THIỂU 20mm.

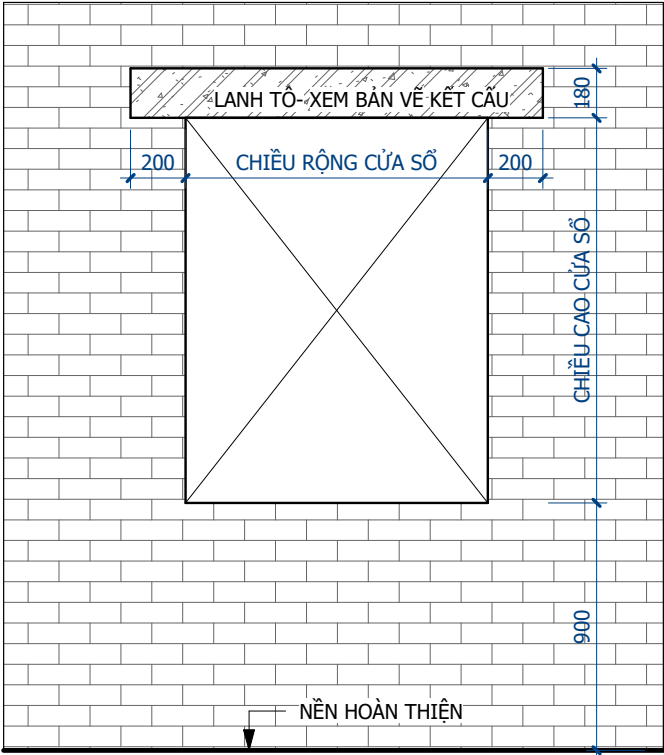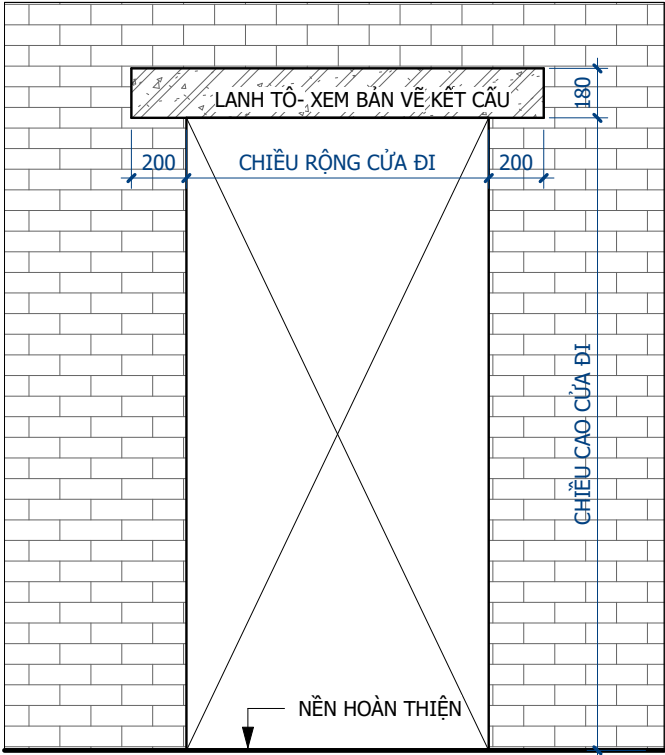

VỊ TRÍ VÀ CHIỀU DÀI LANH TÔ CỬA
1 : 25

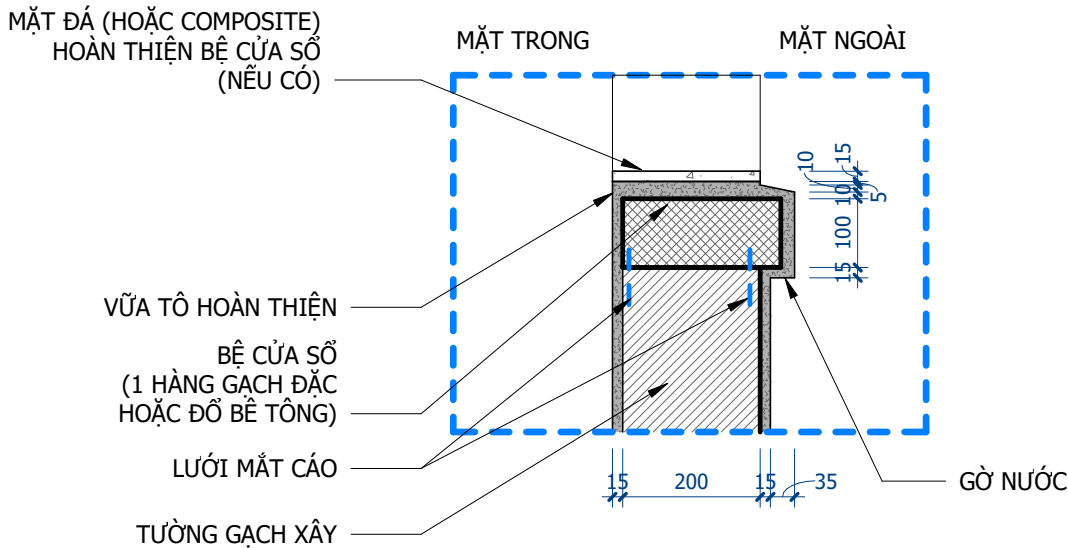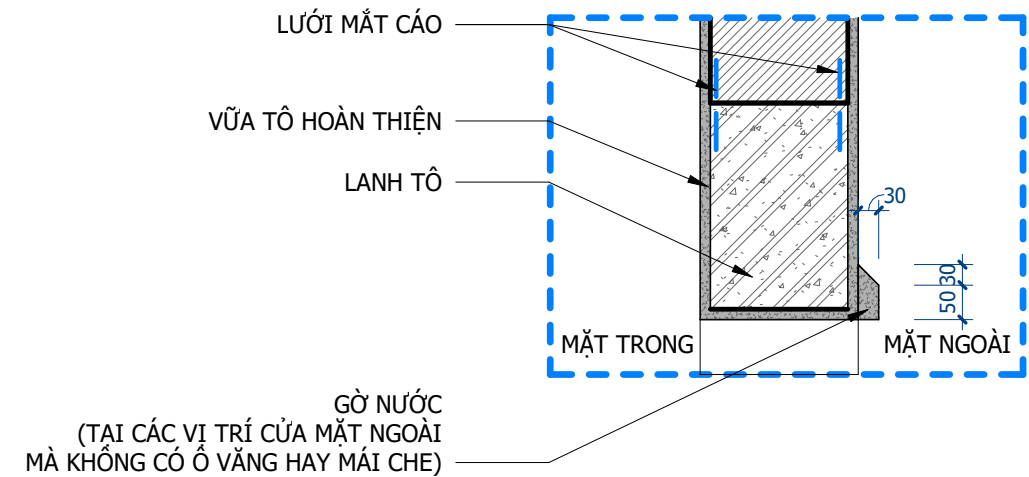


CẤU TẠO ĐẦU CỬA-BÊ CỬA
1 : 10

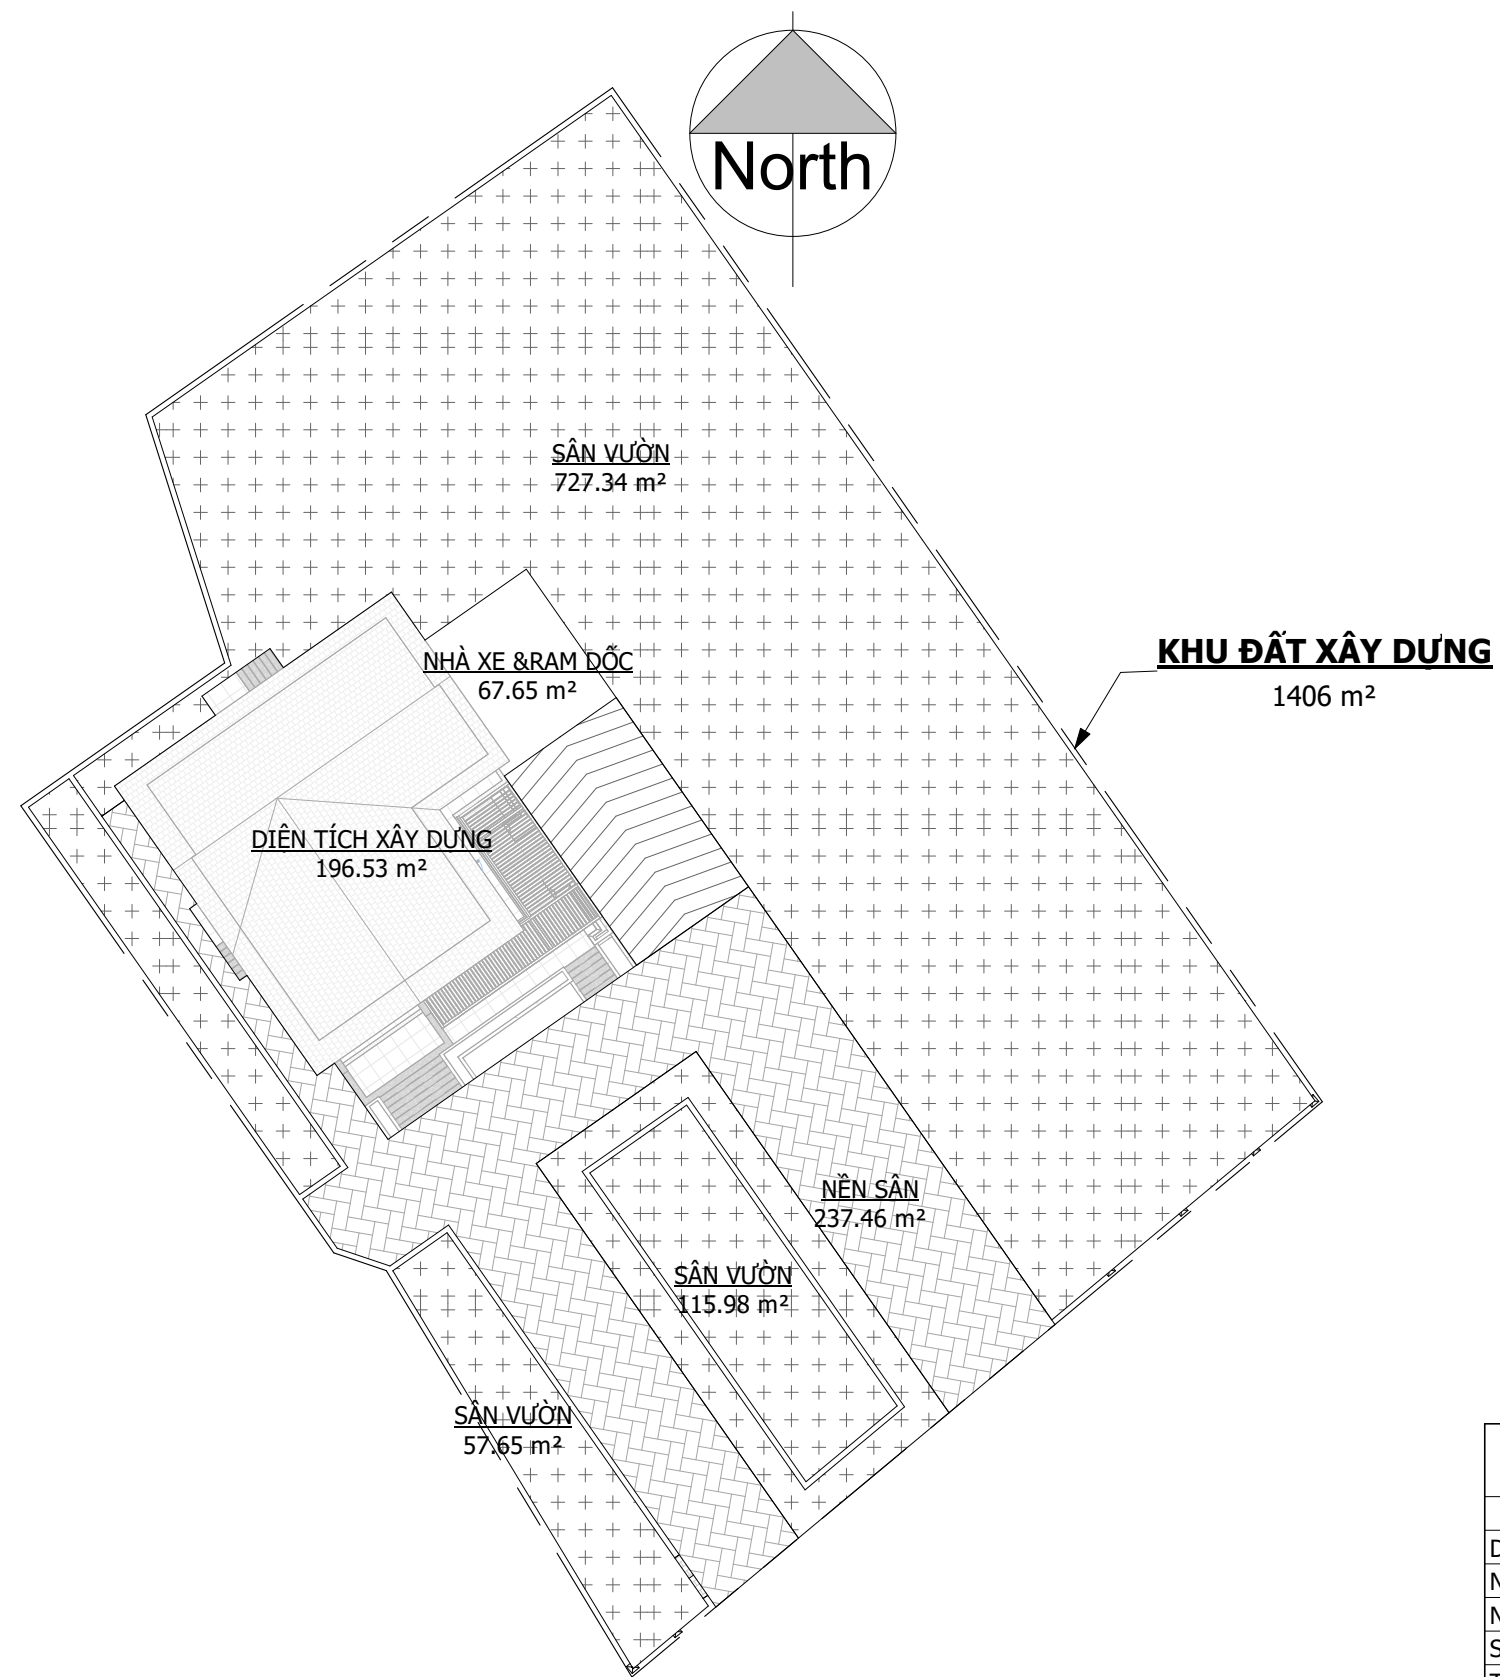


THỐNG KÊ SỬ DỤNG ĐẤT		
LOẠI HÌNH SỬ DỤNG	DIỆN TÍCH	TỈ LỆ %
DIỆN TÍCH XÂY DỰNG	196.53 m ²	14%
NHÀ XE & RAM DỐC	67.65 m ²	5%
NỀN SÂN	237.46 m ²	17%
SÂN VƯỜN	900.96 m ²	64%
TỔNG CỘNG	1402.61 m ²	


1 MẶT BẰNG TỔNG THỂ
1 : 250

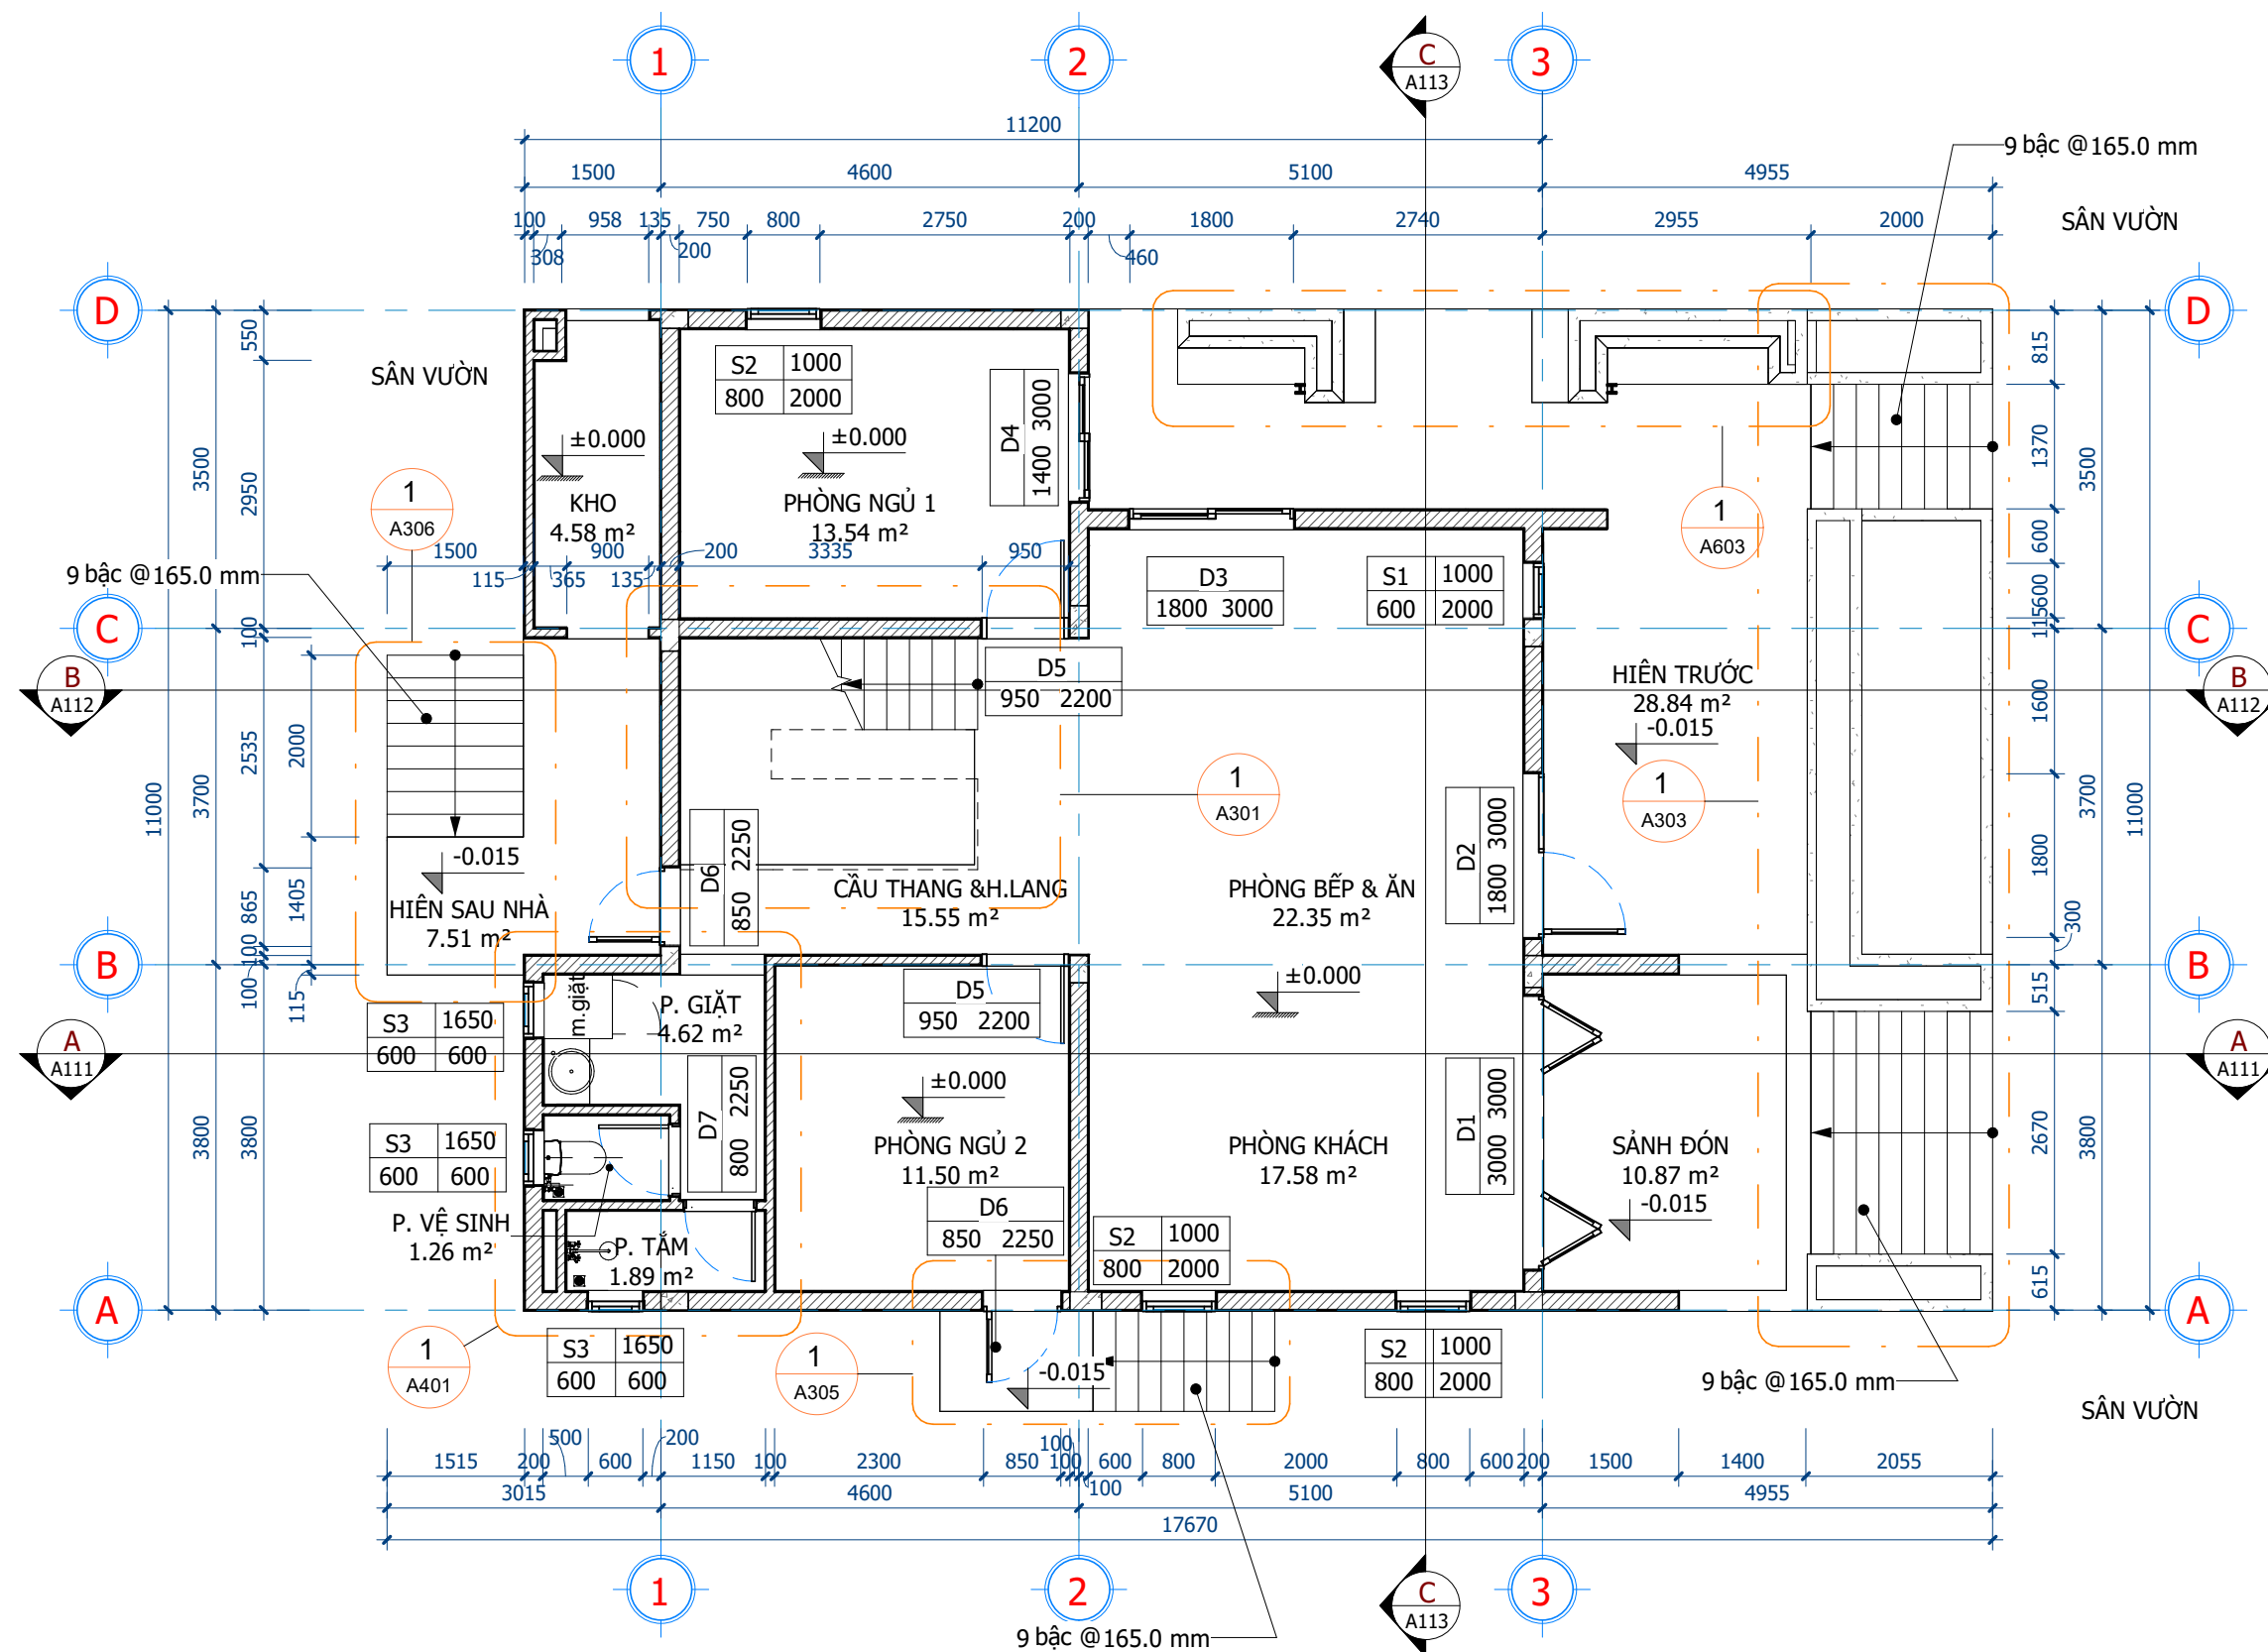


1 MẶT BẰNG KÍCH THƯỚC TẦNG 1
1 : 75

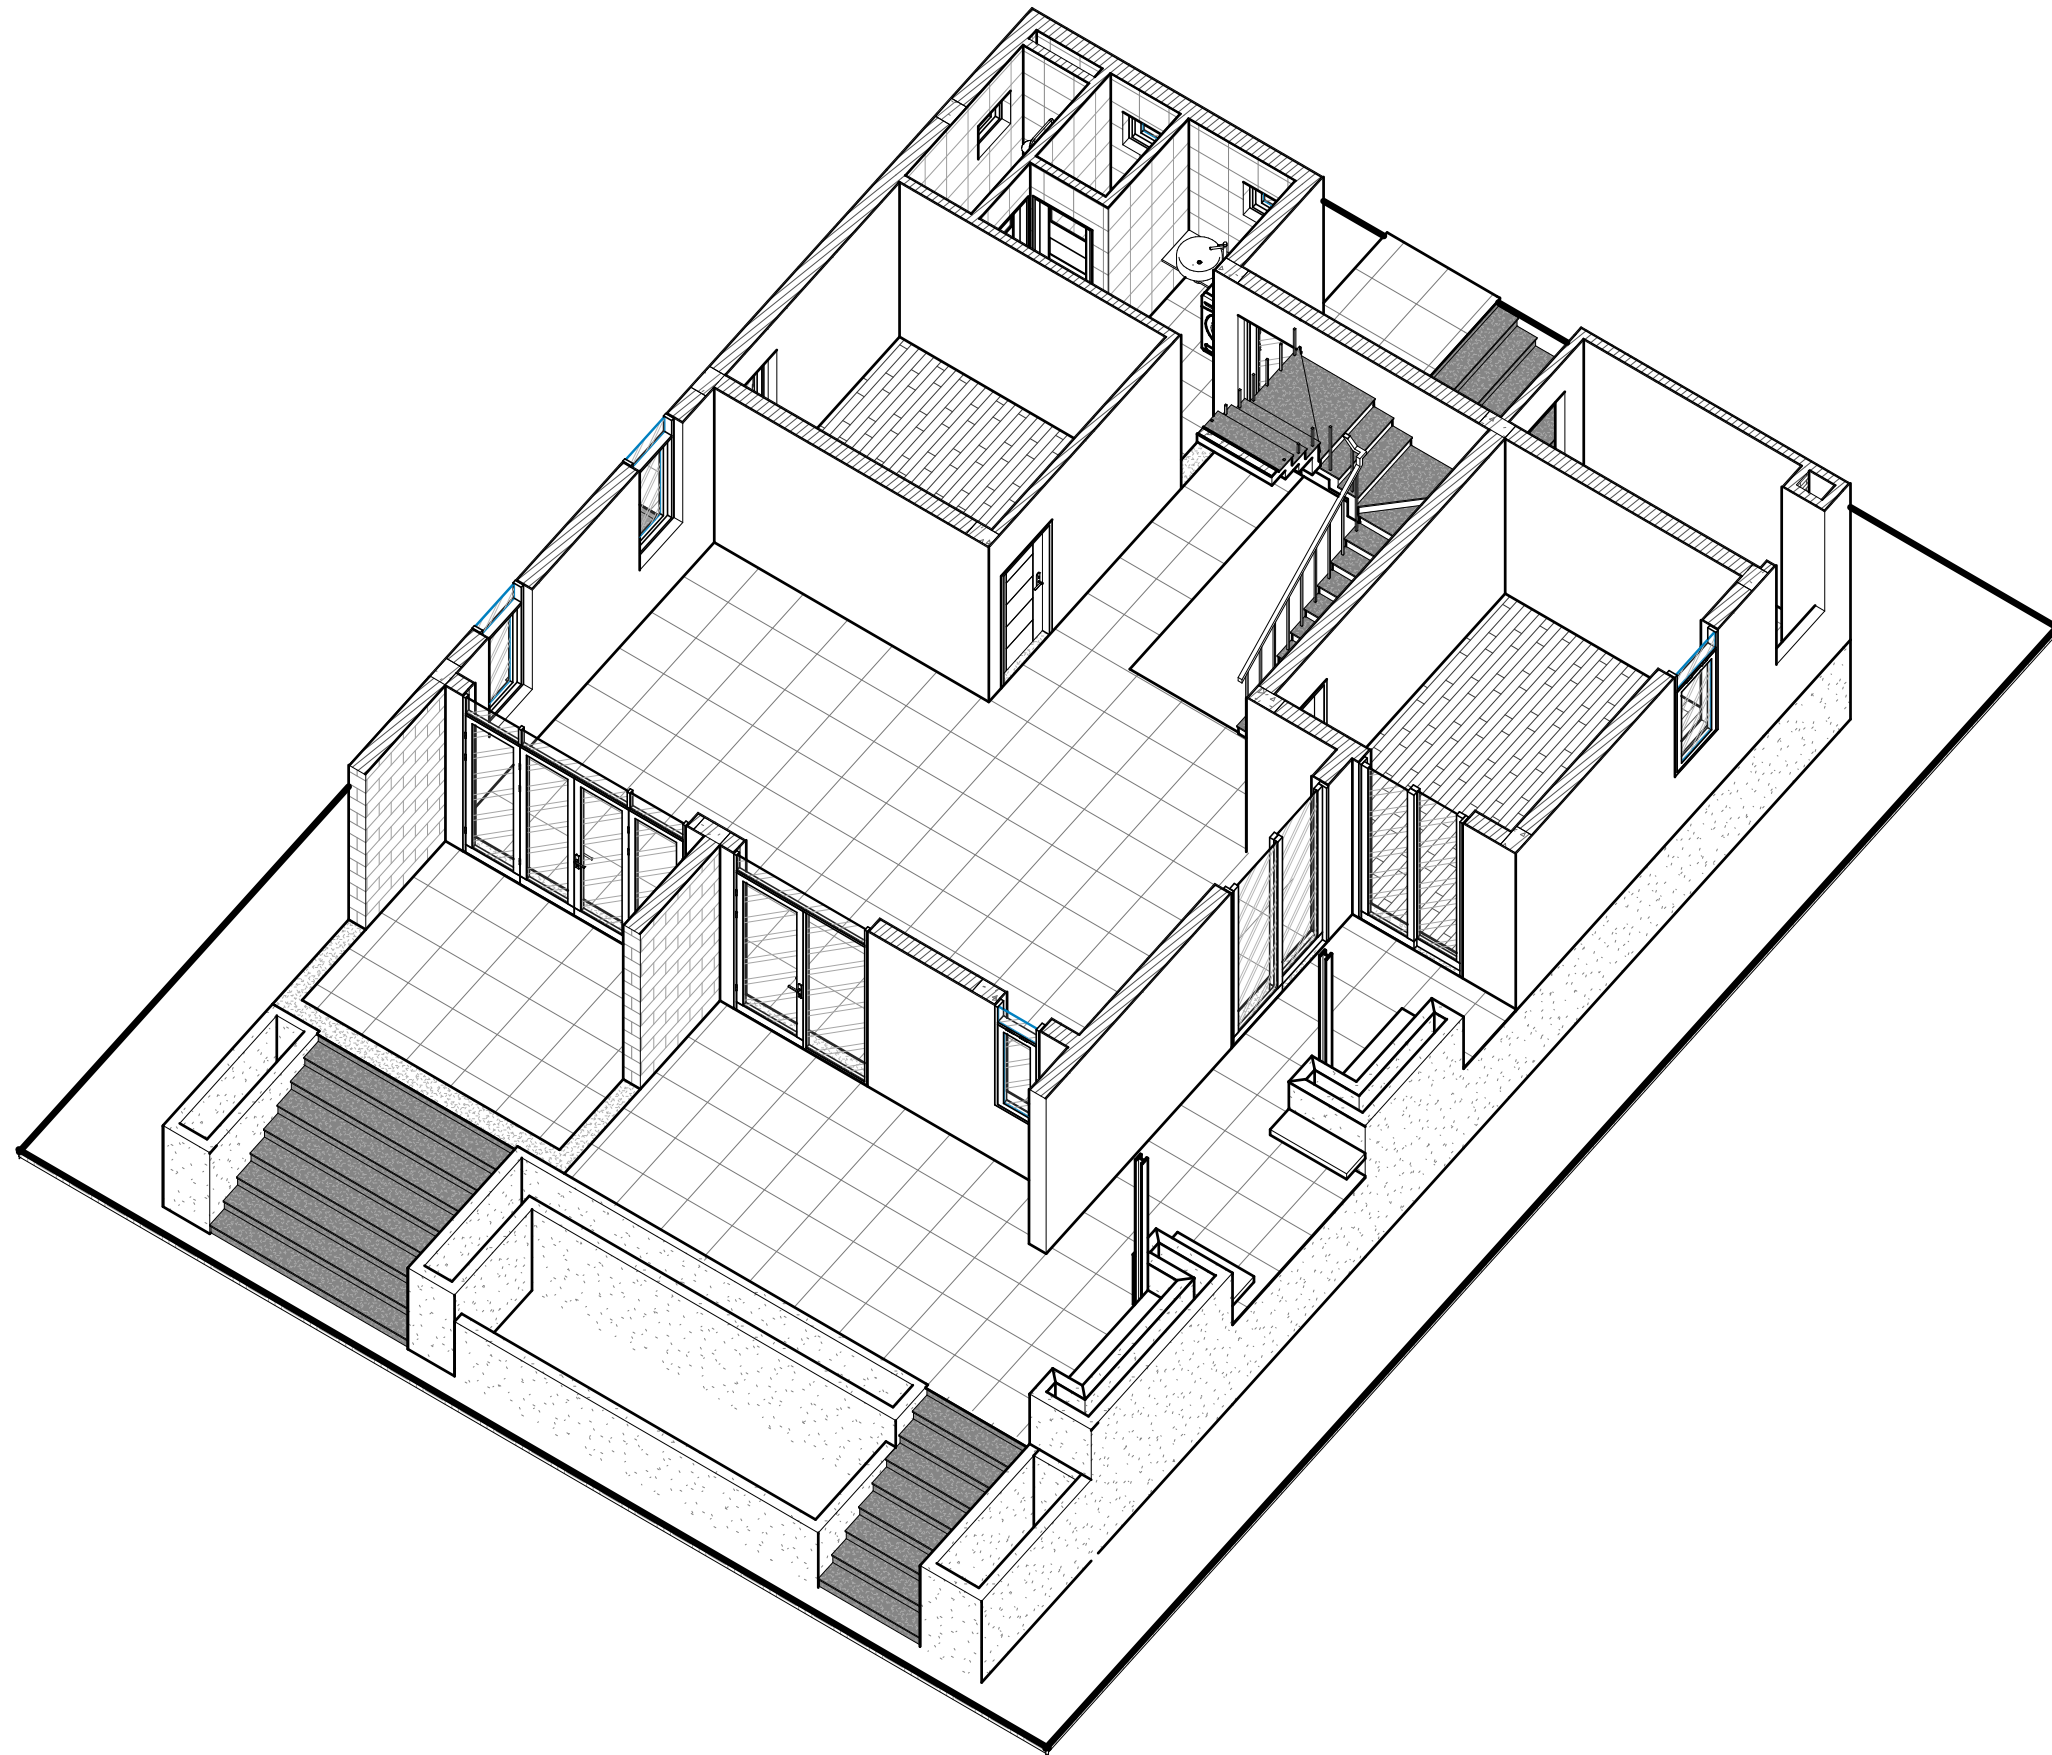


1 PHỐI CẢNH TẦNG 1

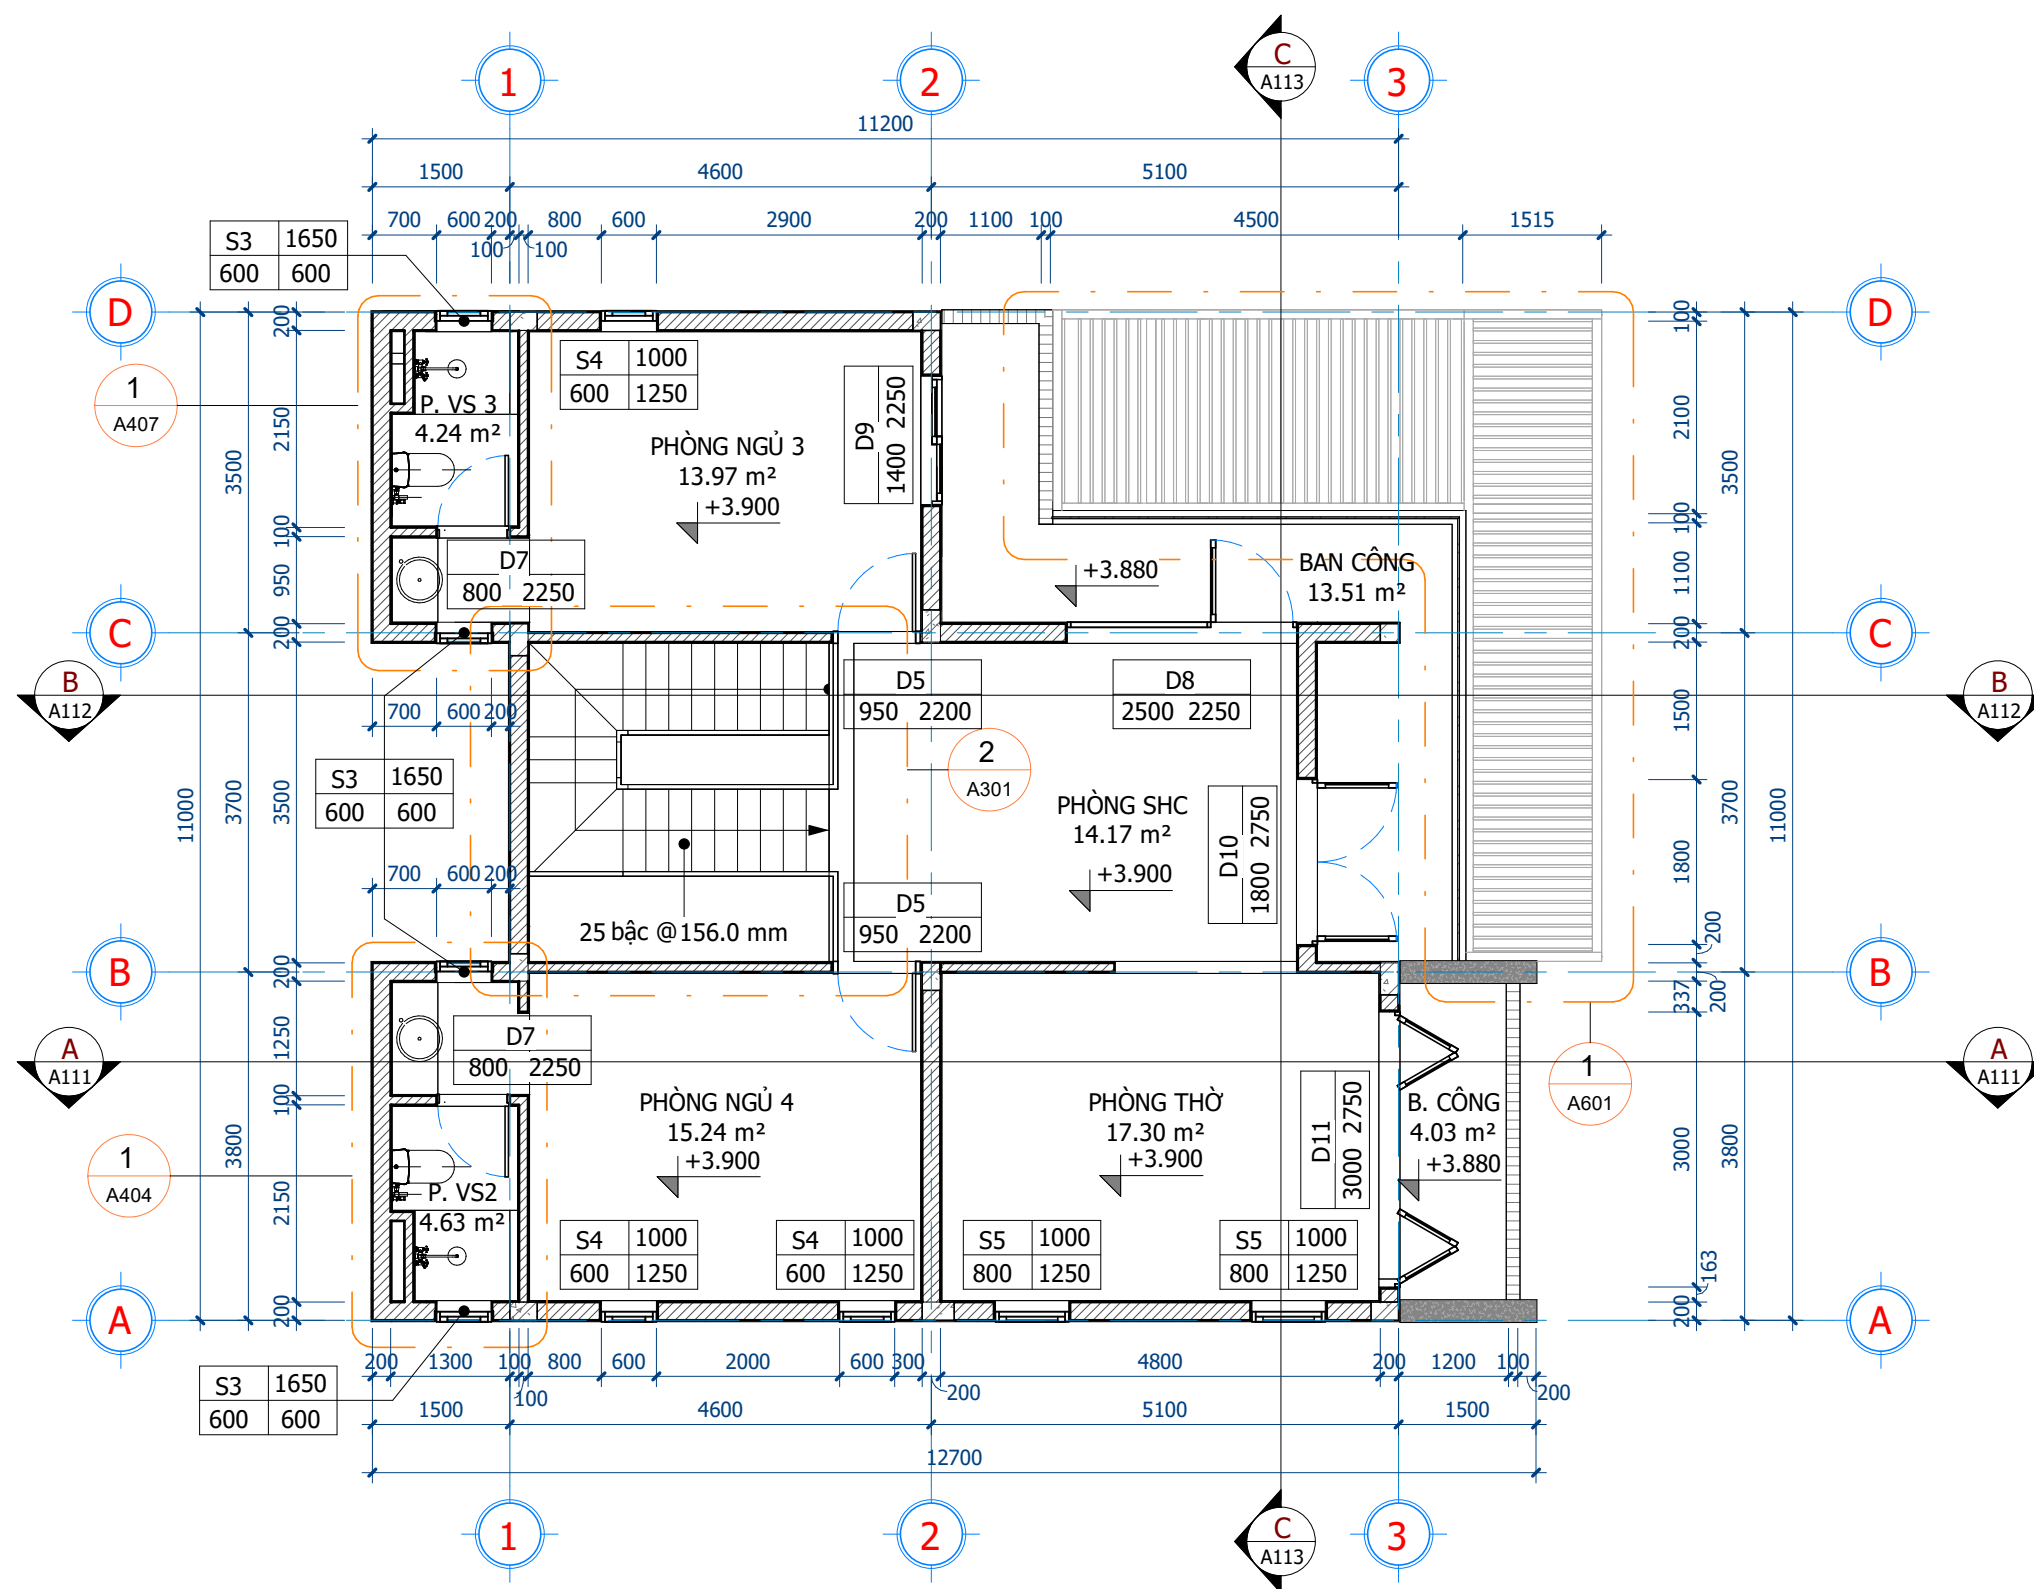


1 MẶT BẰNG KÍCH THƯỚC TẦNG 2
1 : 75

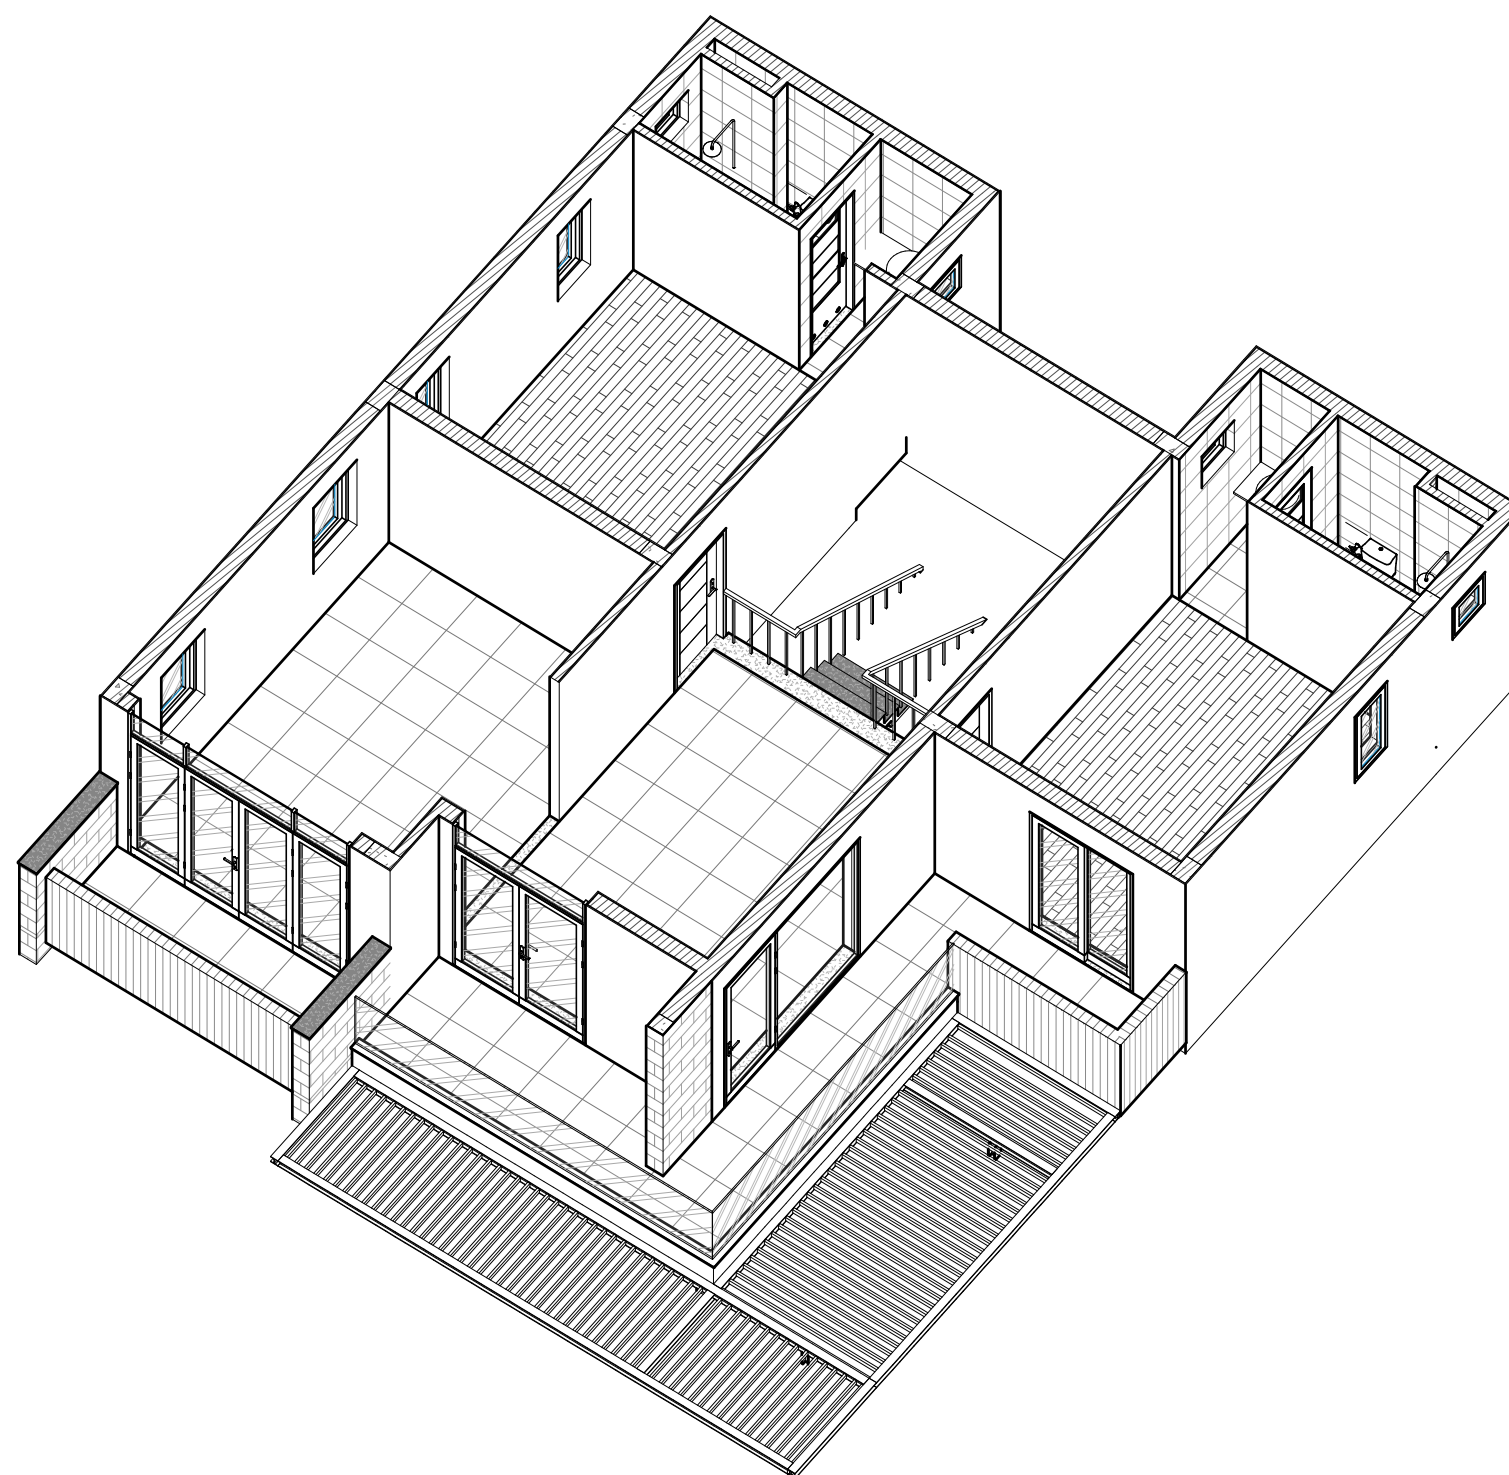


① PHỐI CẢNH TẦNG 2

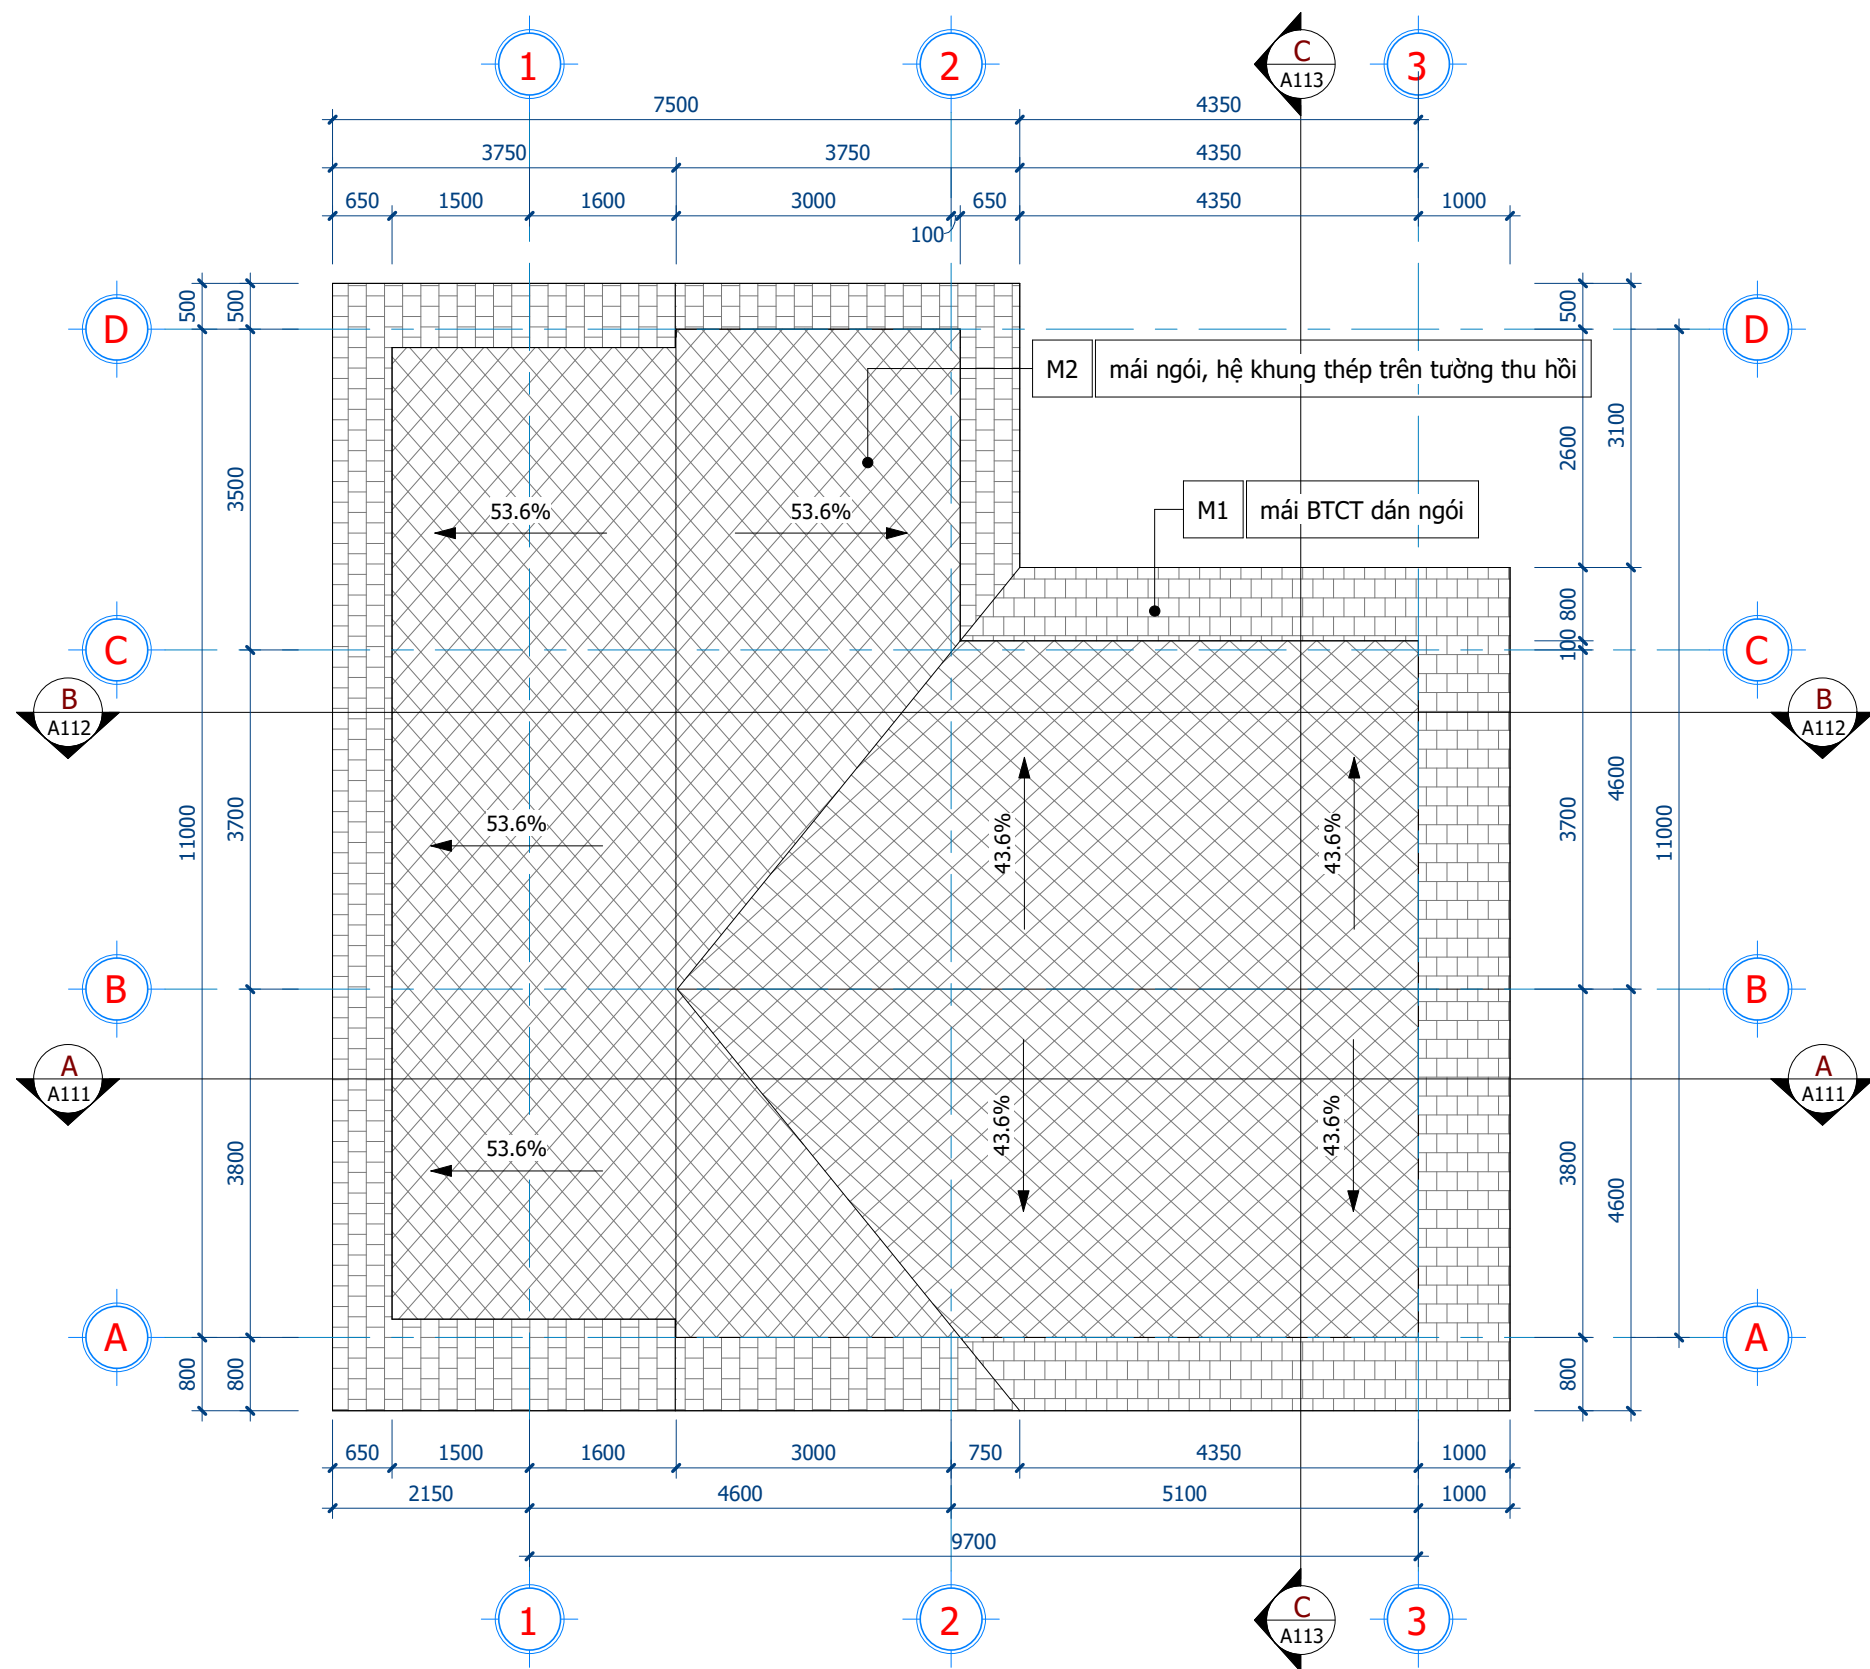

1 MẶT BẰNG KÍCH THƯỚC MÁI
1 : 75

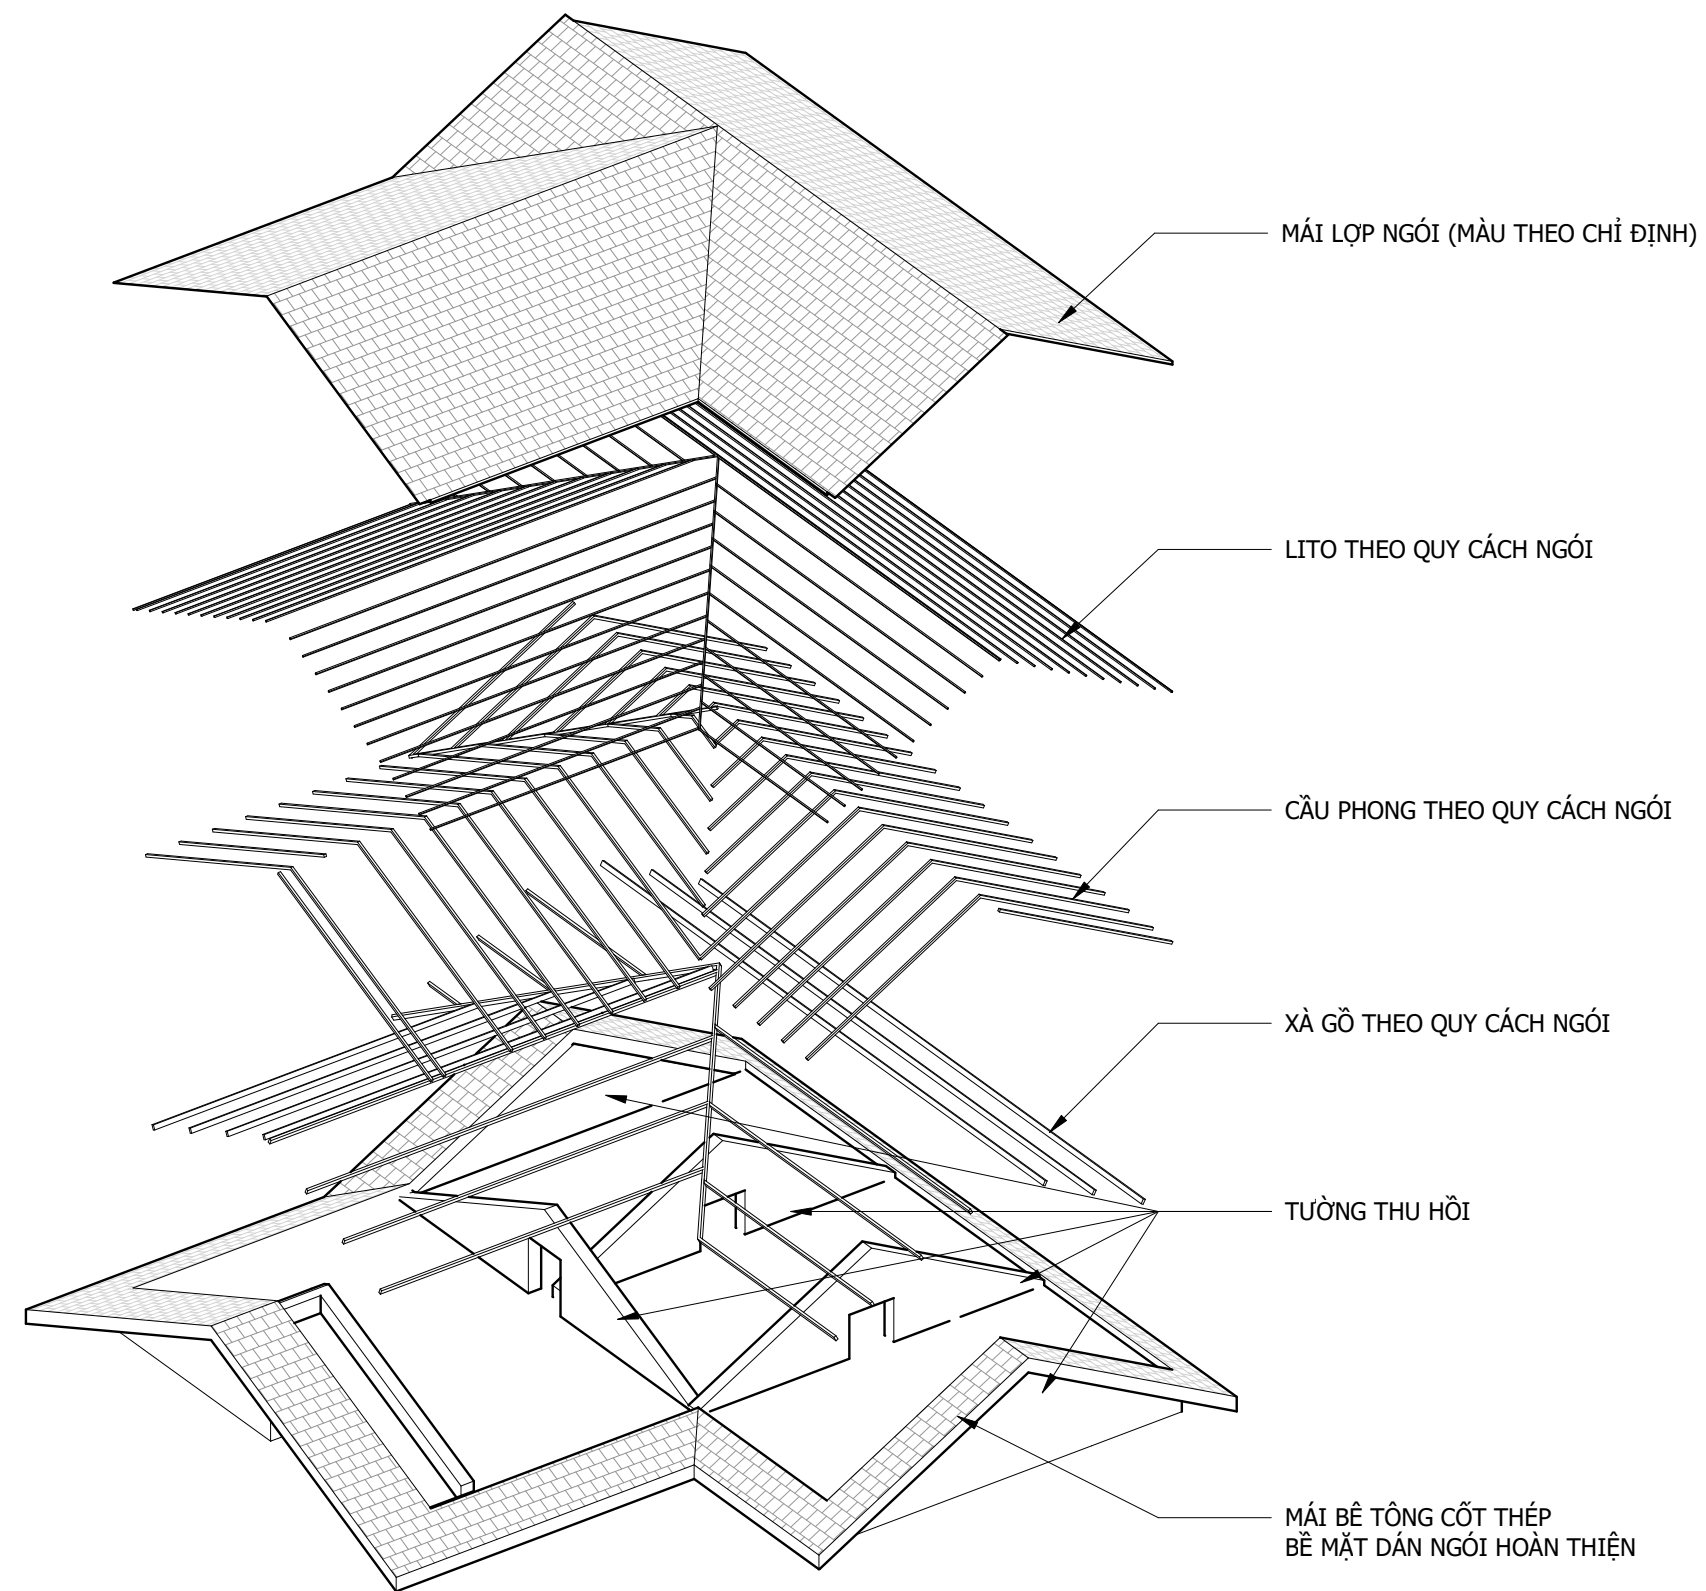

1 HỆ KẾT CẤU MÁI

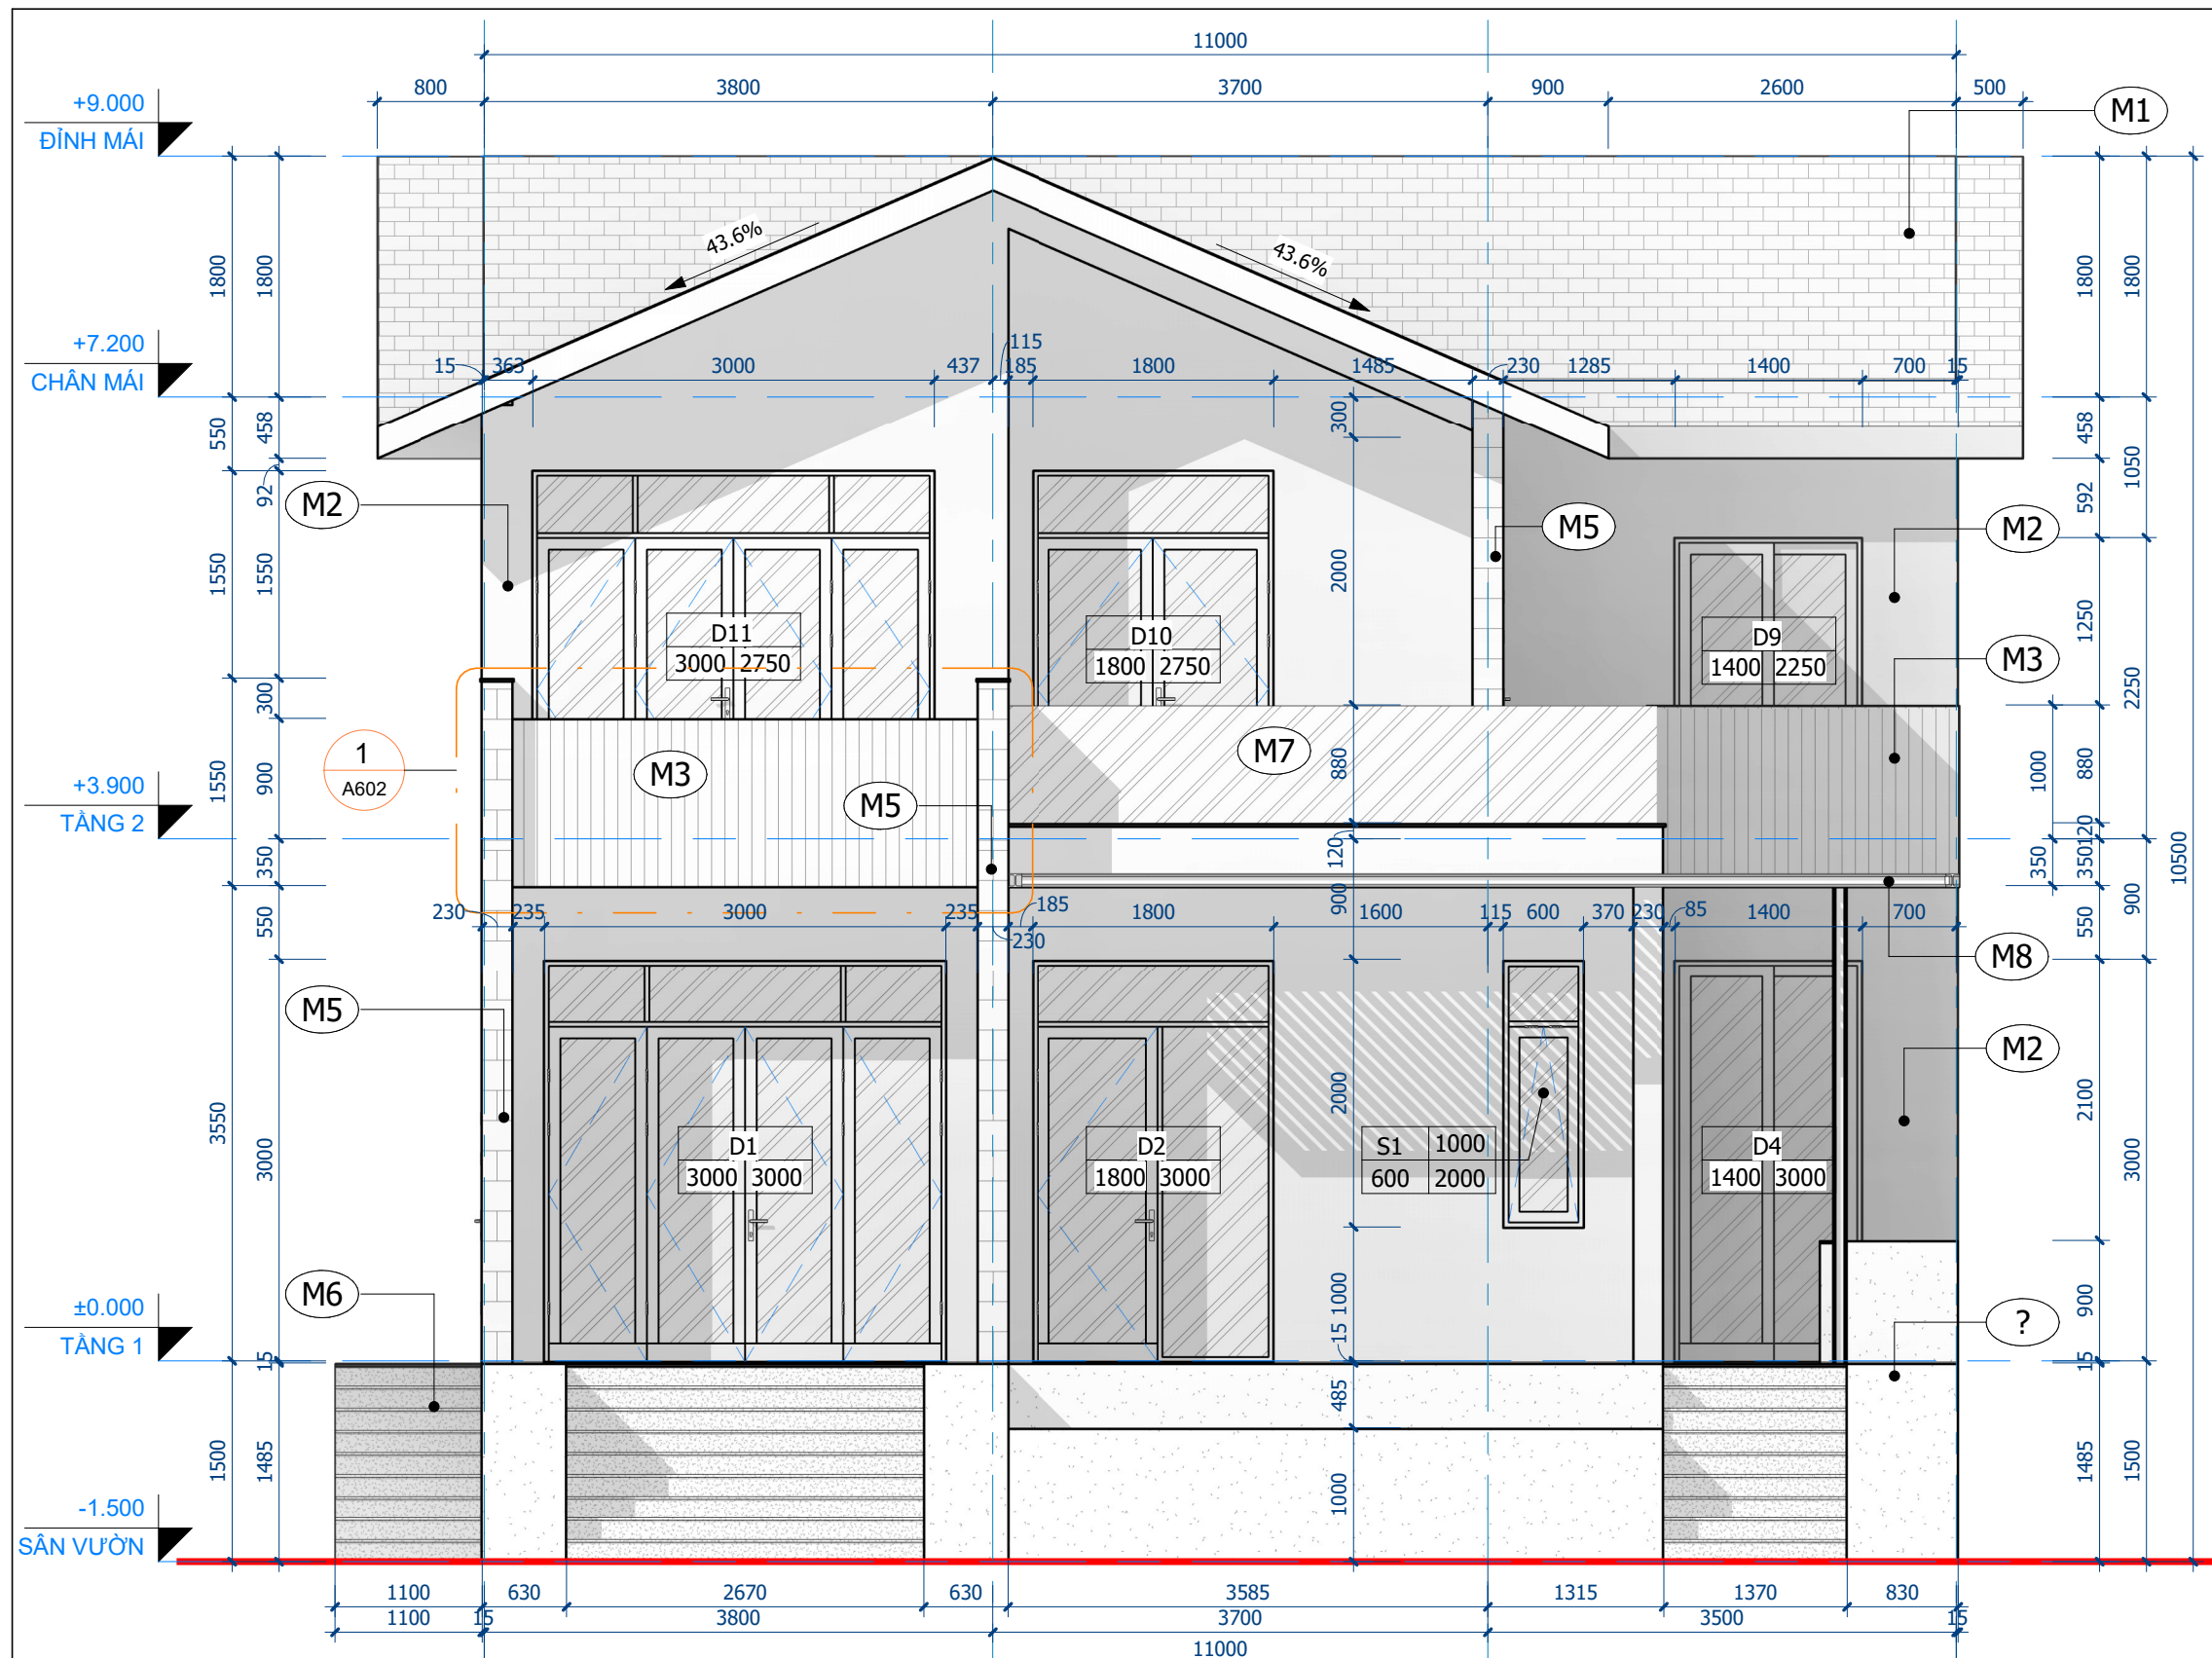


GHI CHÚ VẬT LIỆU-MẶT ĐỨNG	
MÃ	MÔ TẢ CHI TIẾT
M1	NGÓI LỢP (MẪU CHỌN THỰC TẾ)
M2	TƯỜNG SƠN NƯỚC MÀU KEM
M3	ỒP CONWOOD MÀU XÁM NHẠT
M4	TƯỜNG SƠN GIÁ BỀ TỔNG


GHI CHÚ VẬT LIỆU-MẶT ĐỨNG	
MÃ	MÔ TẢ CHI TIẾT
M5	ỒP ĐÁ CHÈ (THEO MẪU)
M6	ĐÁ GRANITE ĐEN
M7	KÍNH CƯỜNG LỰC
M8	SƠN TĨNH ĐIỆN MÀU ĐEN

1 MẶT ĐỨNG TRỰC A-D
1 : 50

KIẾN TRÚC
A107
12/14/21

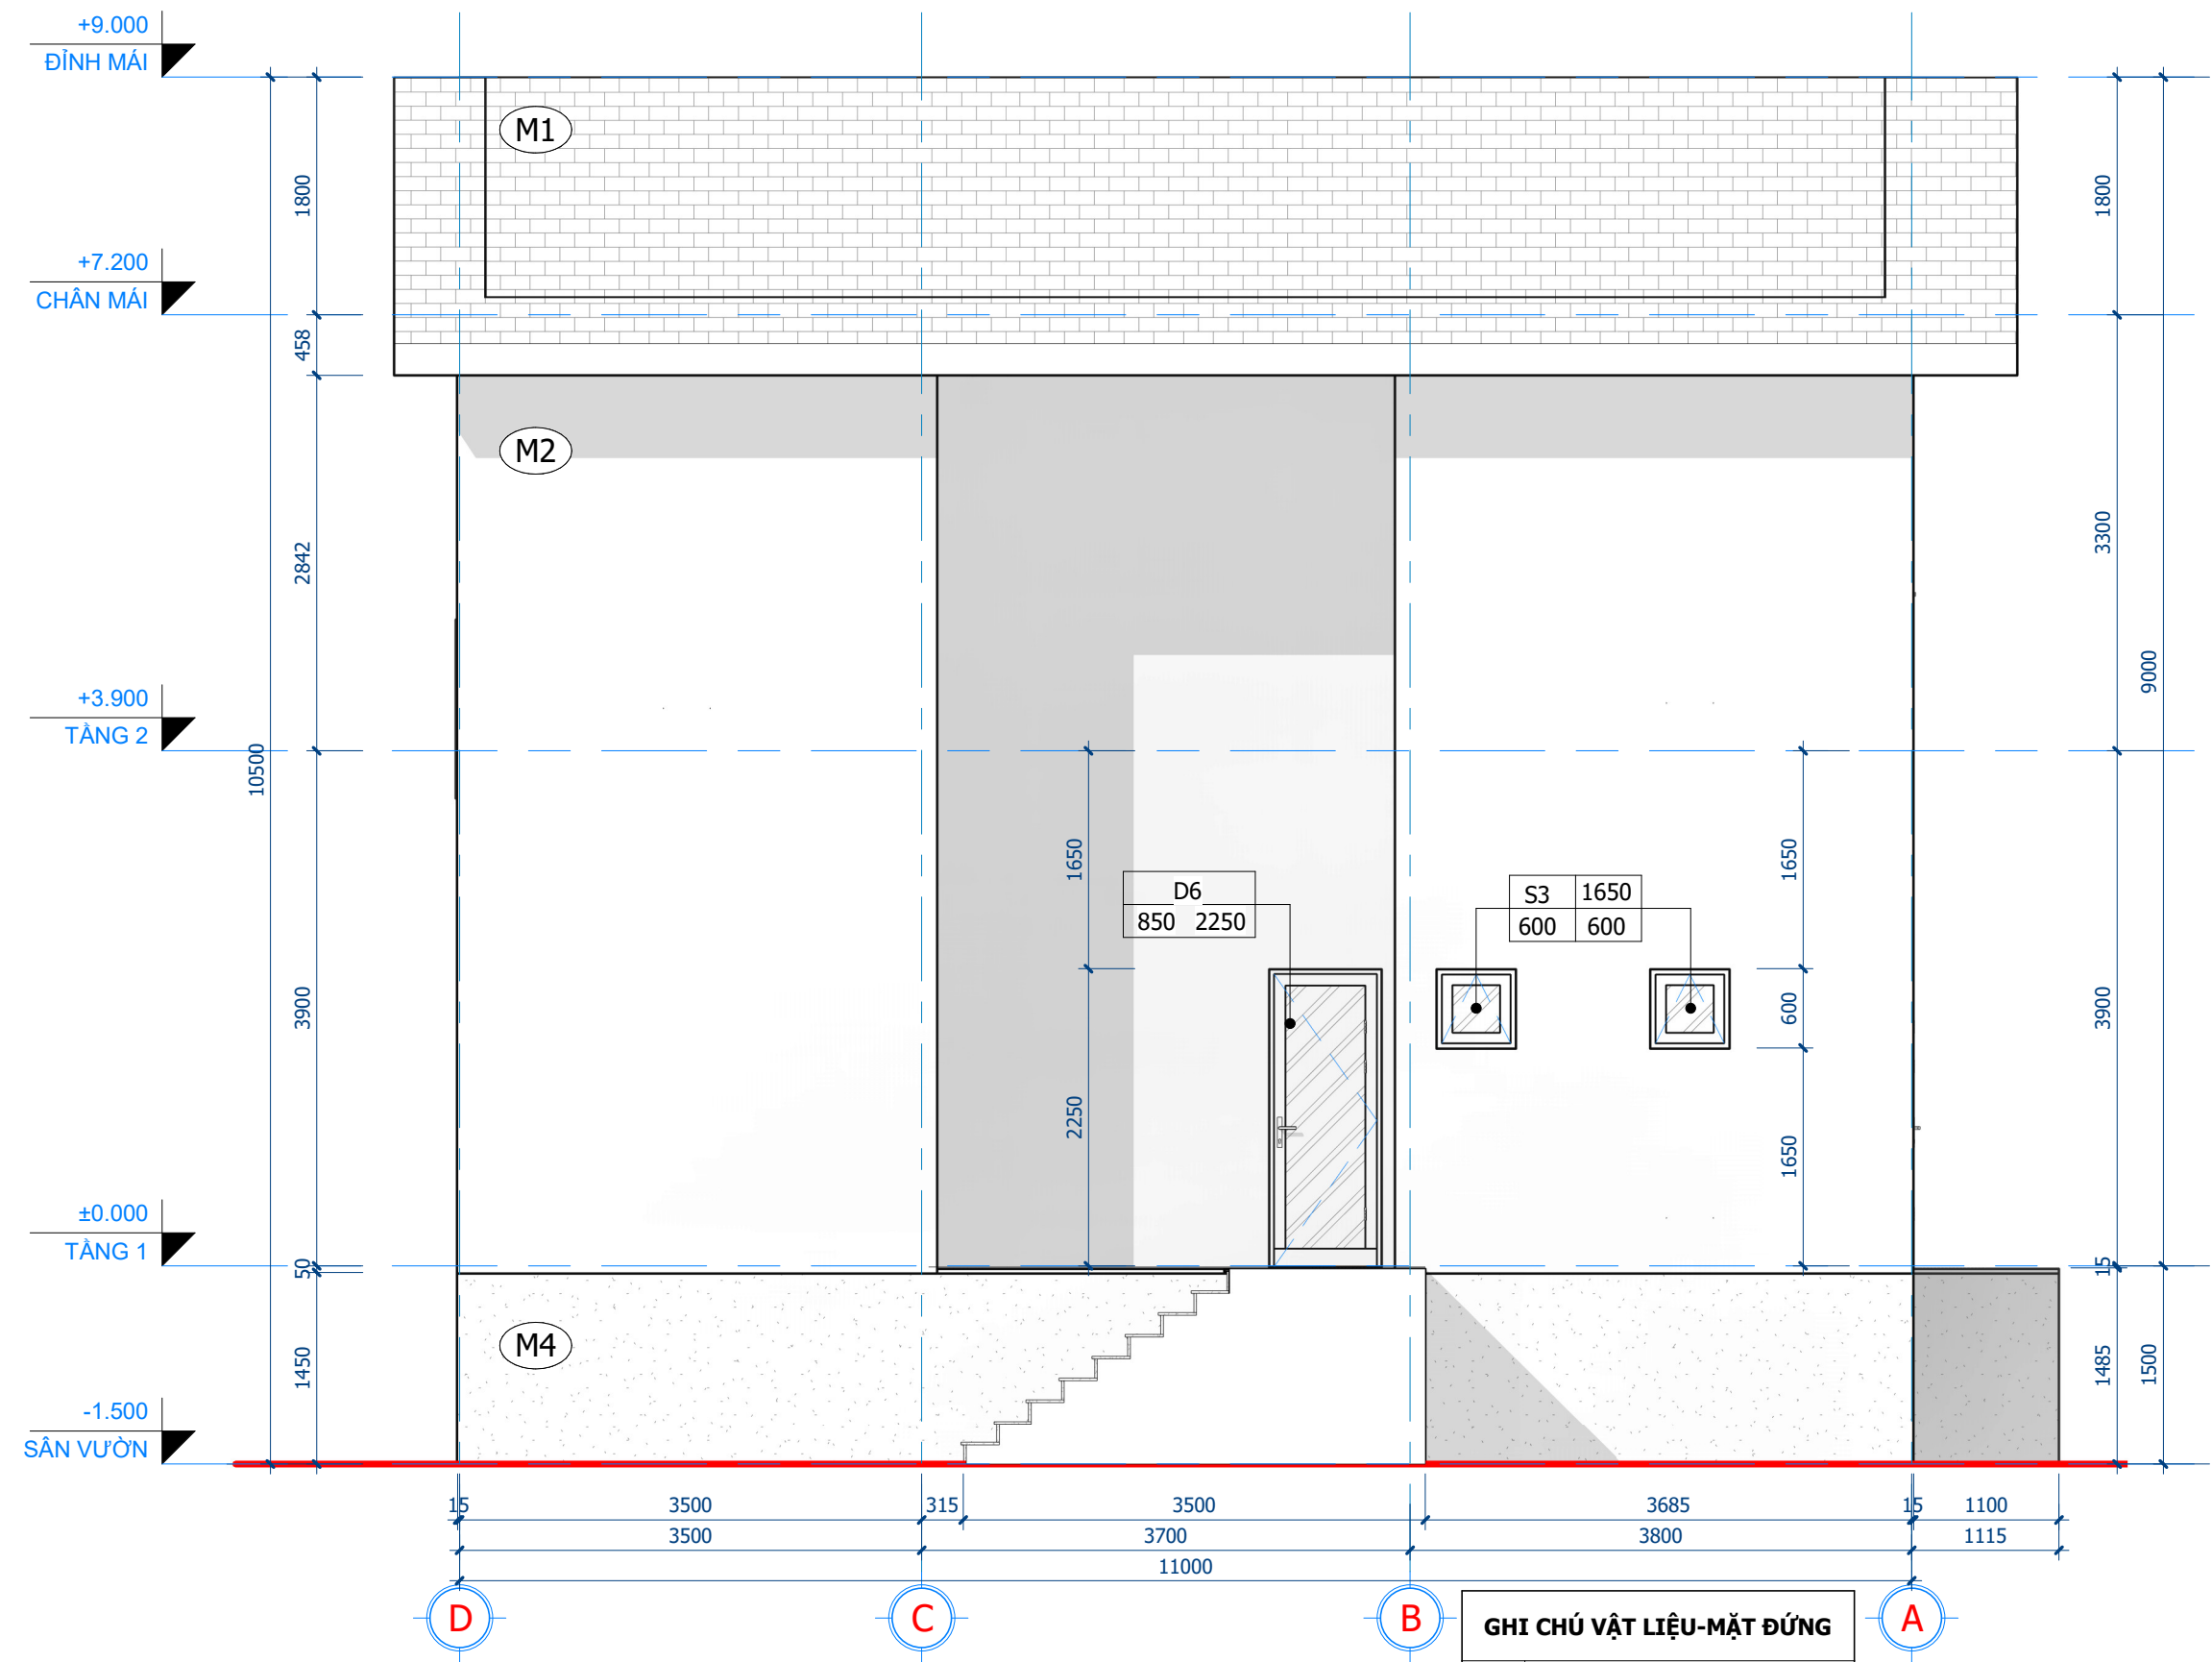


1 MẶT ĐỨNG TRỰC D-A
1 : 50

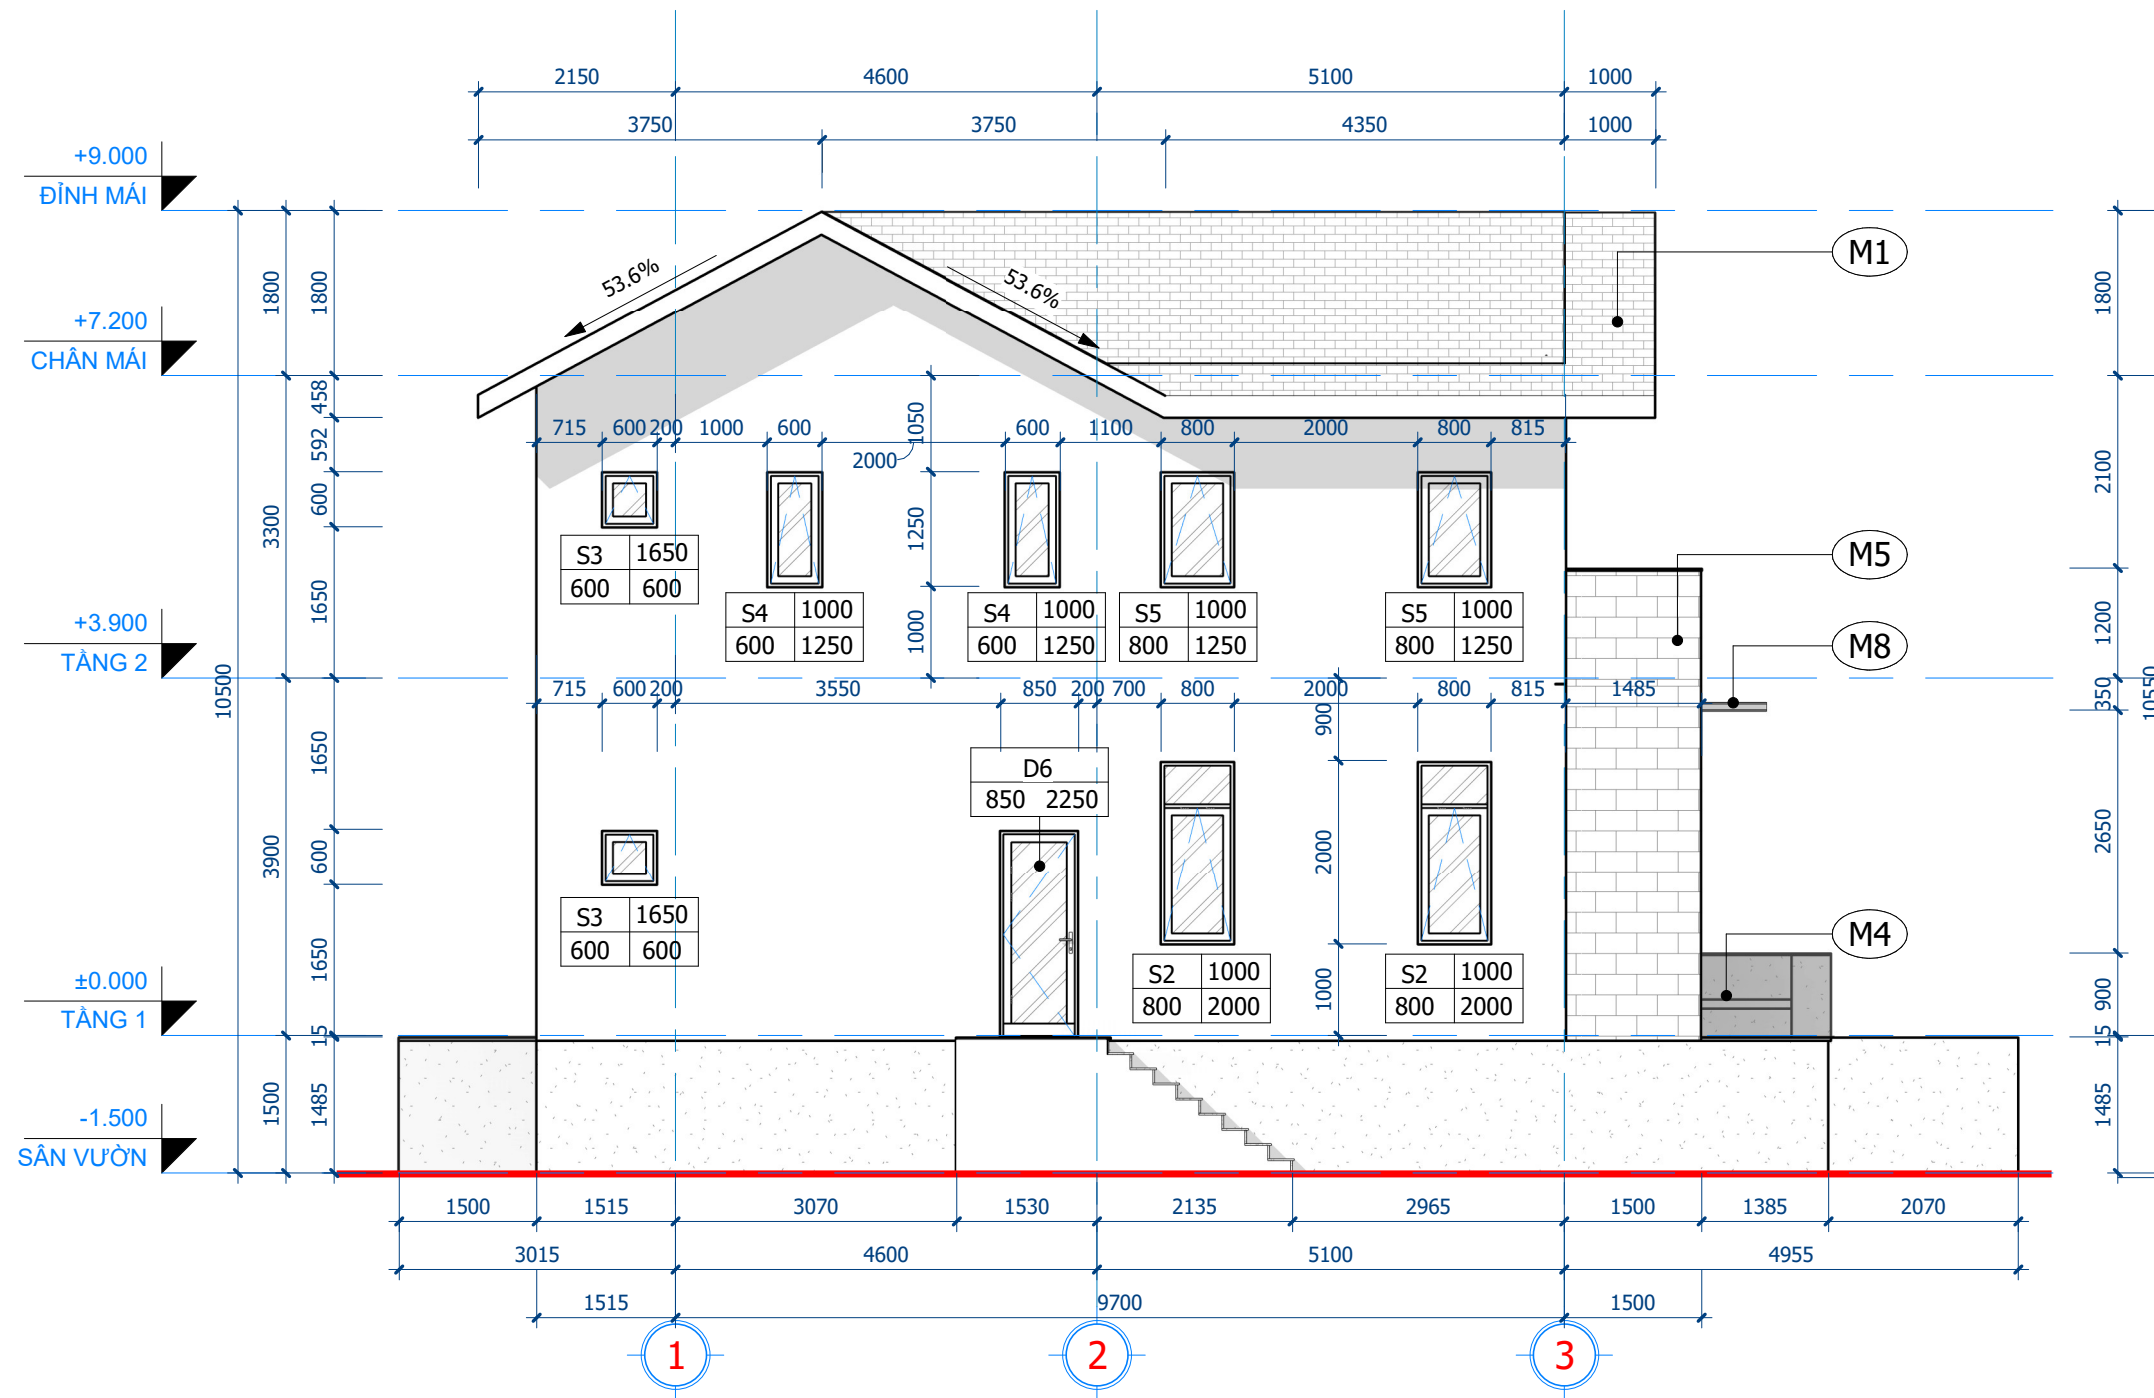

GHI CHÚ VẬT LIỆU-MẶT ĐỨNG	
MÃ	MÔ TẢ CHI TIẾT
M1	NGÓI LỢP (MẪU CHỌN THỰC TẾ)
M2	TƯỜNG SƠN NƯỚC MÀU KEM
M3	ỒP CONWOOD MÀU XÁM NHẠT
M4	TƯỜNG SƠN GIÁ BÊ TÔNG
M5	ỒP ĐÁ CHÉ (THEO MẪU)
M6	ĐÁ GRANITE ĐEN
M7	KÍNH CƯỜNG LỰC
M8	SƠN TĨNH ĐIỆN MÀU ĐEN


1 MẶT ĐỨNG TRỤC 1-3
1 : 75

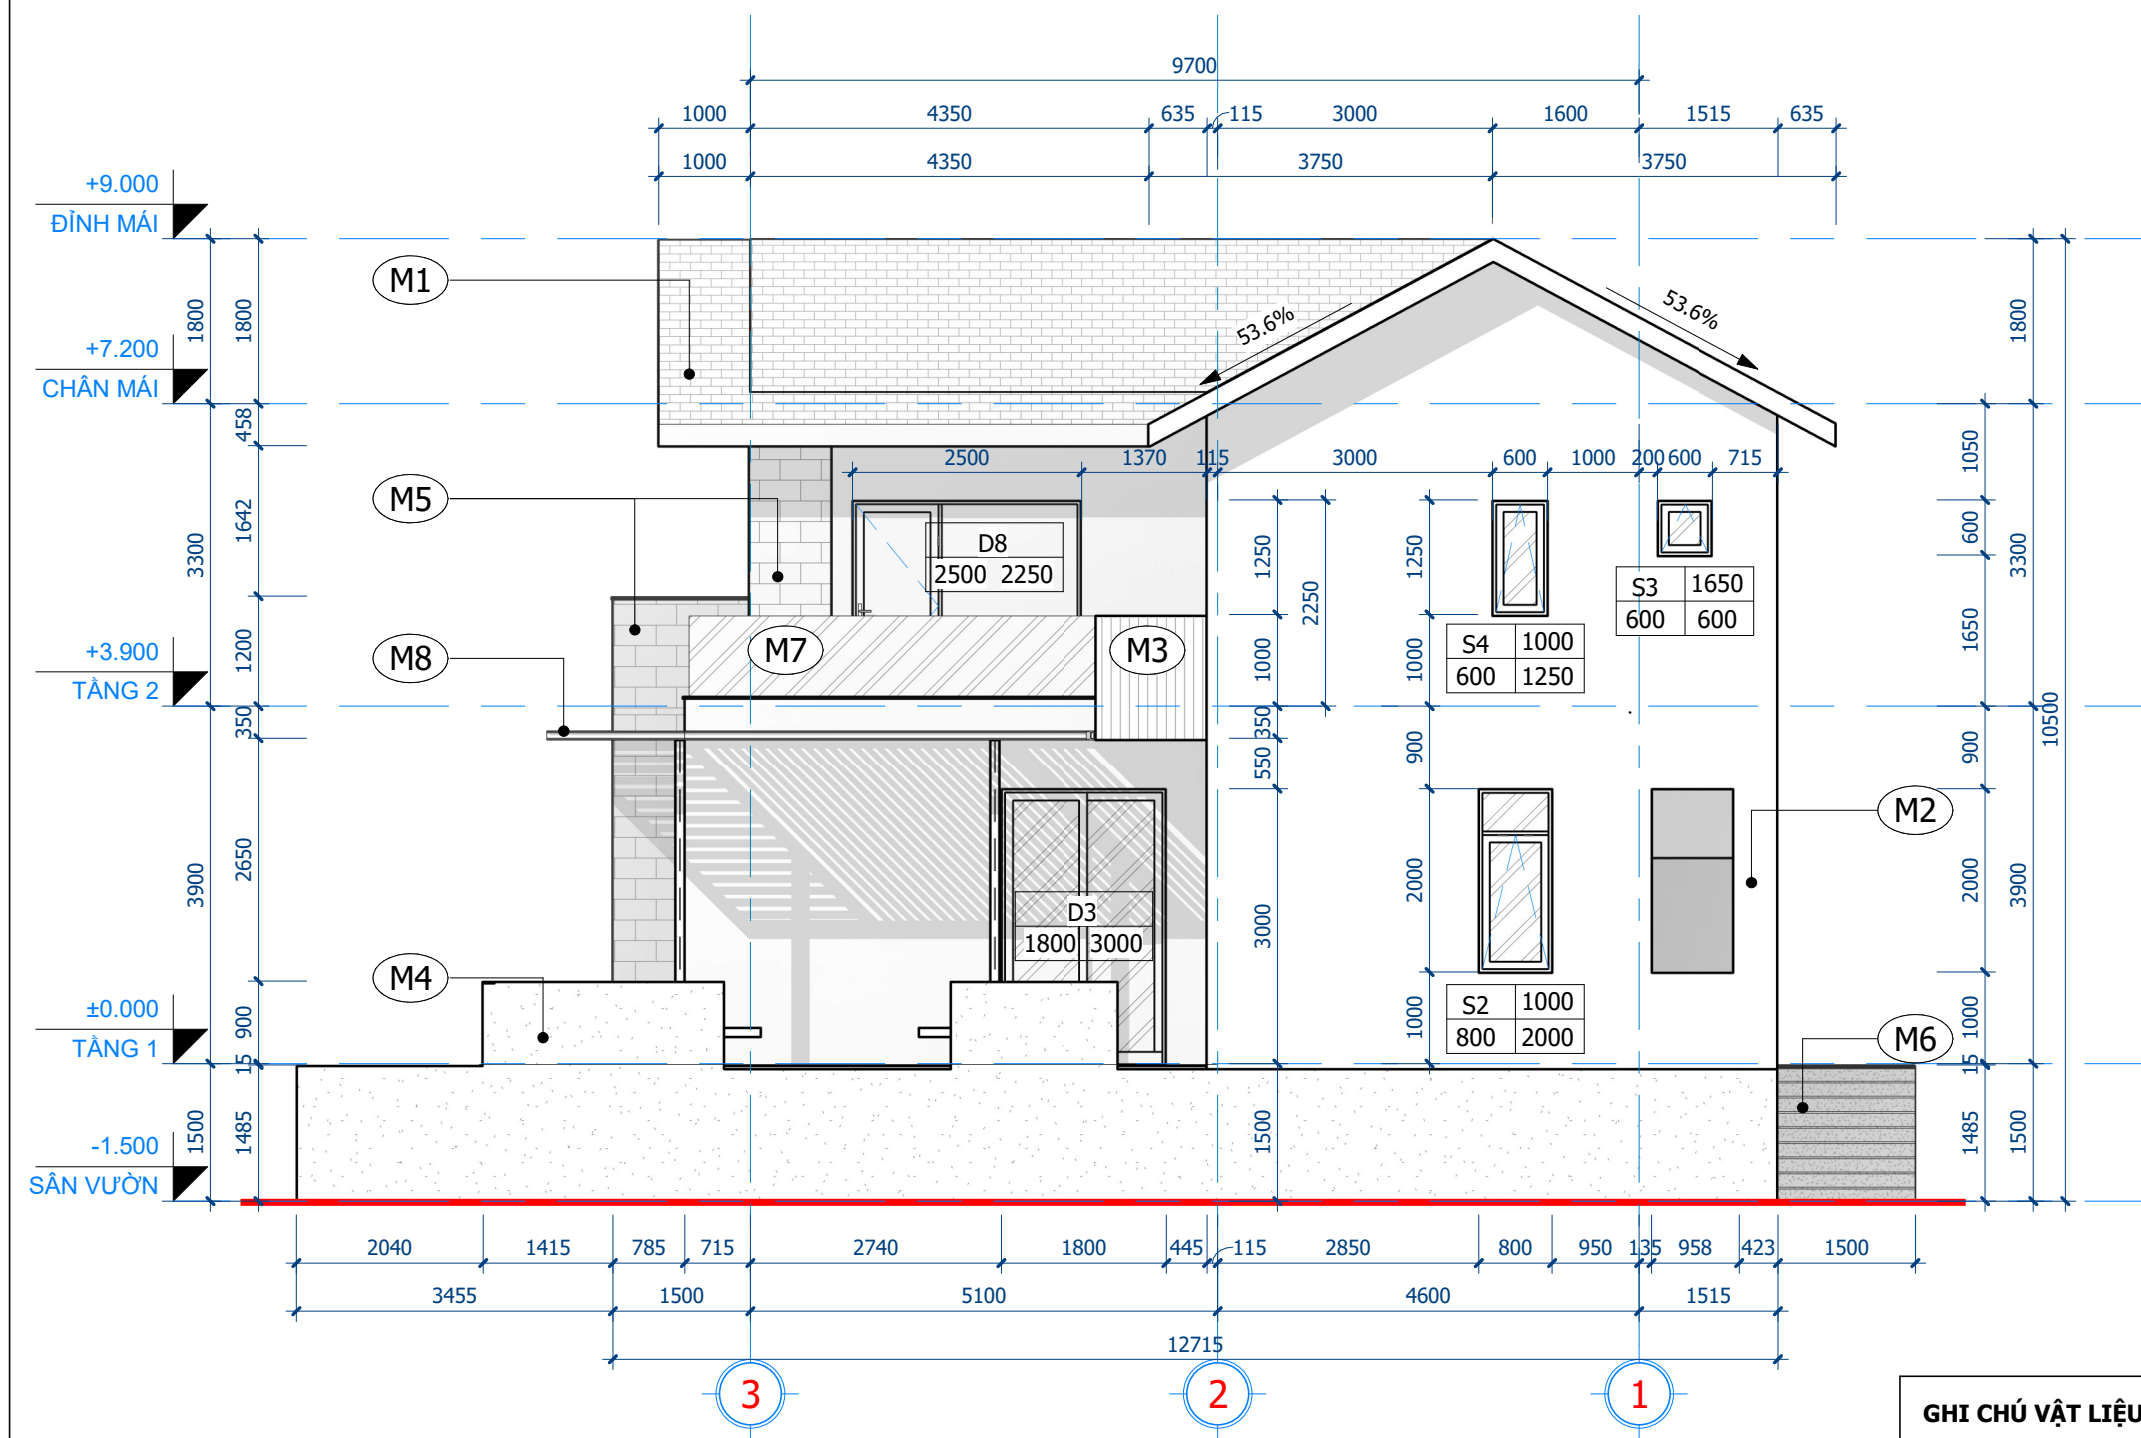


GHI CHÚ VẬT LIỆU-MẶT ĐỨNG	
MÃ	MÔ TẢ CHI TIẾT
M1	NGÓI LỢP (MẪU CHỌN THỰC TẾ)
M2	TƯỜNG SƠN NƯỚC MÀU KEM
M3	ÔP CONWOOD MÀU XÁM NHẠT
M4	TƯỜNG SƠN GIẢ BÊ TÔNG
M5	ÔP ĐÁ CHÉ (THEO MẪU)
M6	ĐÁ GRANITE ĐEN
M7	KÍNH CƯỜNG LỰC
M8	SƠN TĨNH ĐIỆN MÀU ĐEN

1 MẶT ĐỨNG TRỤC 3-1
1 : 75


KIẾN TRÚC
A110
12/14/21

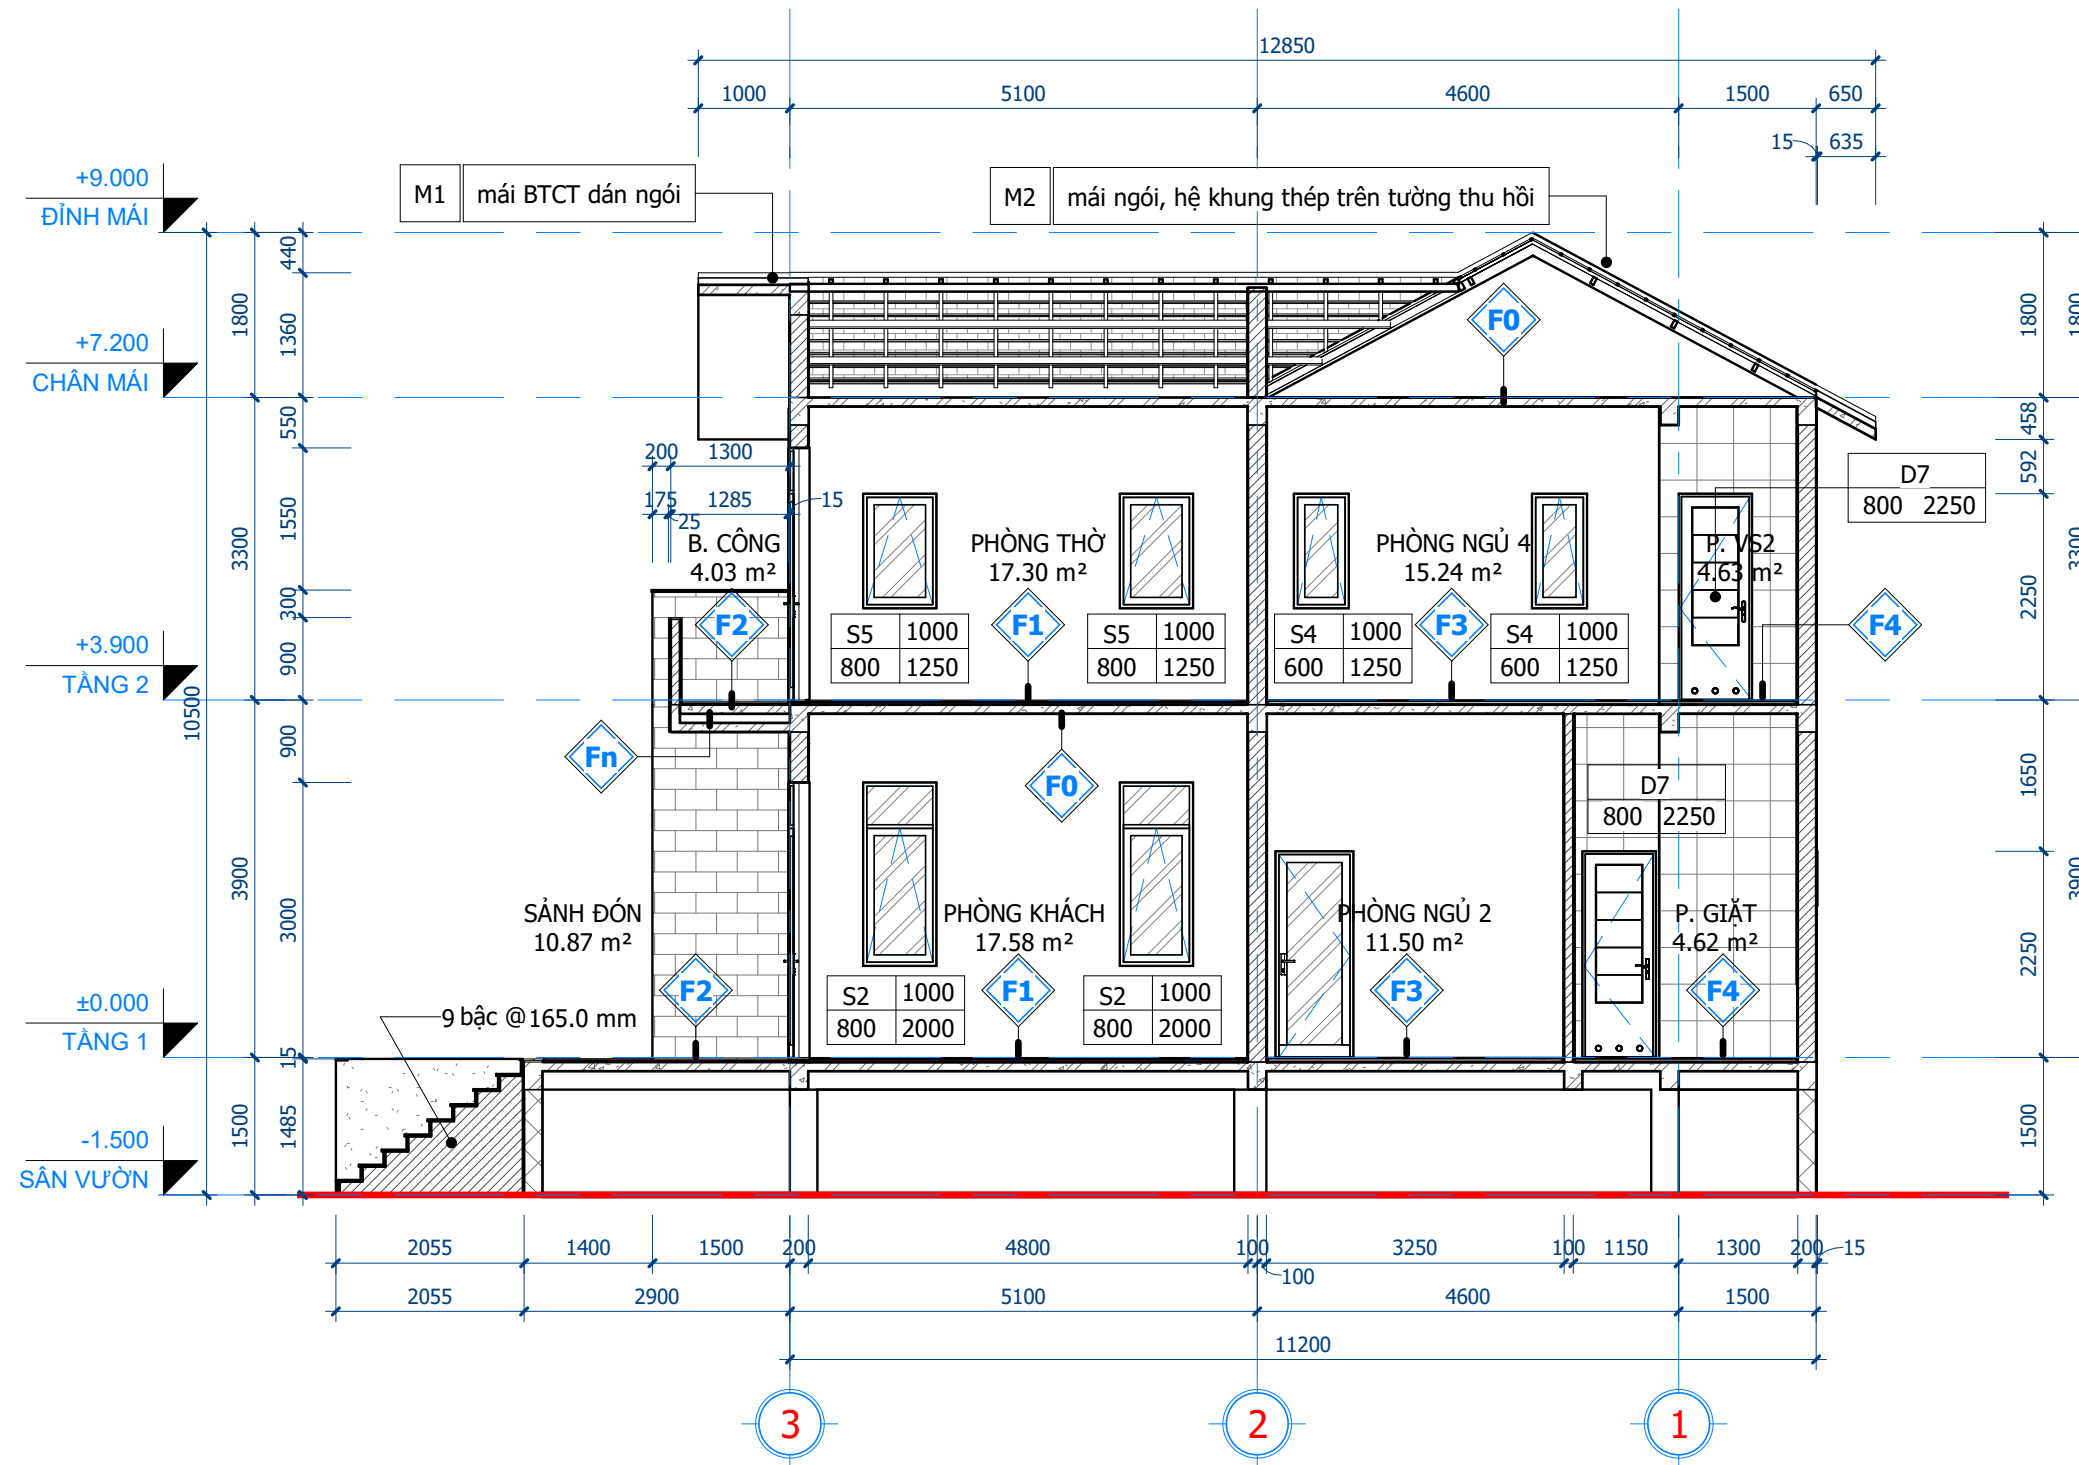


A MẶT CẮT A-A
1 : 75

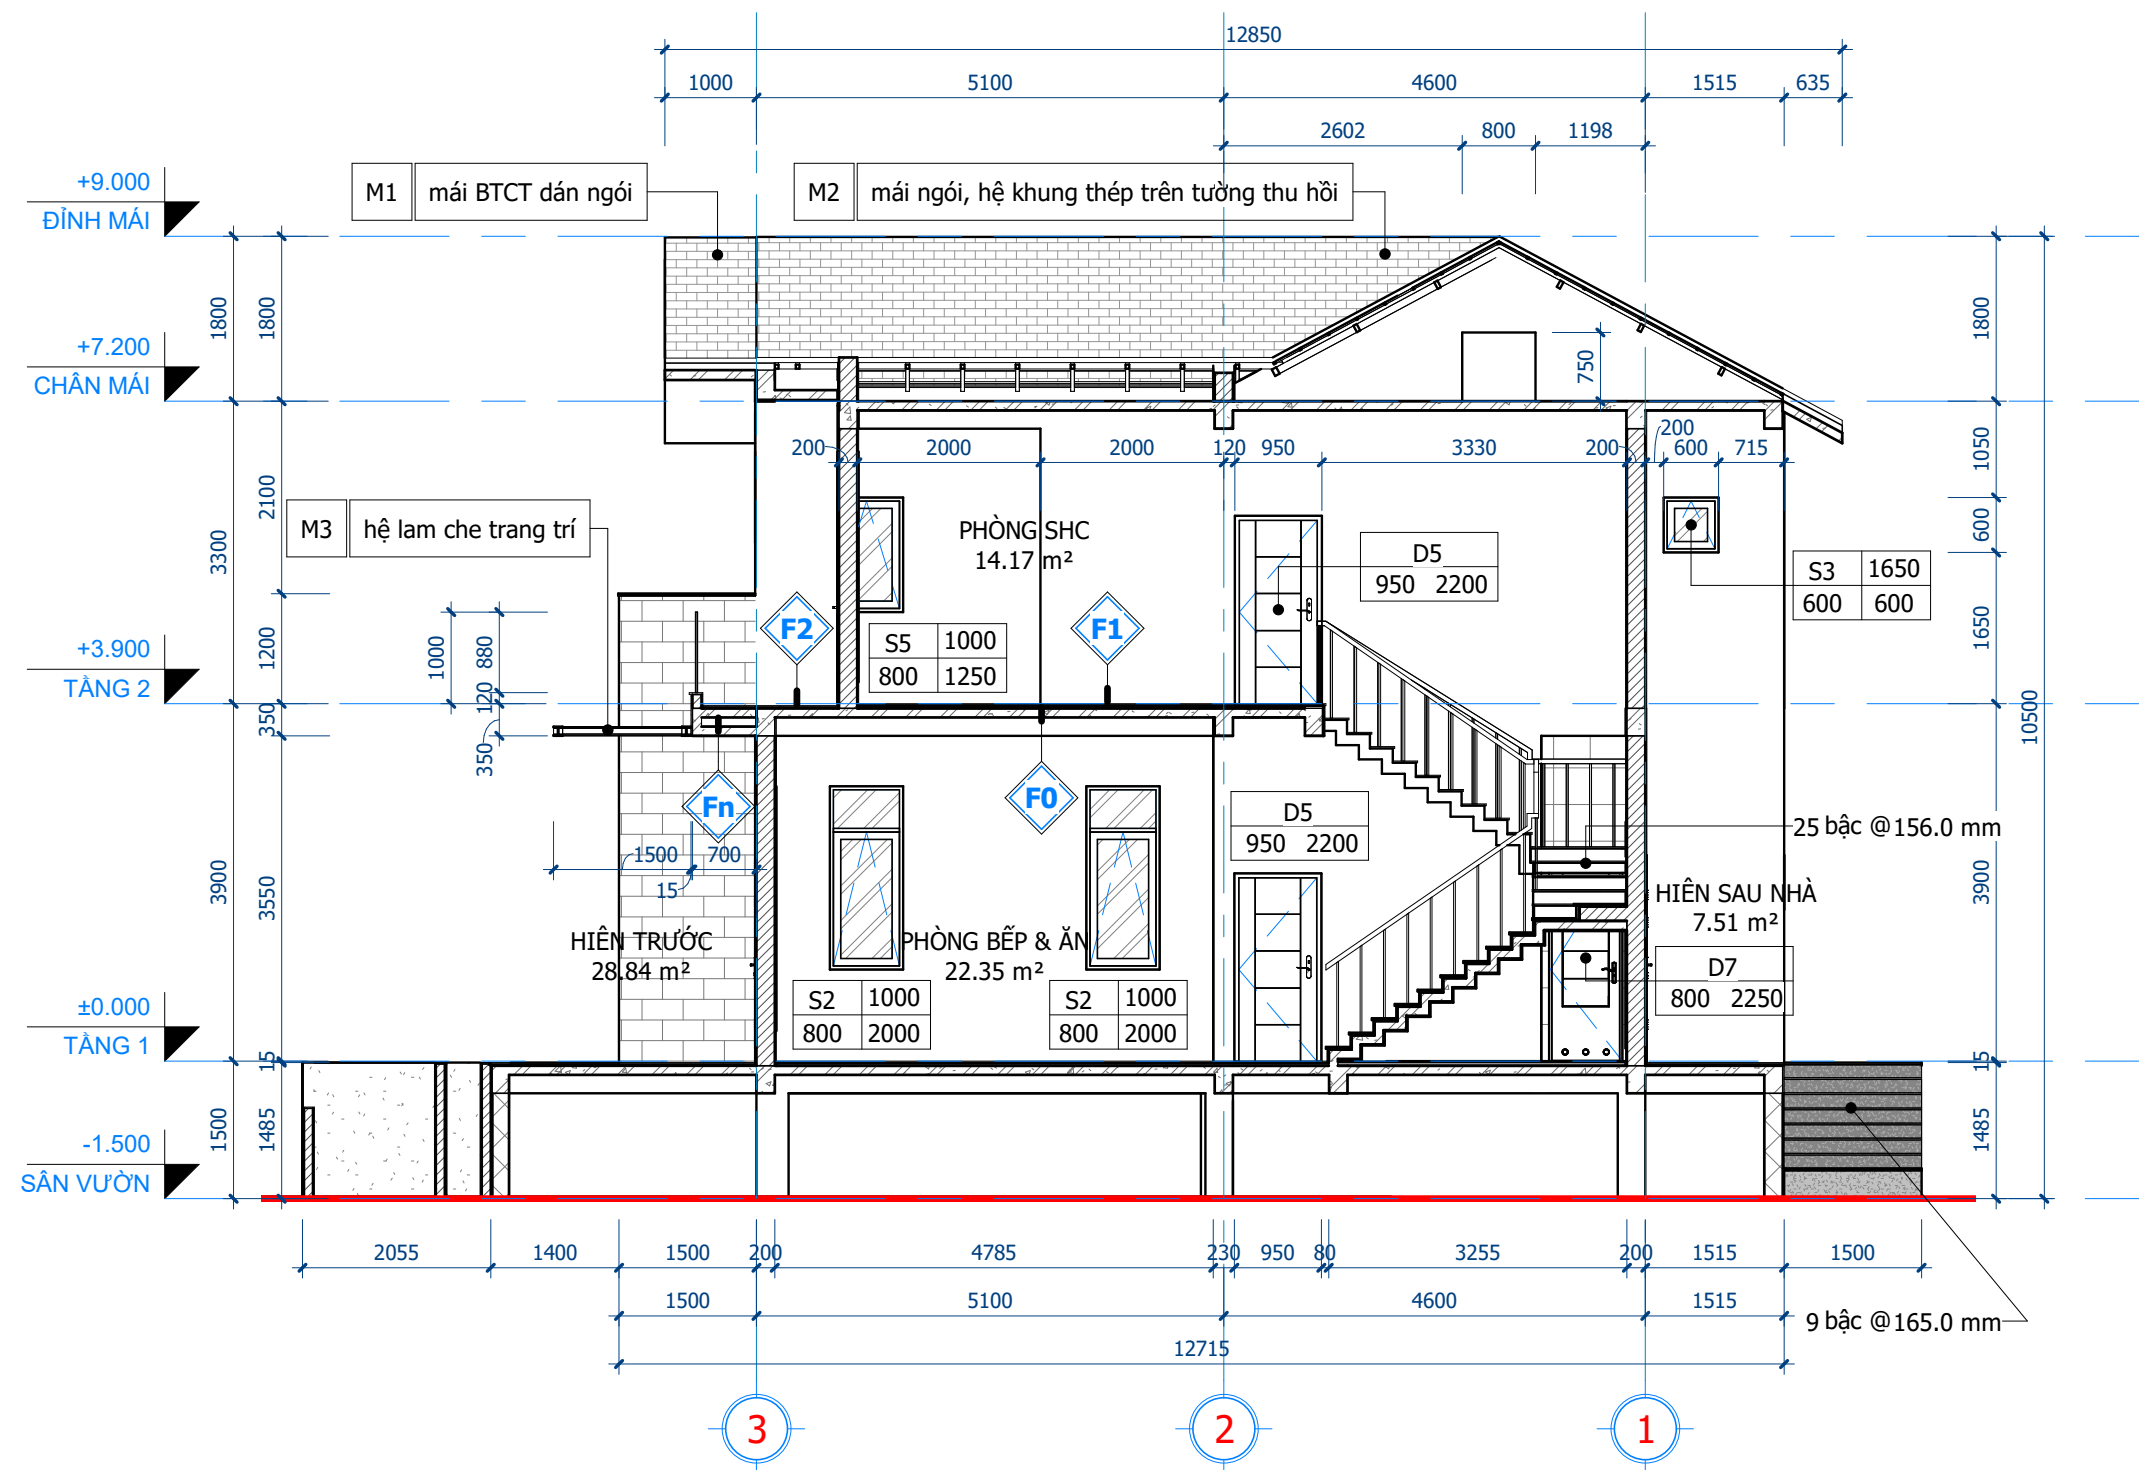

B MẶT CẮT B-B
1 : 75

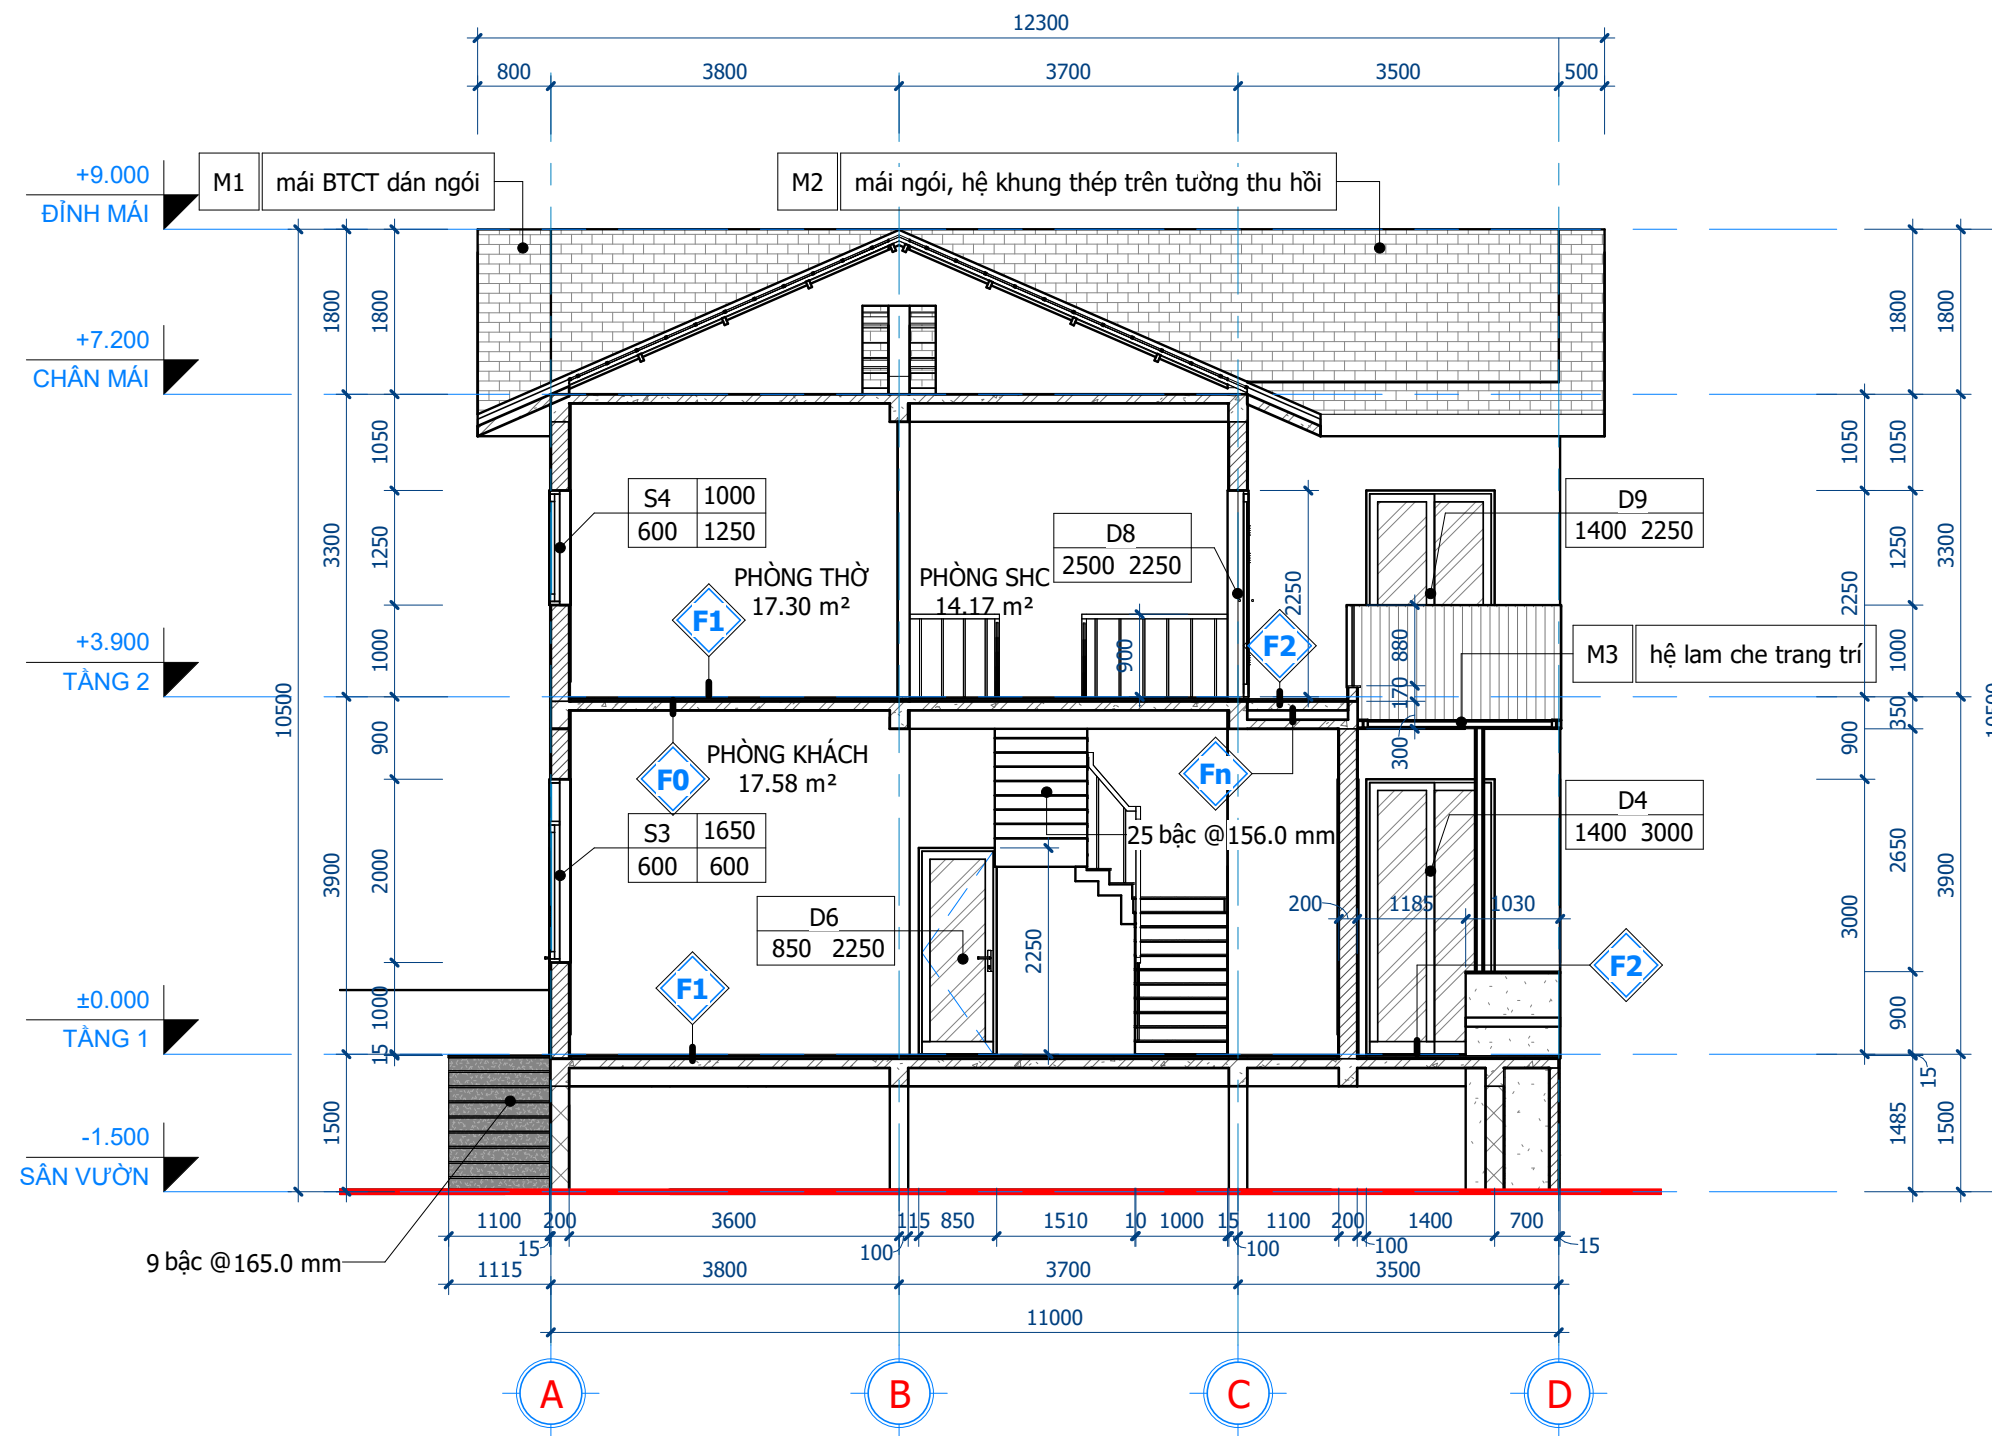

C MẶT CẮT C-C
1 : 75

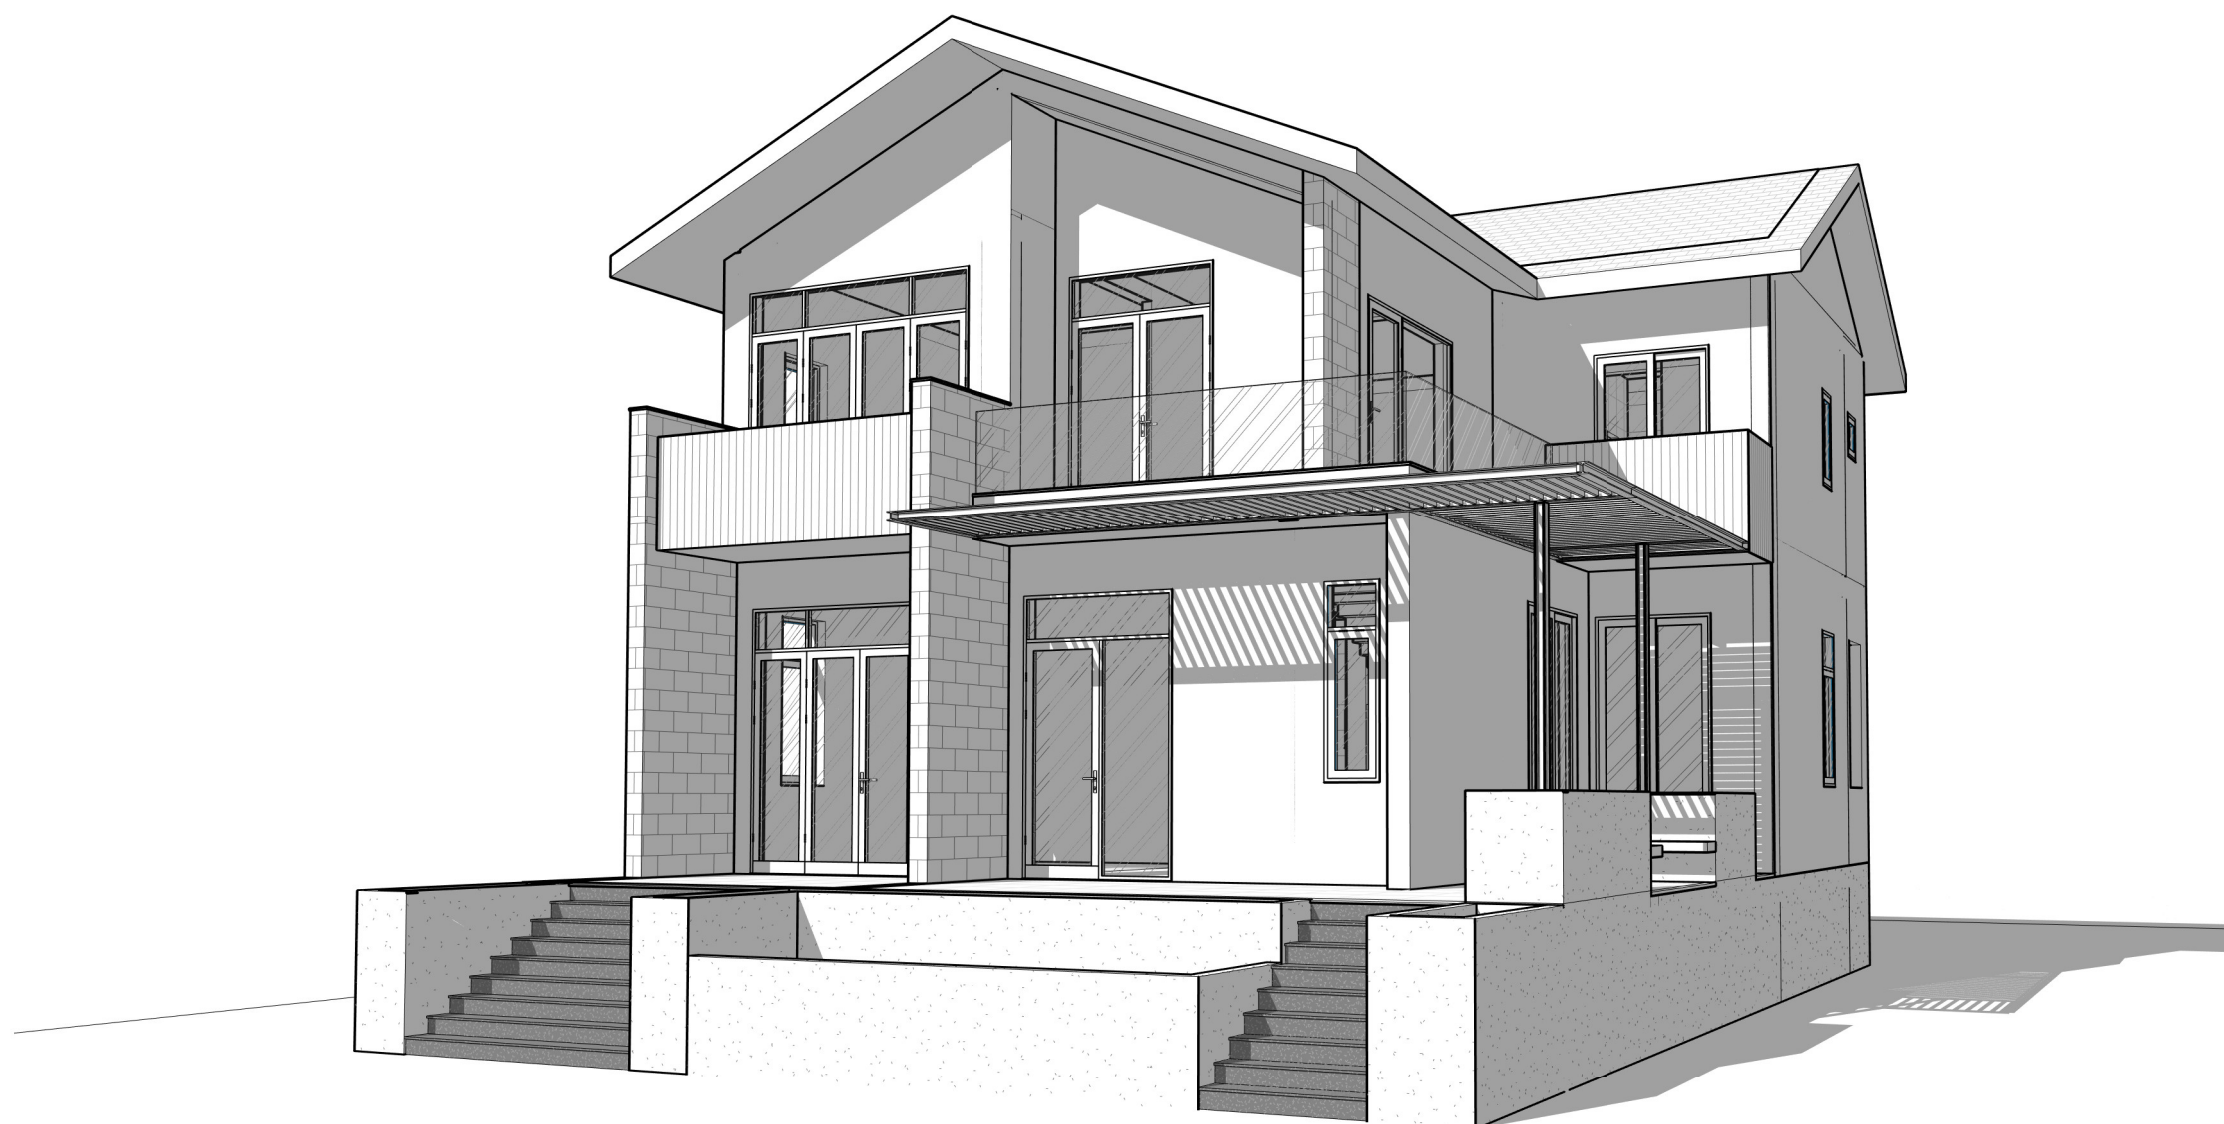


① PHỐI CẢNH CHUNG 1

KIẾN TRÚC
A114
12/14/21




1 PHỐI CẢNH CHUNG 2

KIẾN TRÚC
A115
12/14/21

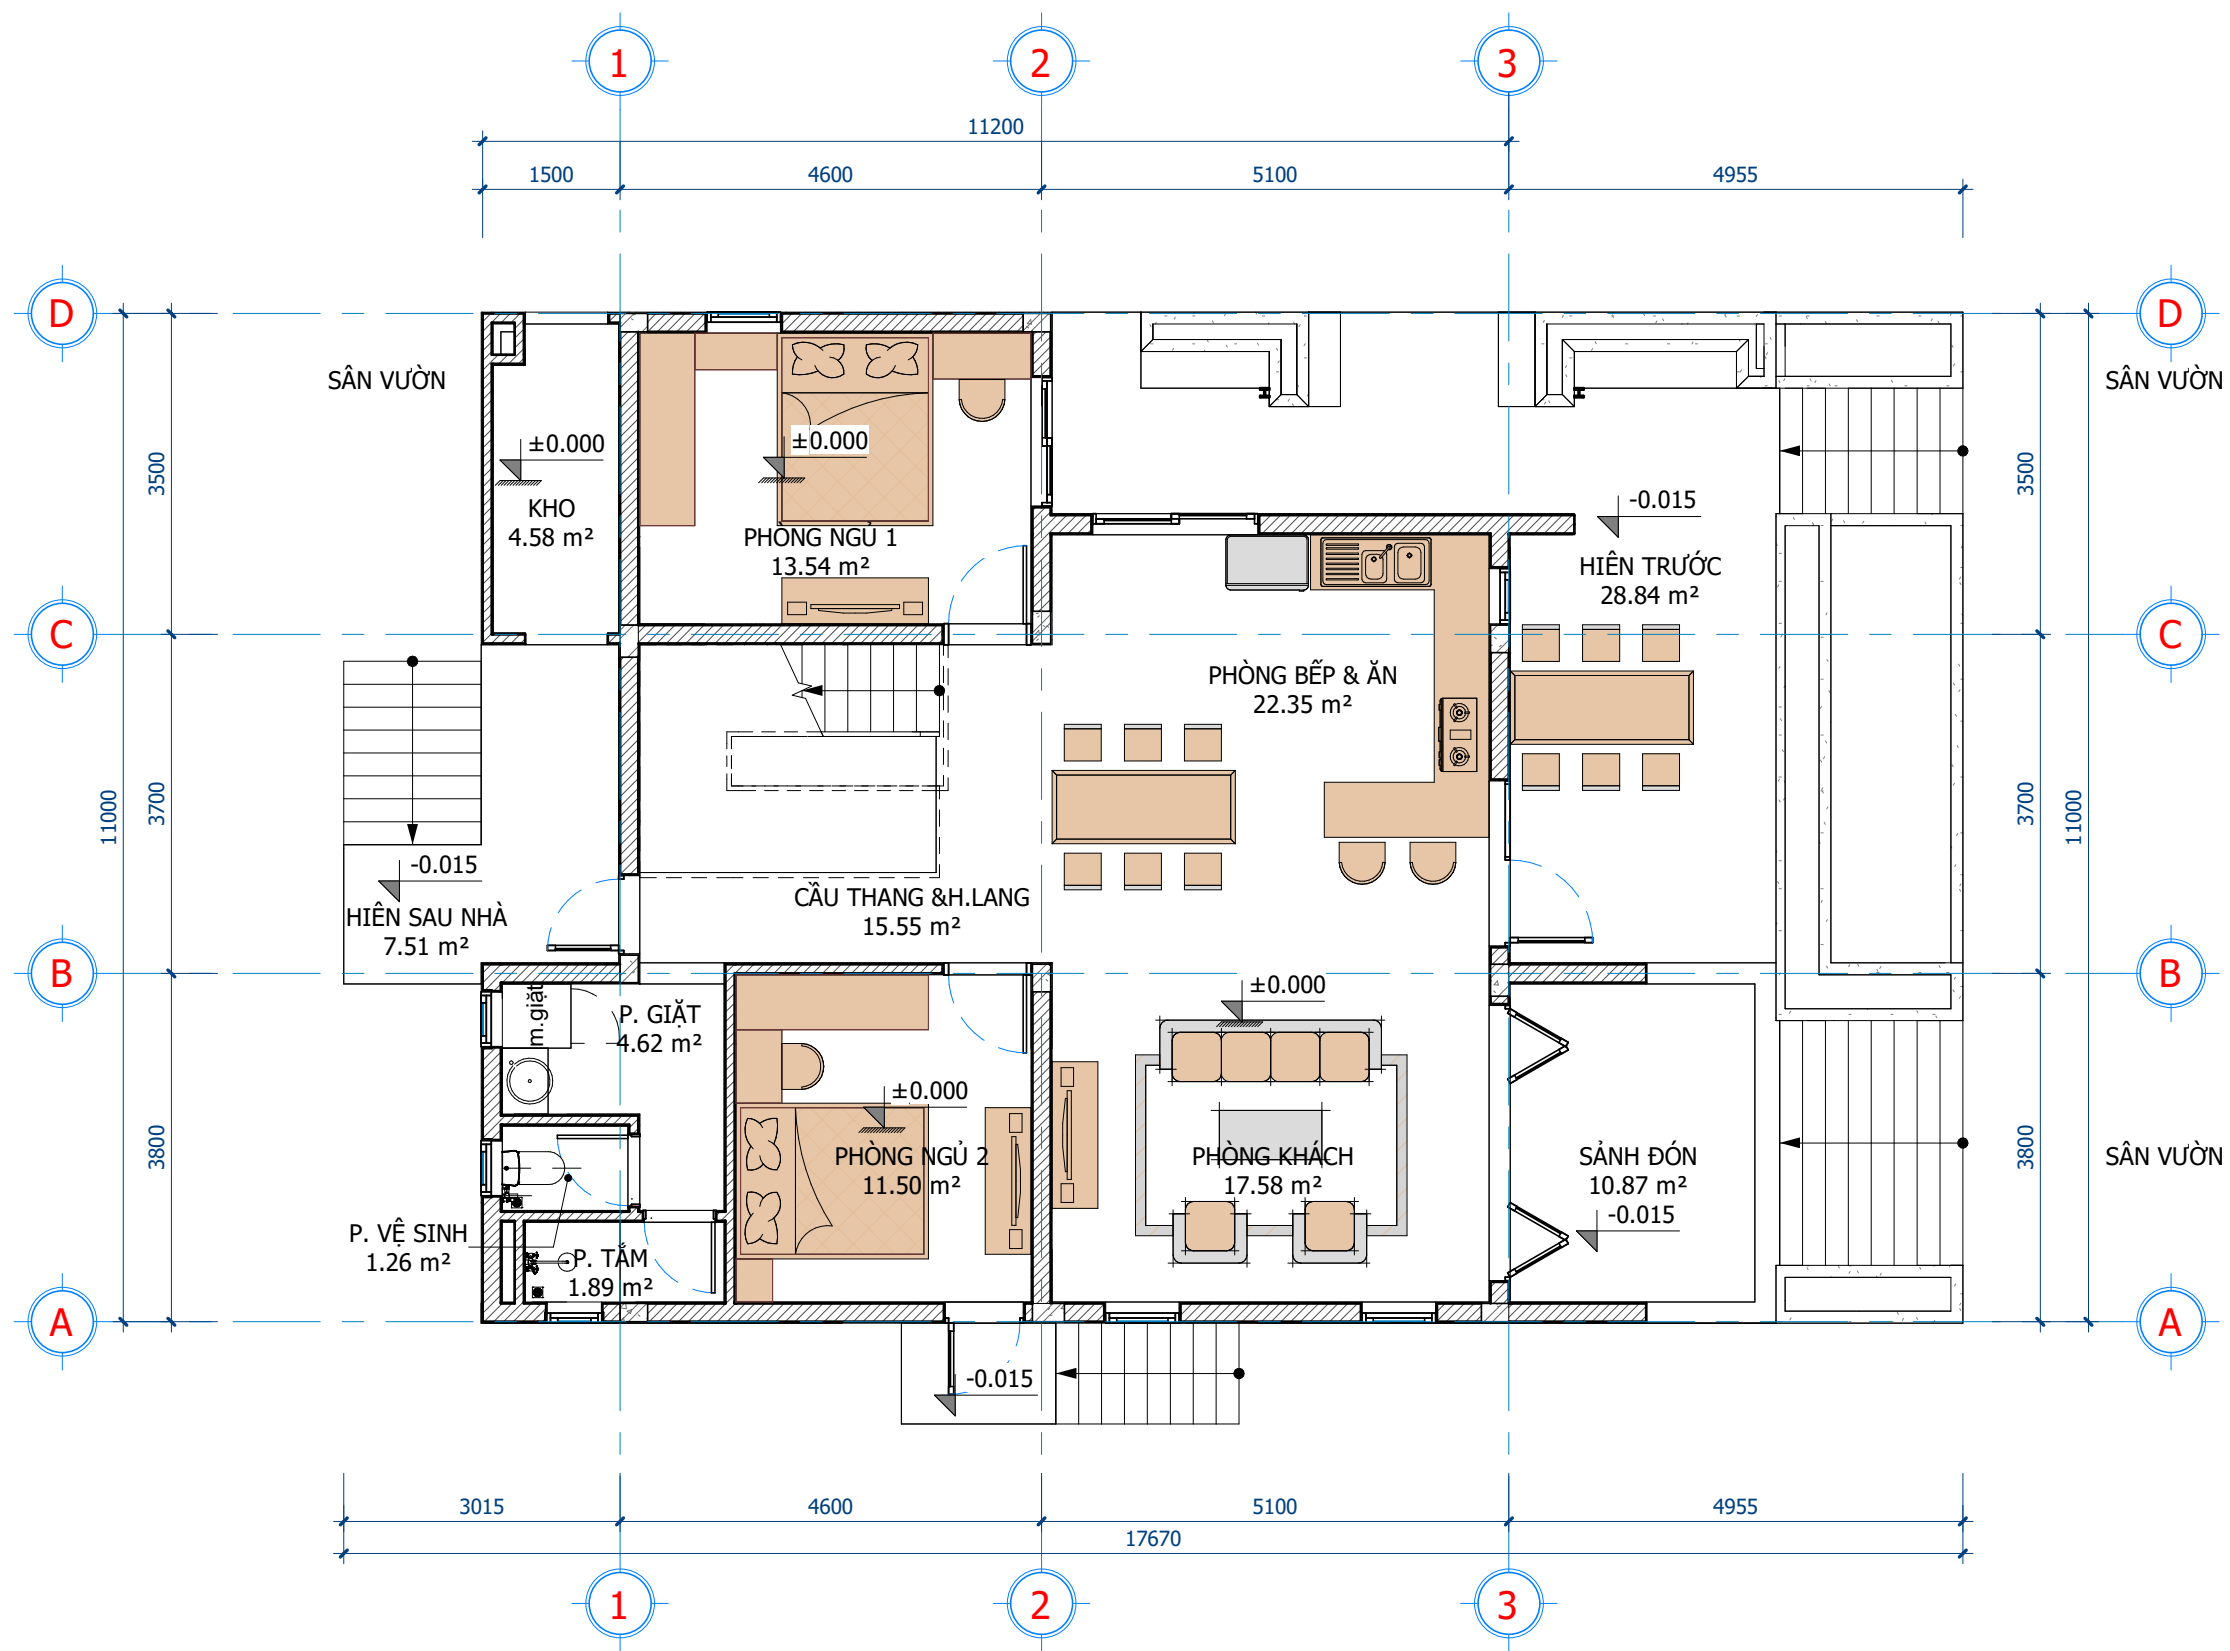

1 MB BỐ TRÍ VẬT DỤNG TẦNG 1
1 : 75

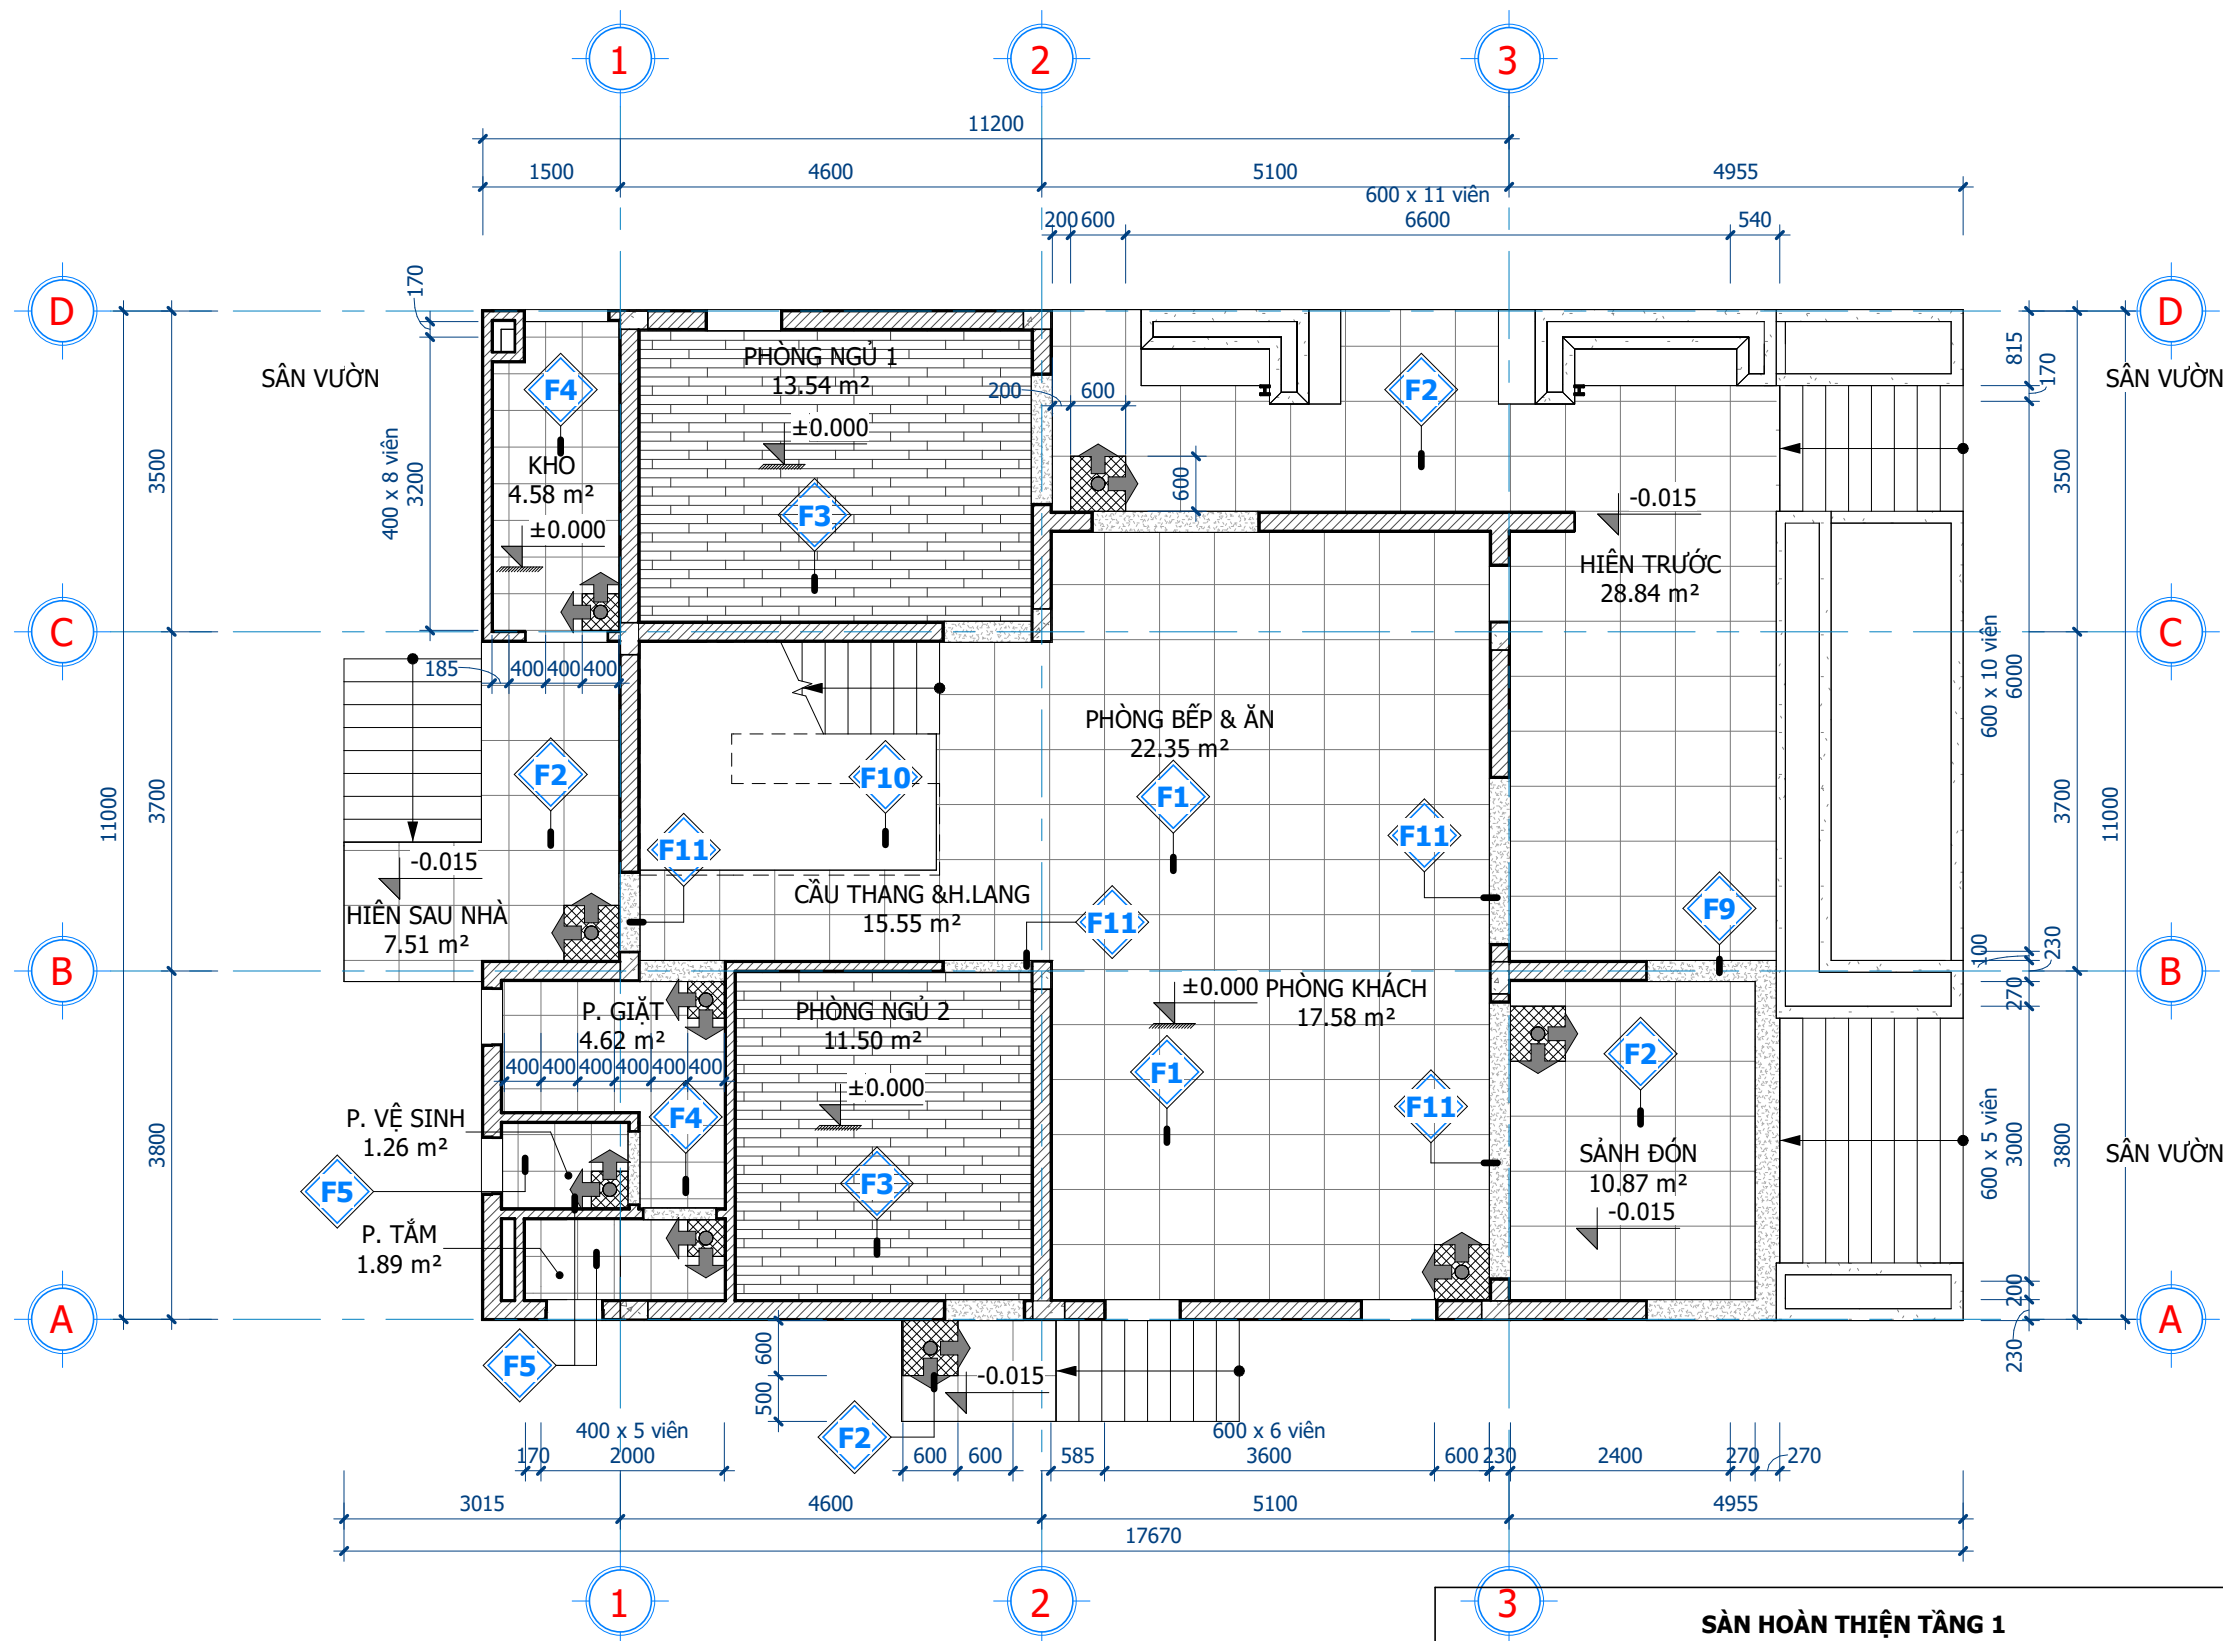

1 MB SÀN HOÀN THIỆN TẦNG 1
1 : 75


mũi tên chỉ hướng lát gạch
vị trí viên gạch chuẩn
KÝ HIỆU VIÊN GẠCH ĐỊNH VỊ CHUẨN

SÀN HOÀN THIỆN TẦNG 1		
KÝ HIỆU	DIỄN GIẢI	DIỆN TÍCH
F1	SÀN HOÀN THIỆN ĐÁ GRANITE 600X600, MÀU KEM SÁNG	47.51 m ²
F2	SÀN HOÀN THIỆN ĐÁ GRANITE 600X600, CHỐNG TRƯỢT	47.33 m ²
F3	SÀN GỖ CÔNG NGHIỆP, MÀU XÁM NHẠT	25.03 m ²
F4	SÀN HOÀN THIỆN GẠCH CERAMIC 400X400, CÓ LỚP CHỐNG THẤM	8.98 m ²
F5	SÀN HOÀN THIỆN GẠCH CERAMIC 400X400, CHỐNG TRƯỢT	3.15 m ²
F9	SÀN HOÀN THIỆN ĐÁ GRANITE MÀU XÁM ĐẬM, LÁT TRANG TRÍ	1.45 m ²
F10	NỀN VƯỜN TIỂU CẢNH TRONG NHÀ	7.94 m ²
F11	SÀN HOÀN THIỆN ĐÁ GRANITE MÀU XÁM ĐẬM, LÁT NGẠNH CỬA	2.99 m ²

KIẾN TRÚC
A202
12/14/21



1 MB BỐ TRÍ VẬT DỤNG TẦNG 2
1 : 75

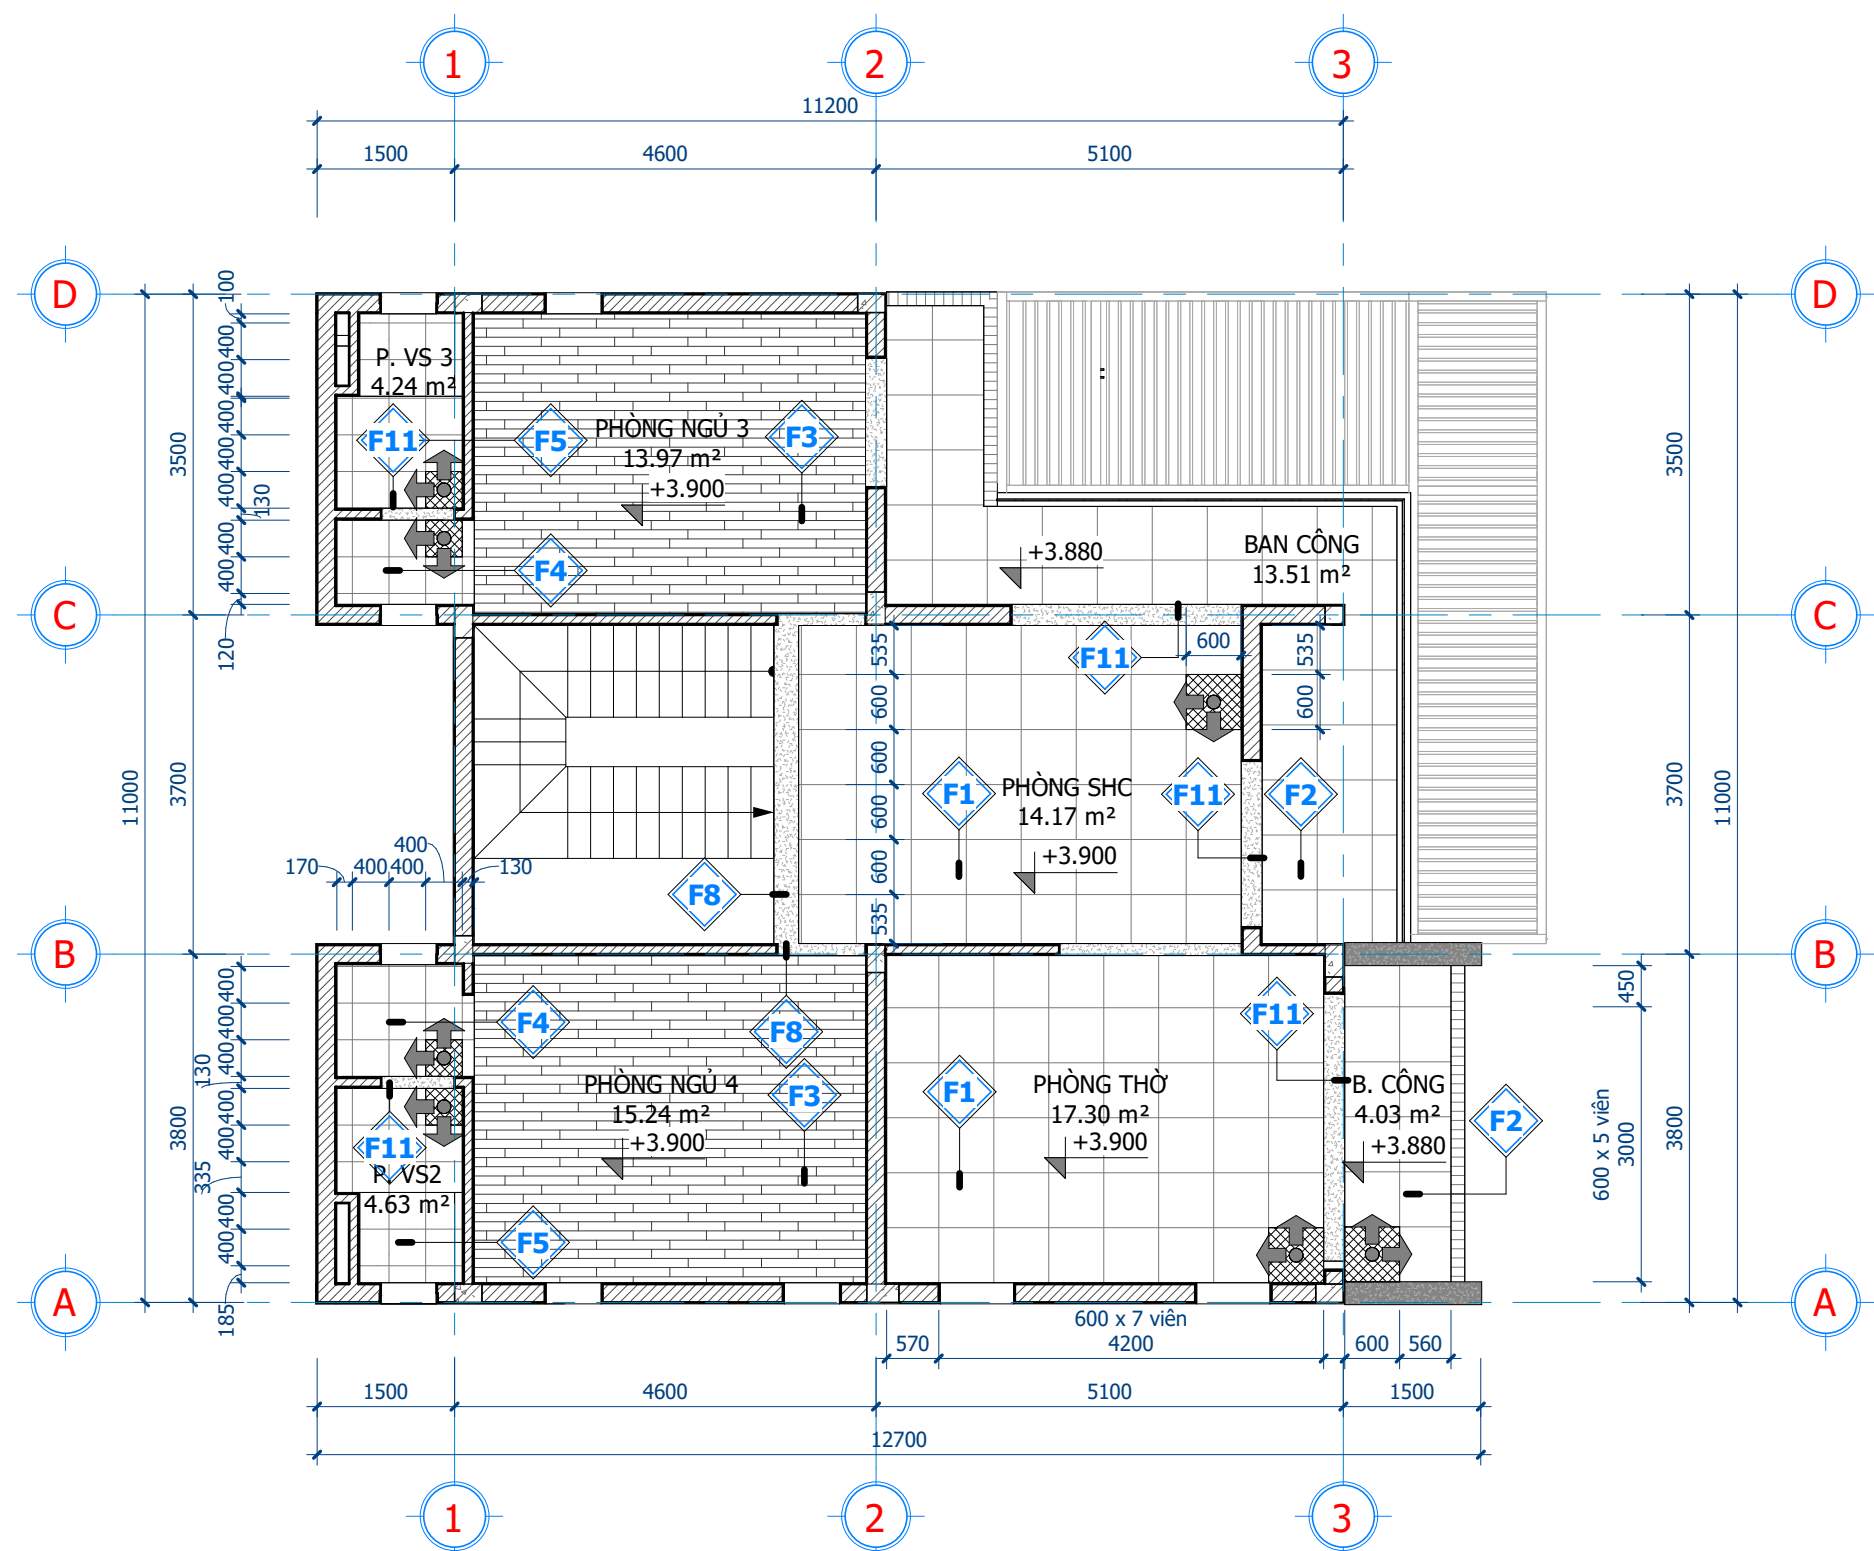


mũi tên chỉ hướng lát gạch
vị trí viên gạch chuẩn
KÝ HIỆU VIÊN GẠCH ĐỊNH VỊ CHUẨN


1 MB HOÀN THIỆN SÀN TẦNG 2
1 : 75

SÀN HOÀN THIỆN TẦNG 2		
KÝ HIỆU	DIỄN GIẢI	DIỆN TÍCH
F1	SÀN HOÀN THIỆN ĐÁ GRANITE 600X600, MÀU KEM SÁNG	34.62 m ²
F2	SÀN HOÀN THIỆN ĐÁ GRANITE 600X600, CHỐNG TRƯỢT	17.54 m ²
F3	SÀN GỖ CÔNG NGHIỆP, MÀU XÁM NHẠT	29.21 m ²
F4	SÀN HOÀN THIỆN GẠCH CERAMIC 400X400, CÓ LỚP CHỐNG THẤM	3.17 m ²
F5	SÀN HOÀN THIỆN GẠCH CERAMIC 400X400, CHỐNG TRƯỢT	5.34 m ²
F8	SÀN HOÀN THIỆN ĐÁ GRANITE MÀU XÁM ĐẬM, LÁT NGANGH CỬA	0.94 m ²
F11	SÀN HOÀN THIỆN ĐÁ GRANITE MÀU XÁM ĐẬM, LÁT NGANGH CỬA	2.69 m ²


KIẾN TRÚC
A204
12/14/21

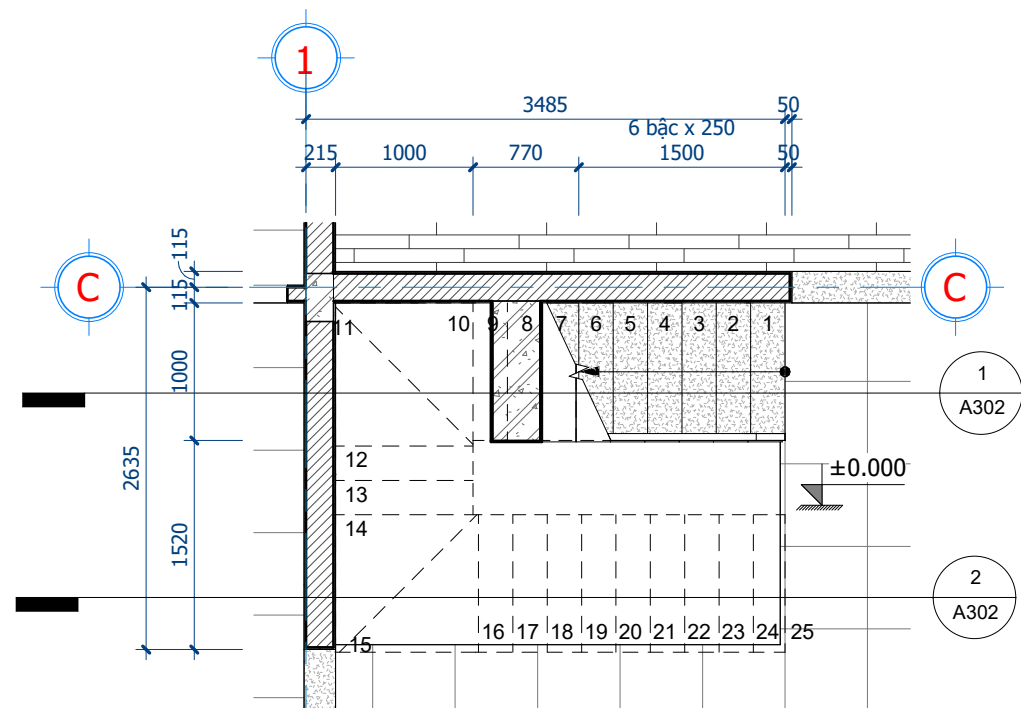


1 MB CẦU THANG TẦNG 1
1 : 50

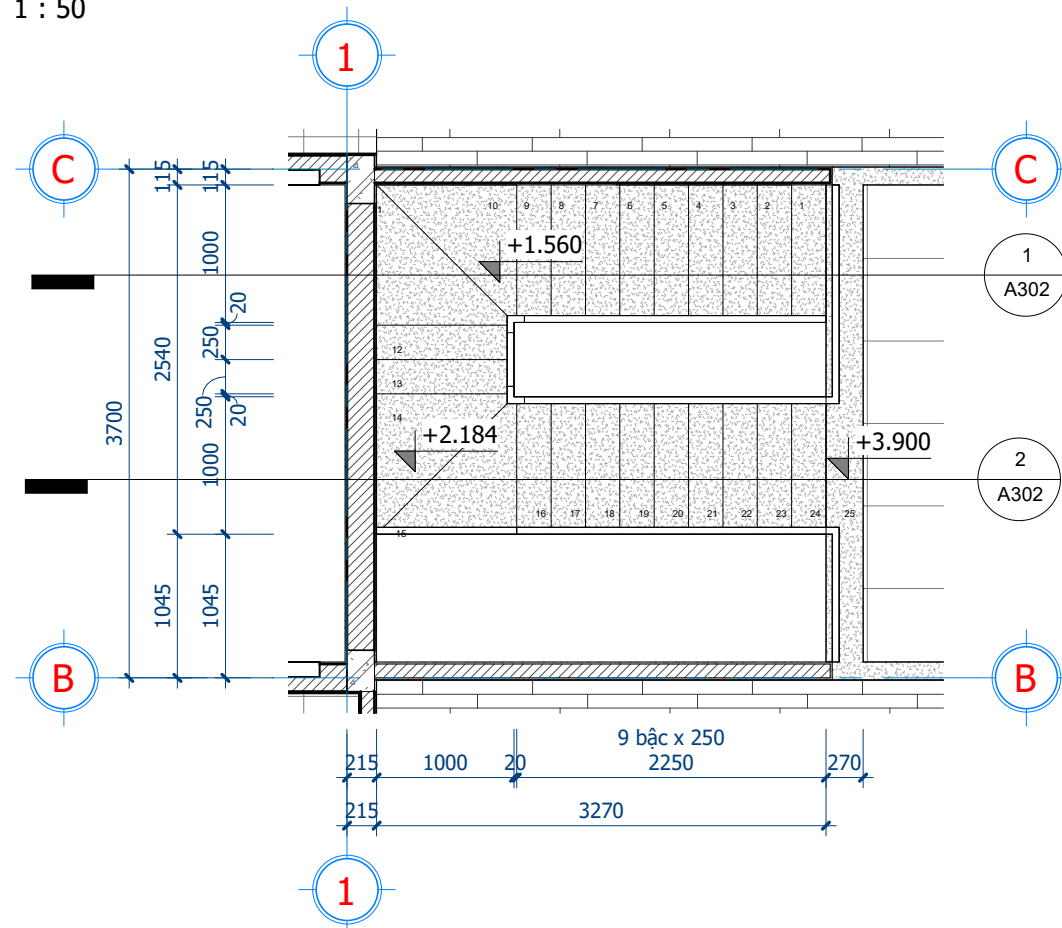


2 MB CẦU THANG TẦNG 2
1 : 50

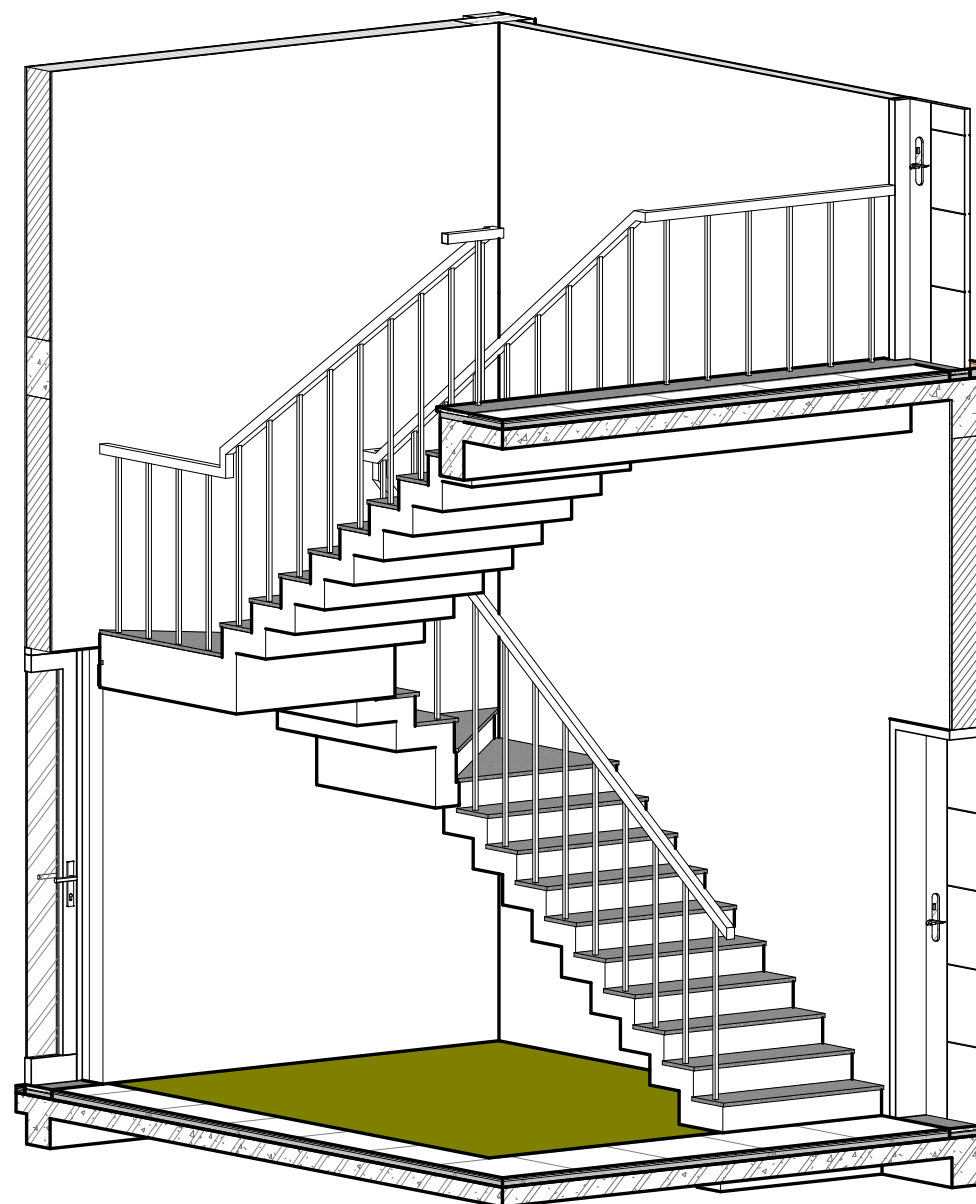


3 PHỐI CẢNH CẦU THANG

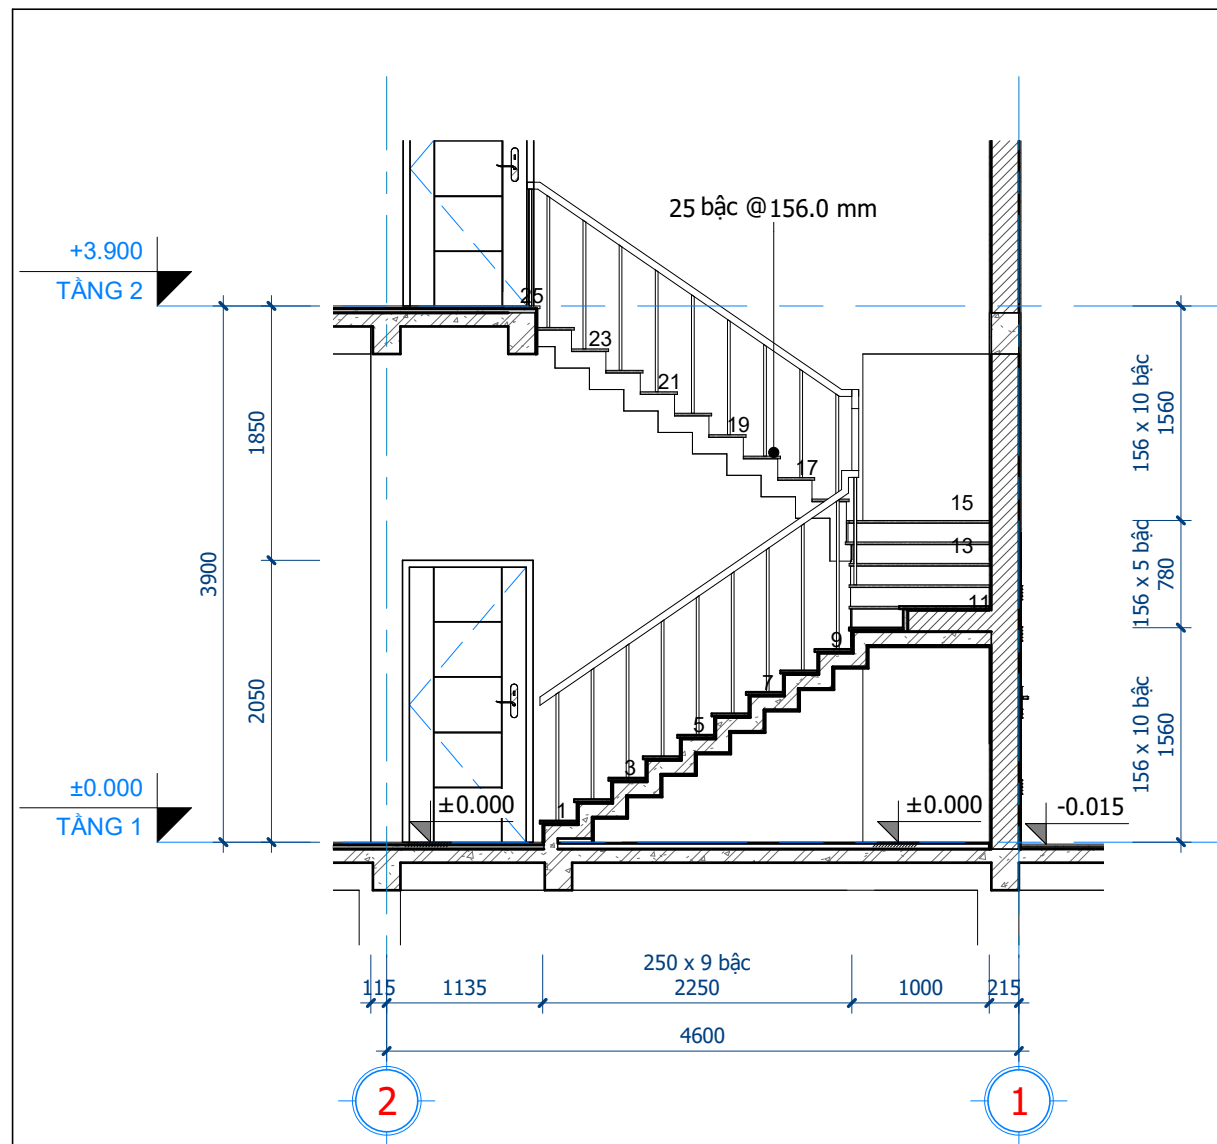


1 MẶT CẮT 1-1
1 : 50

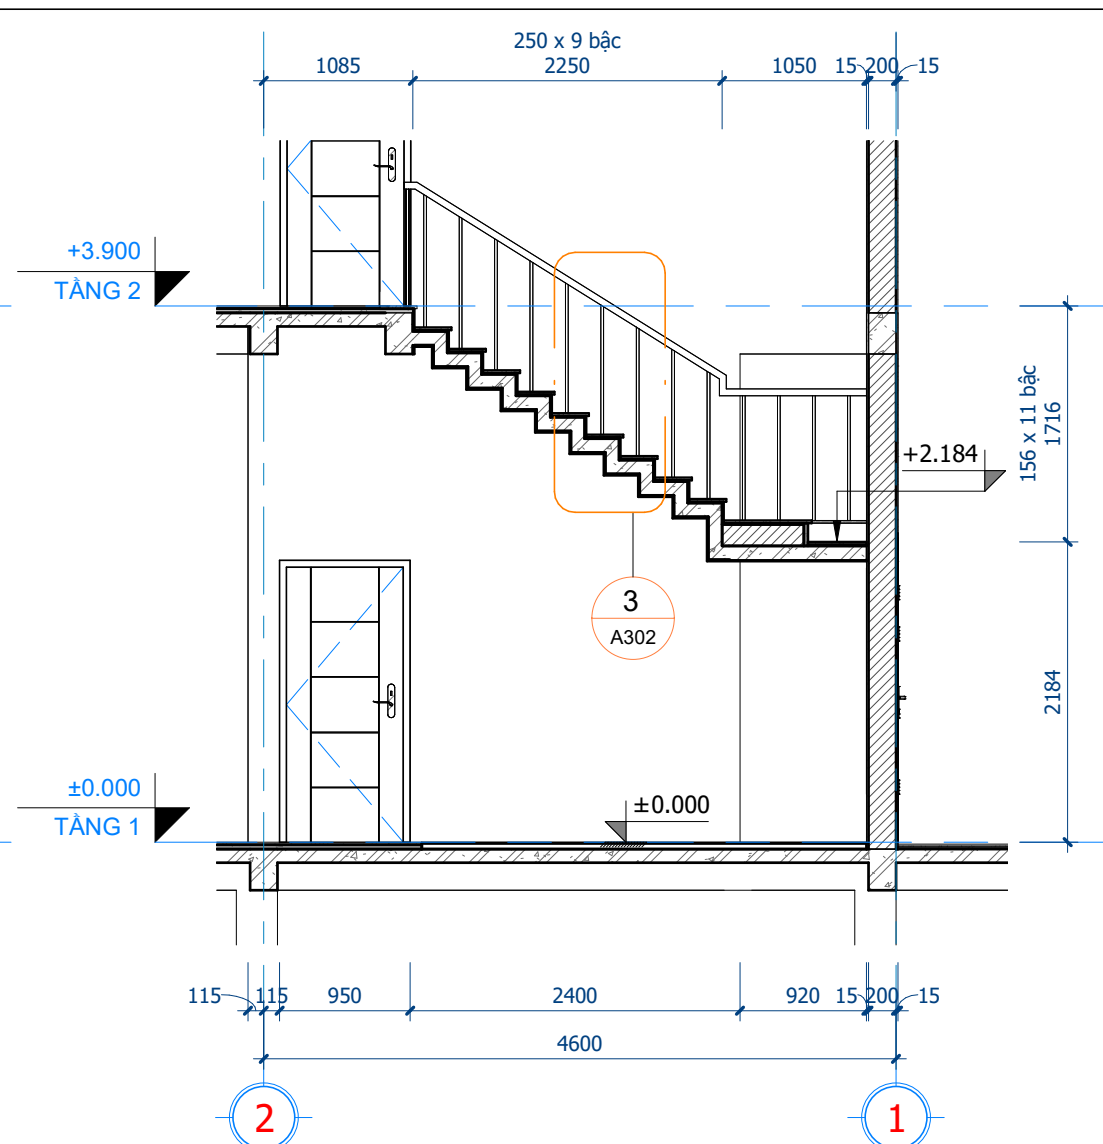


2 MẶT CẮT 2-2
1 : 50

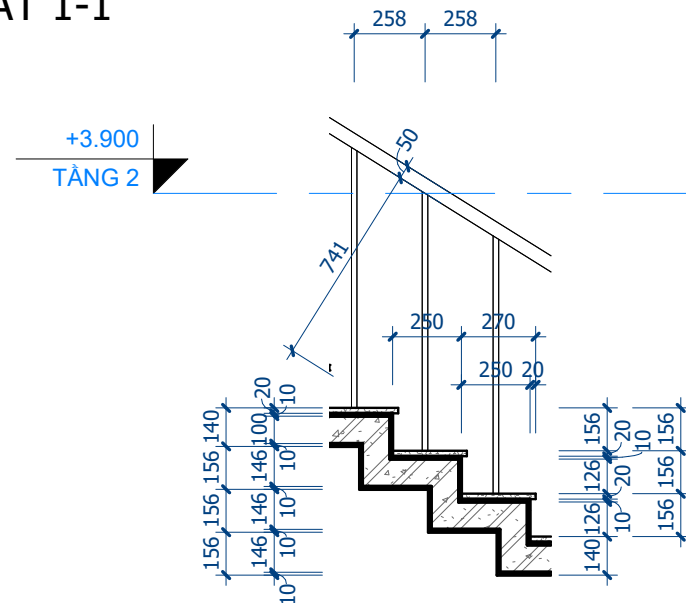


3 CT BẬC CẦU THANG
1 : 25

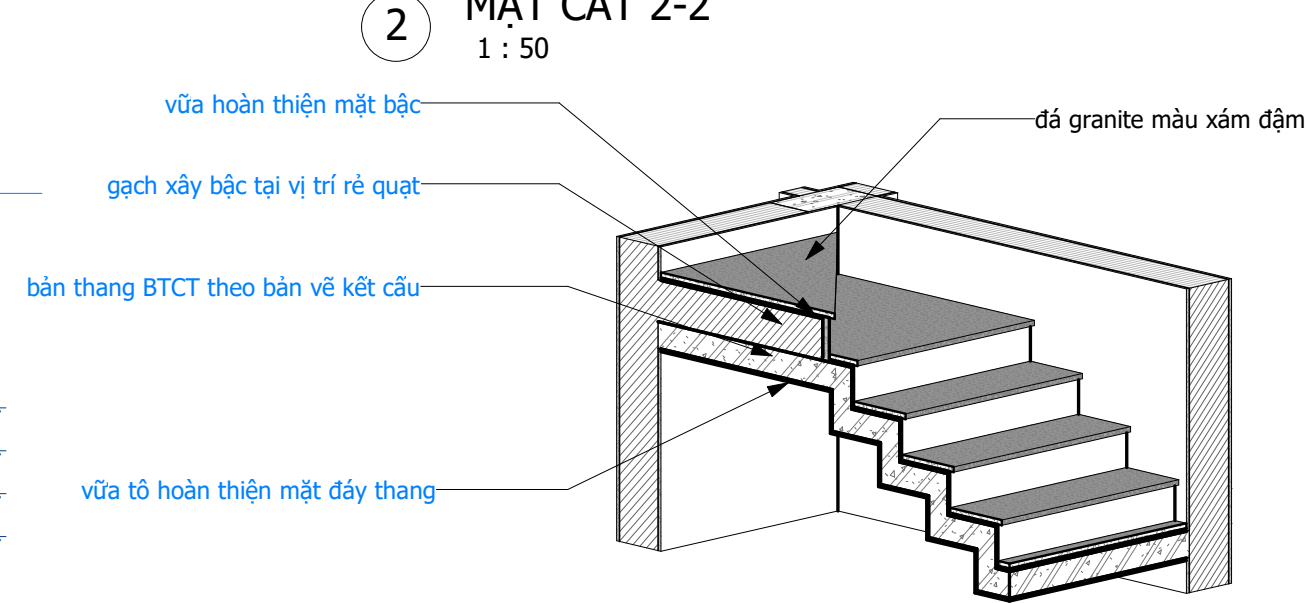


4 CHI TIẾT BẬC THANG

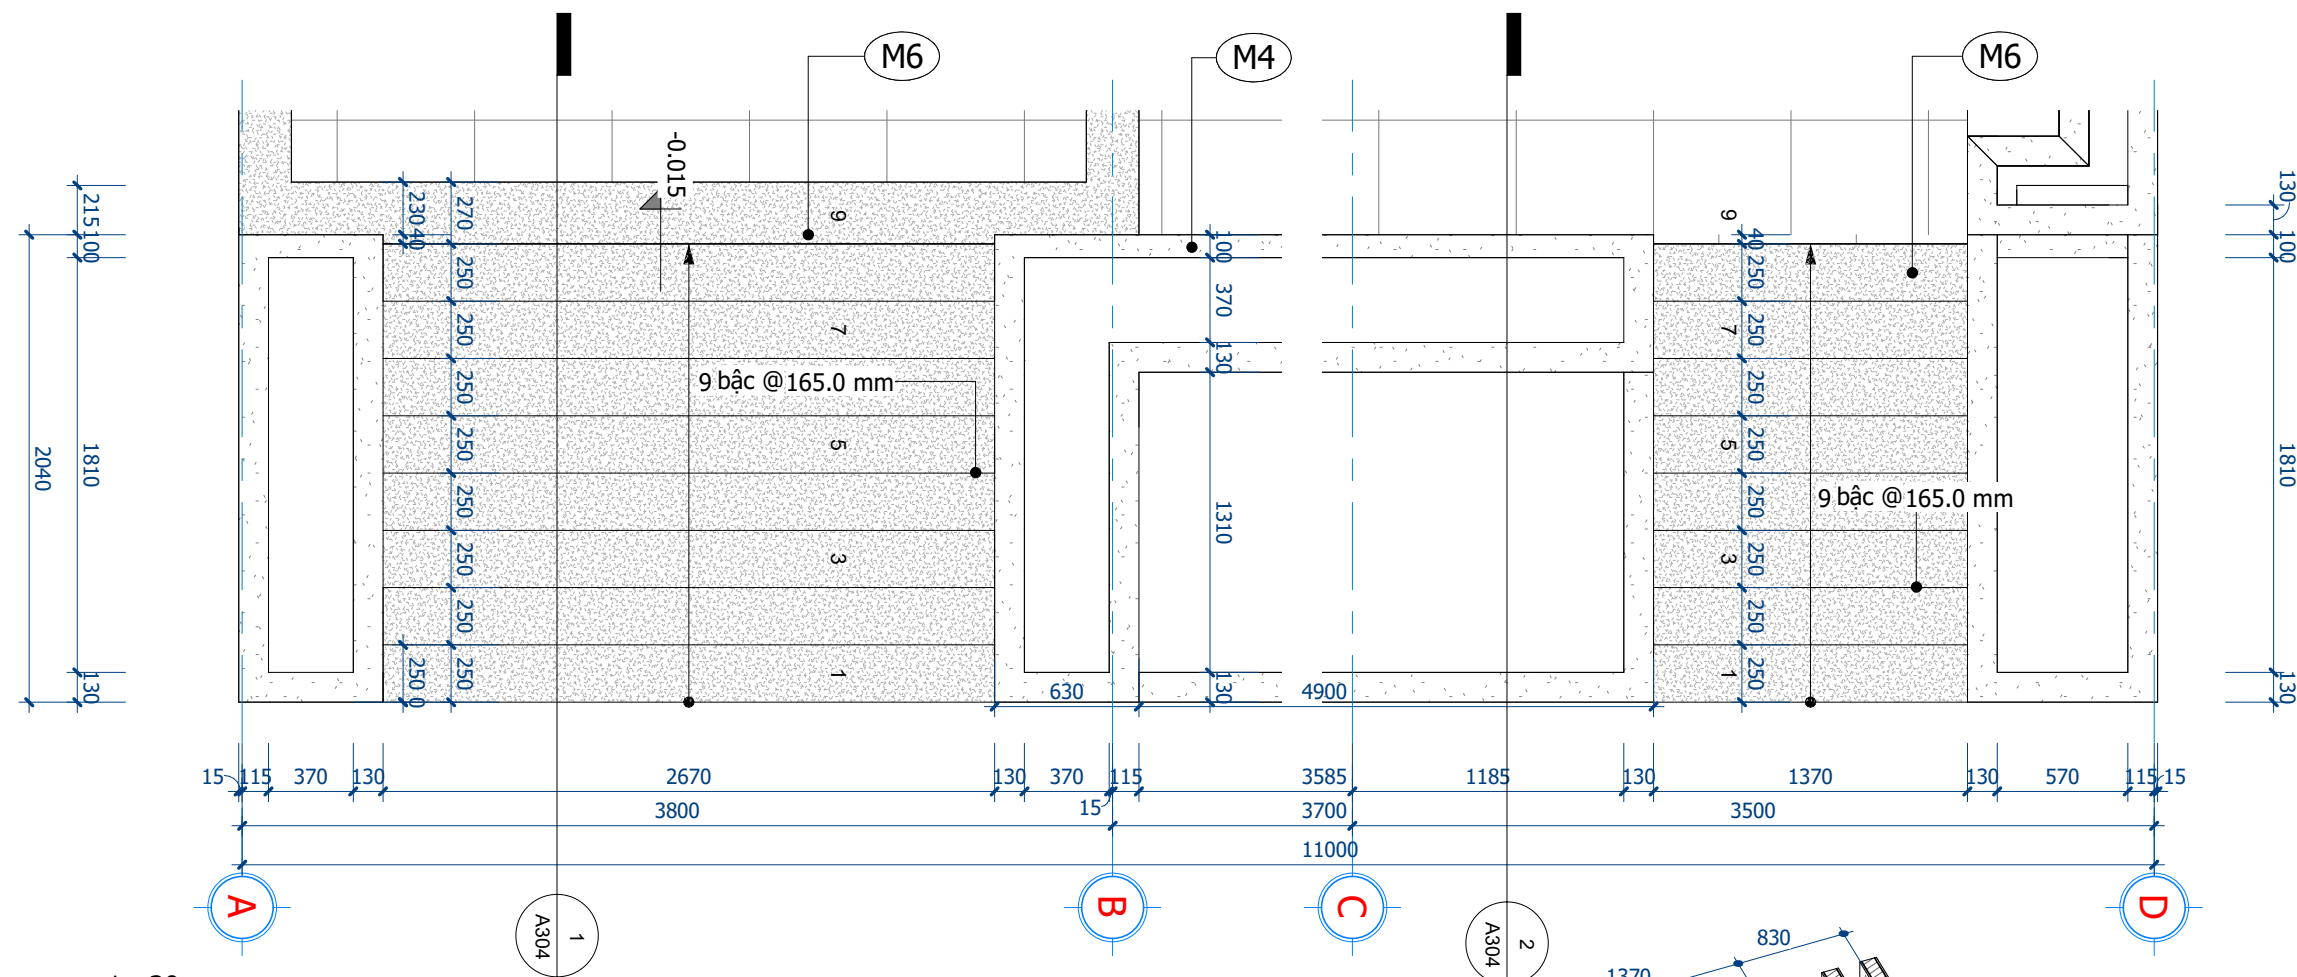


1 : 30
BẬC CẤP 01- MẶT BẰNG CHI TIẾT

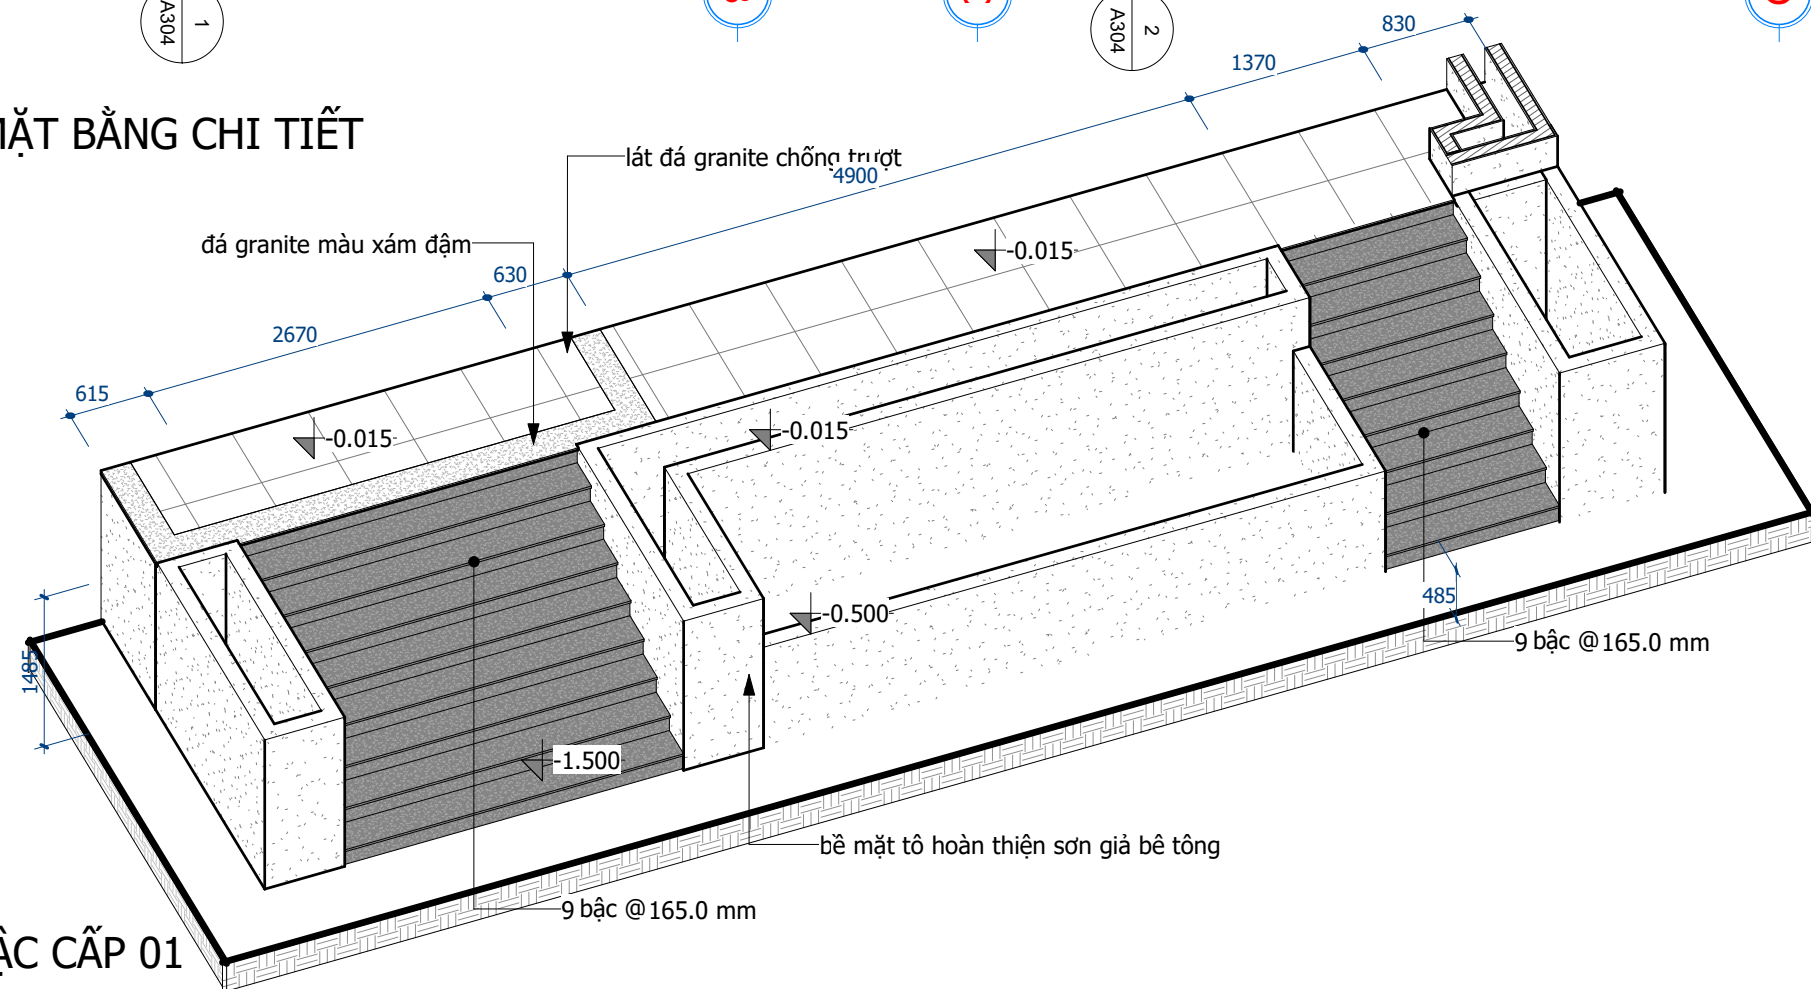


2 PHỐI CẢNH BẬC CẤP 01

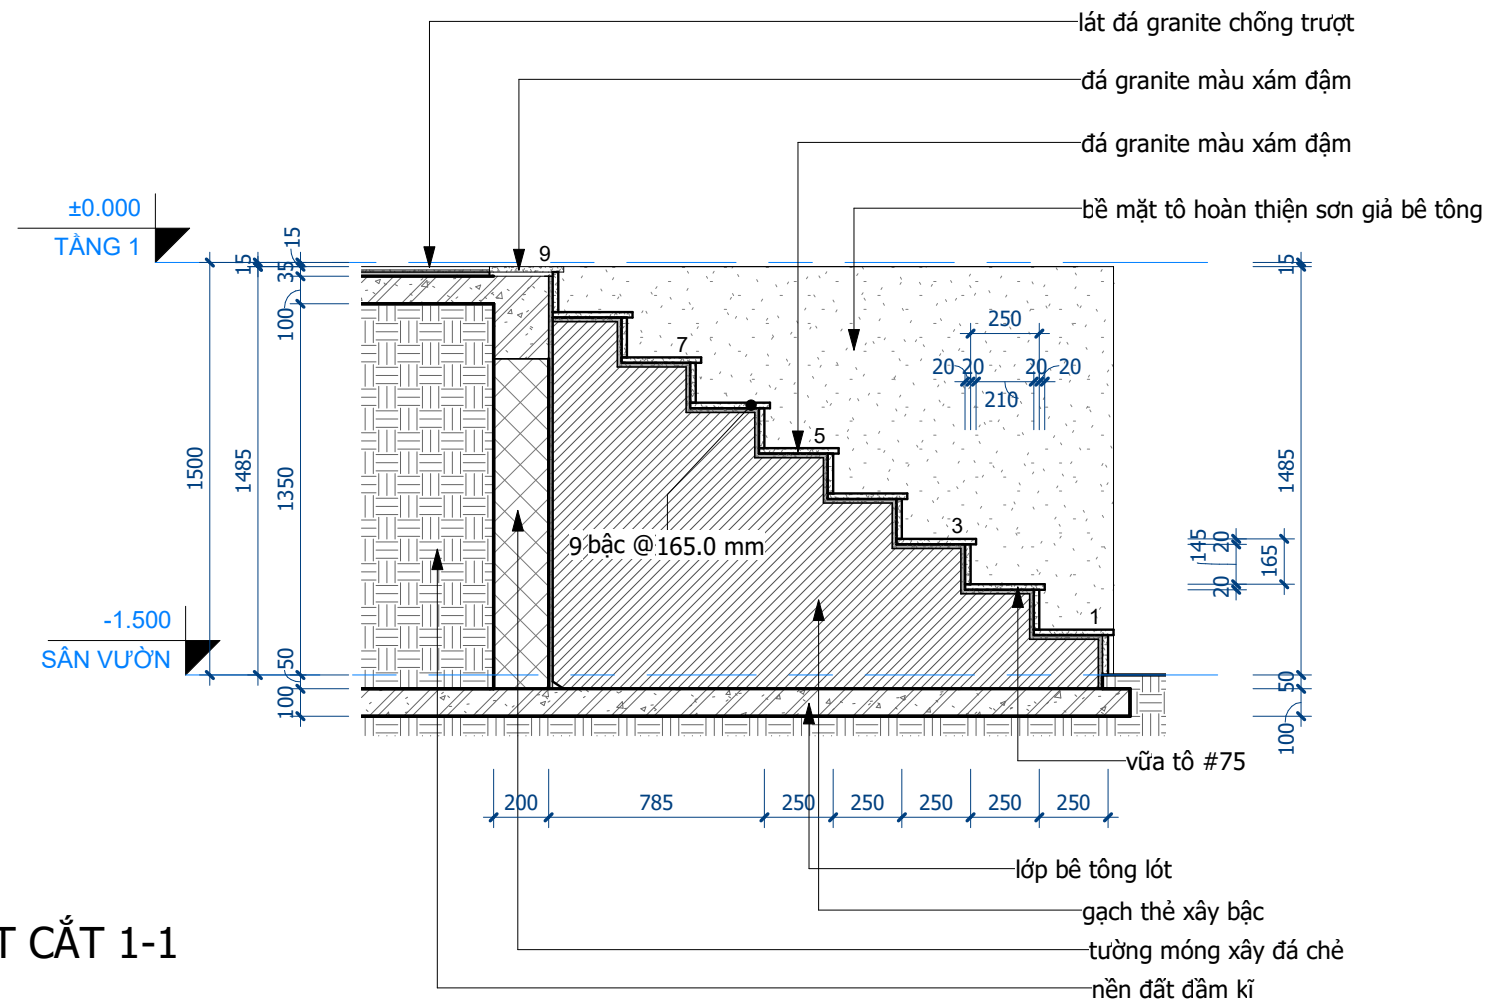


1 BẬC CẤP 01- MẶT CẮT 1-1
1 : 25

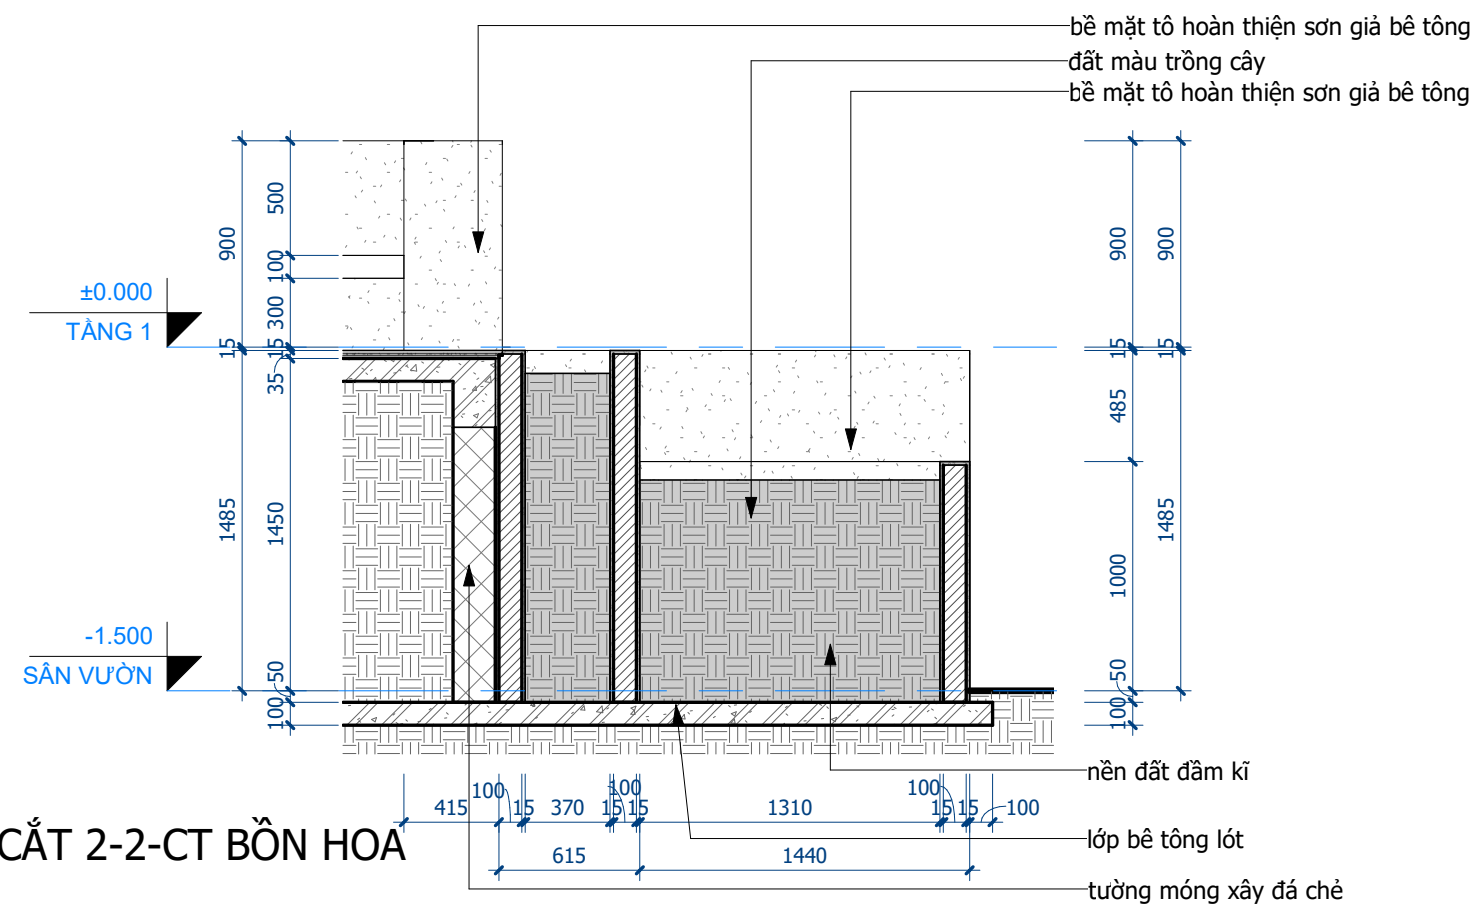


2 BẬC CẤP 01-MẶT CẮT 2-2-CT BỒN HOA
1 : 30

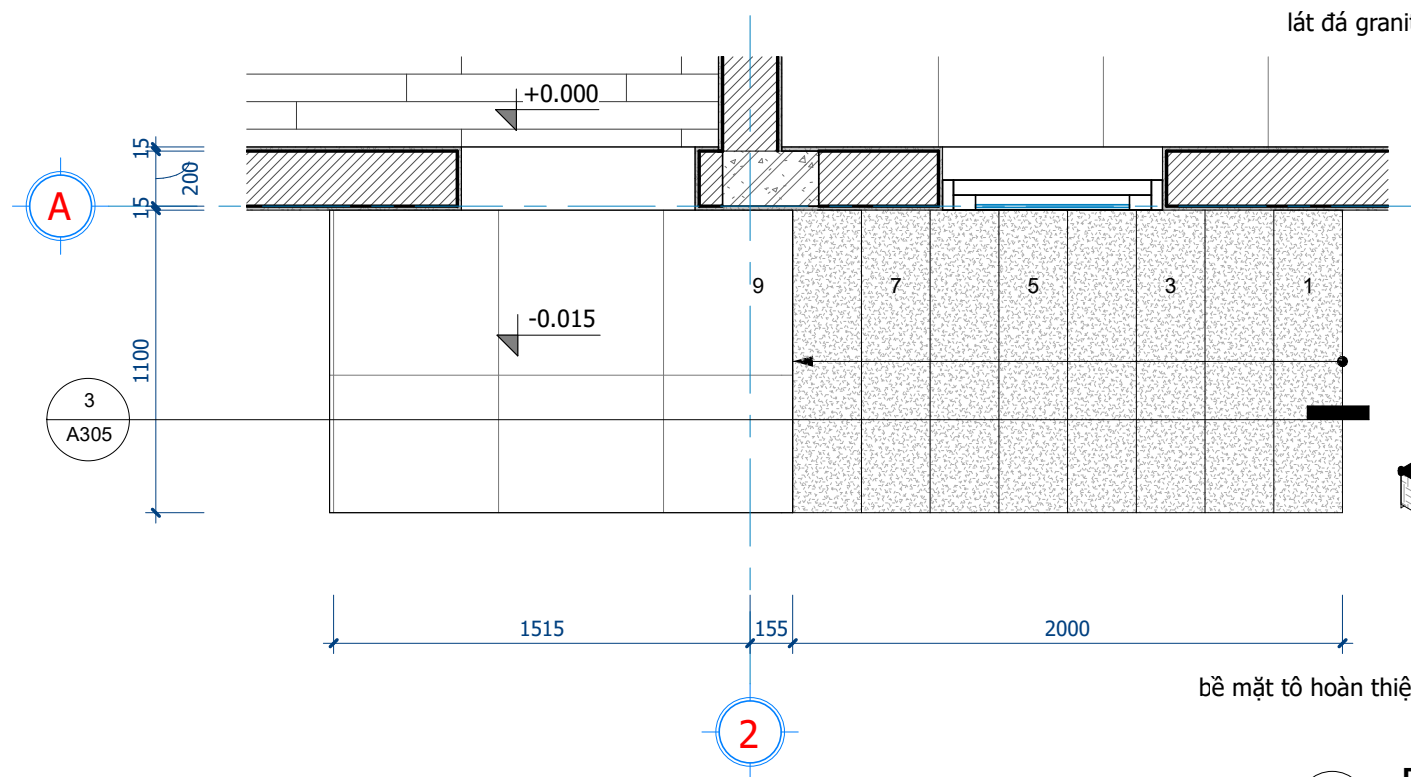


1 BẬC CẤP 02- MẶT BẰNG CHI TIẾT
1 : 25

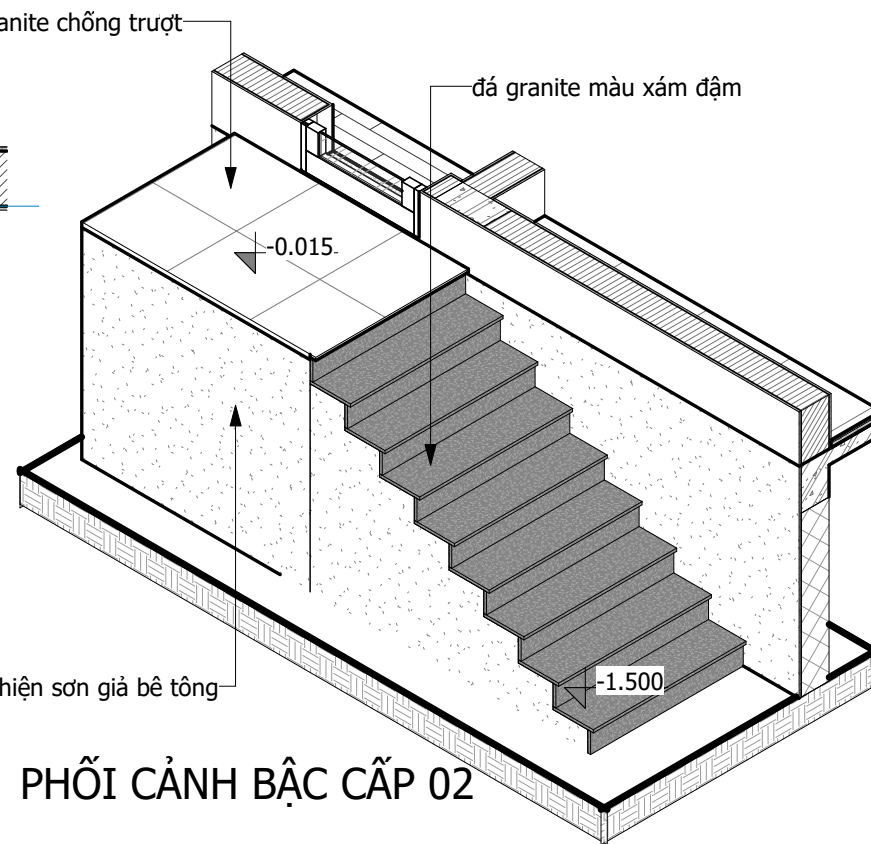

2 PHỐI CẢNH BẬC CẤP 02

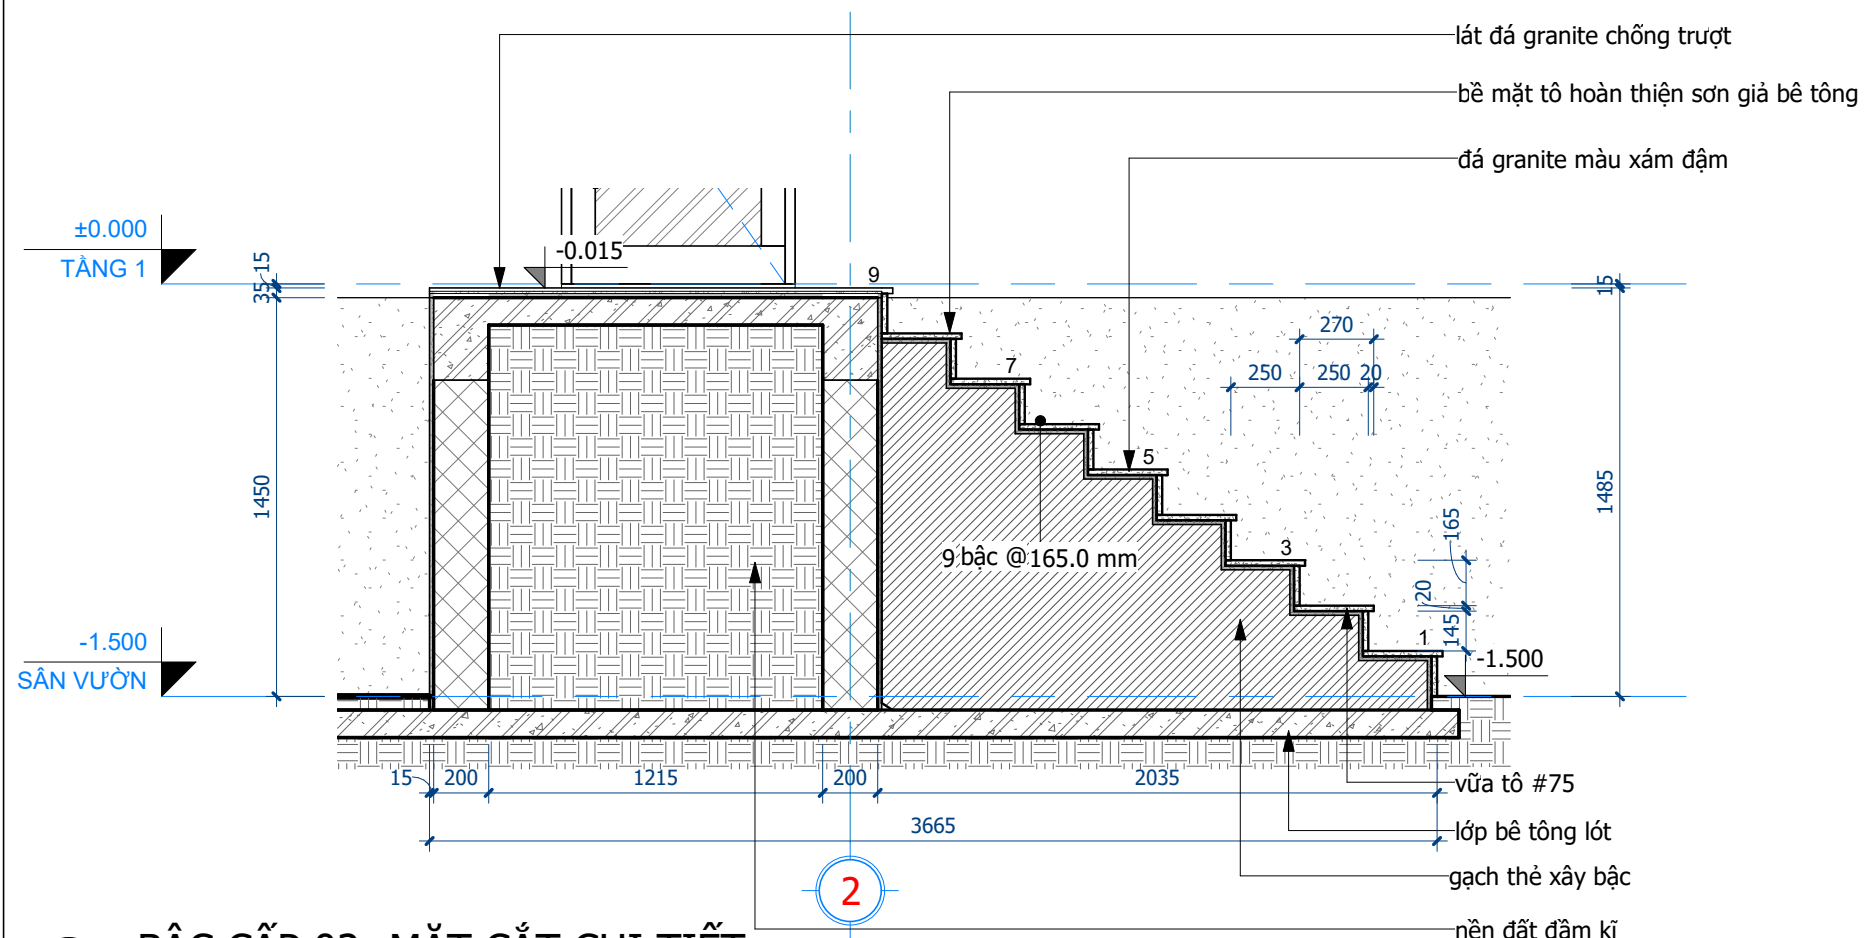


3 BẬC CẤP 02- MẶT CẮT CHI TIẾT
1 : 25

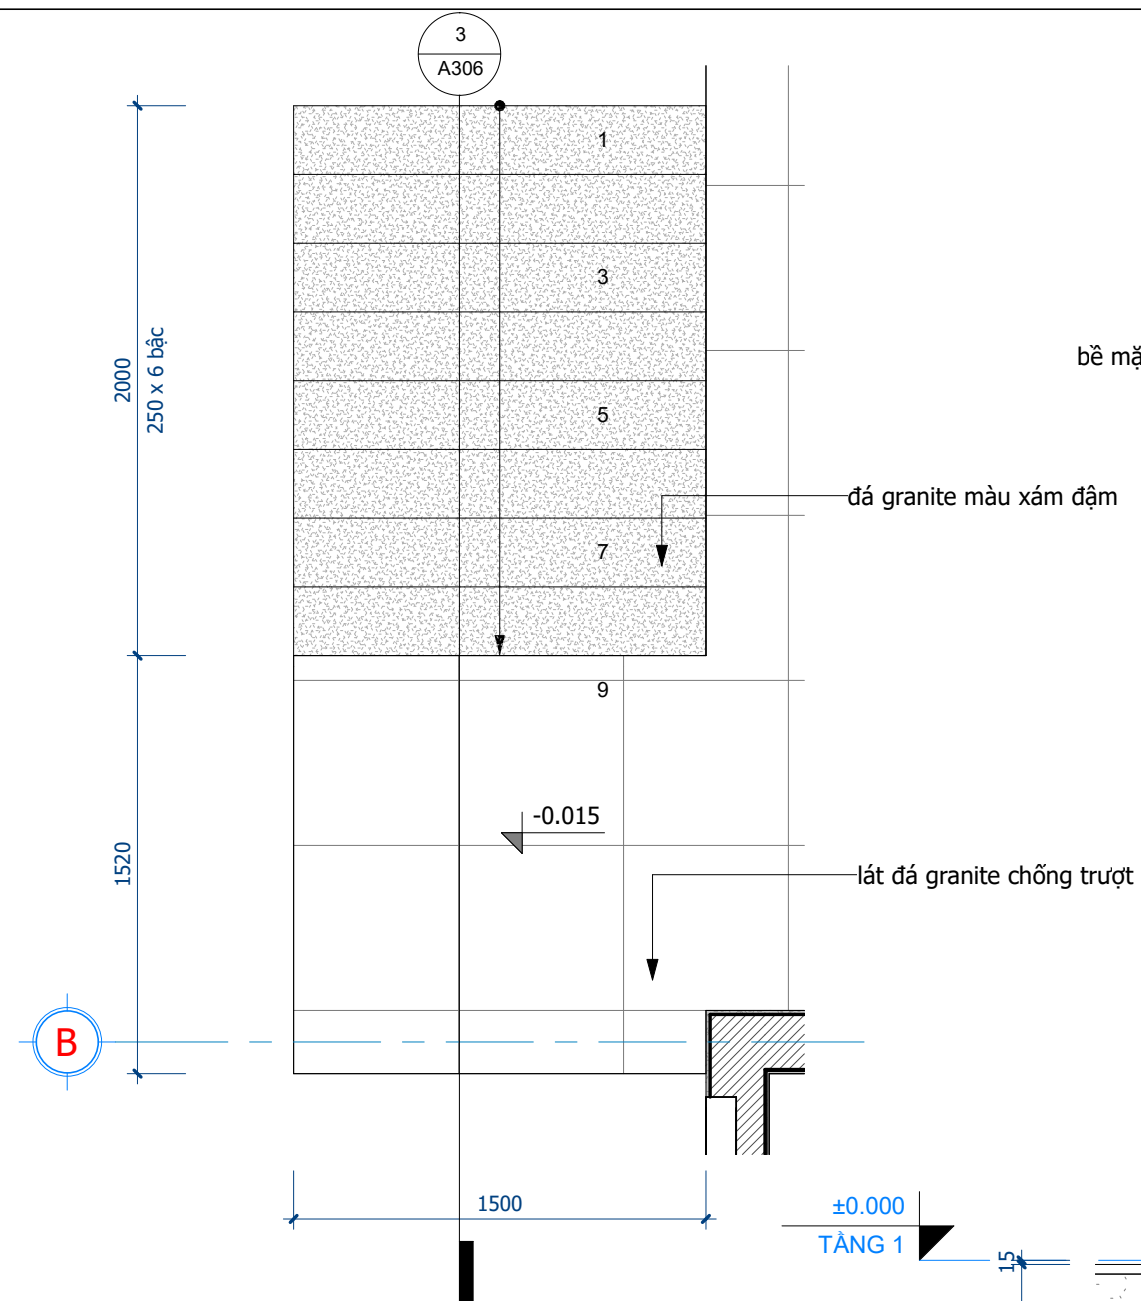



1 BẬC CẤP 03-MẶT BẰNG CHI TIẾT
1 : 25

3 BẬC CẤP 03- MẶT CẮT CHI TIẾT
1 : 25

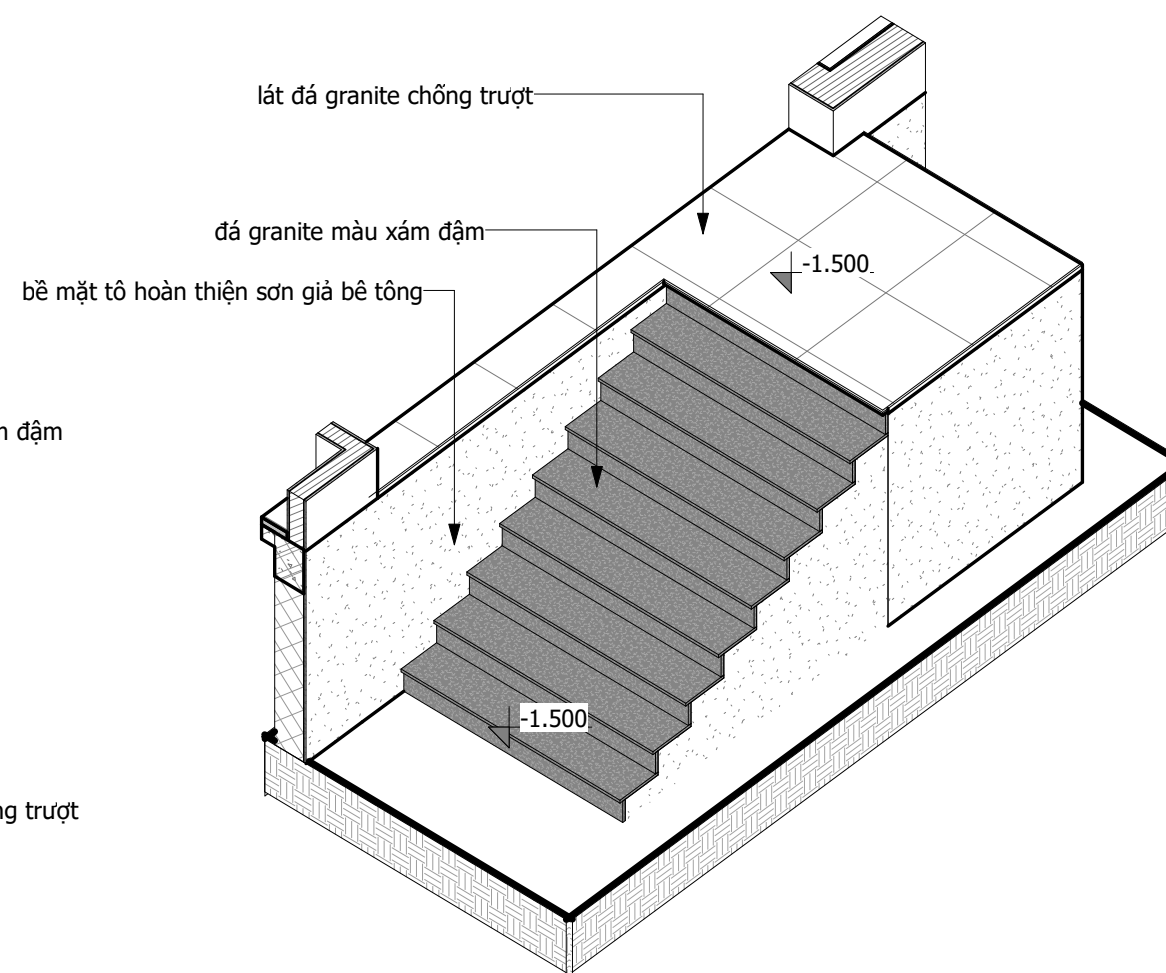


2 PHỐI CẢNH BẬC CẤP 03

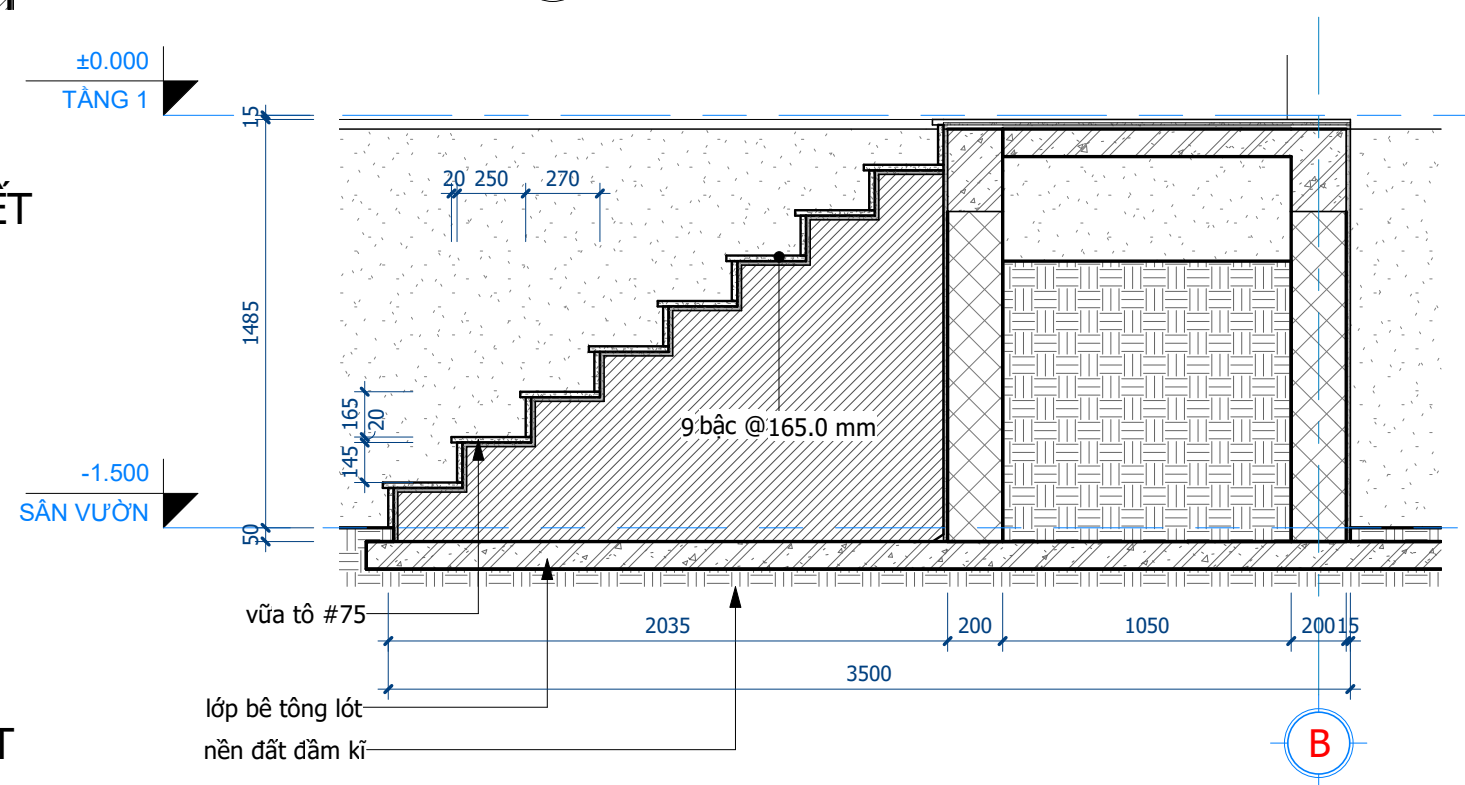


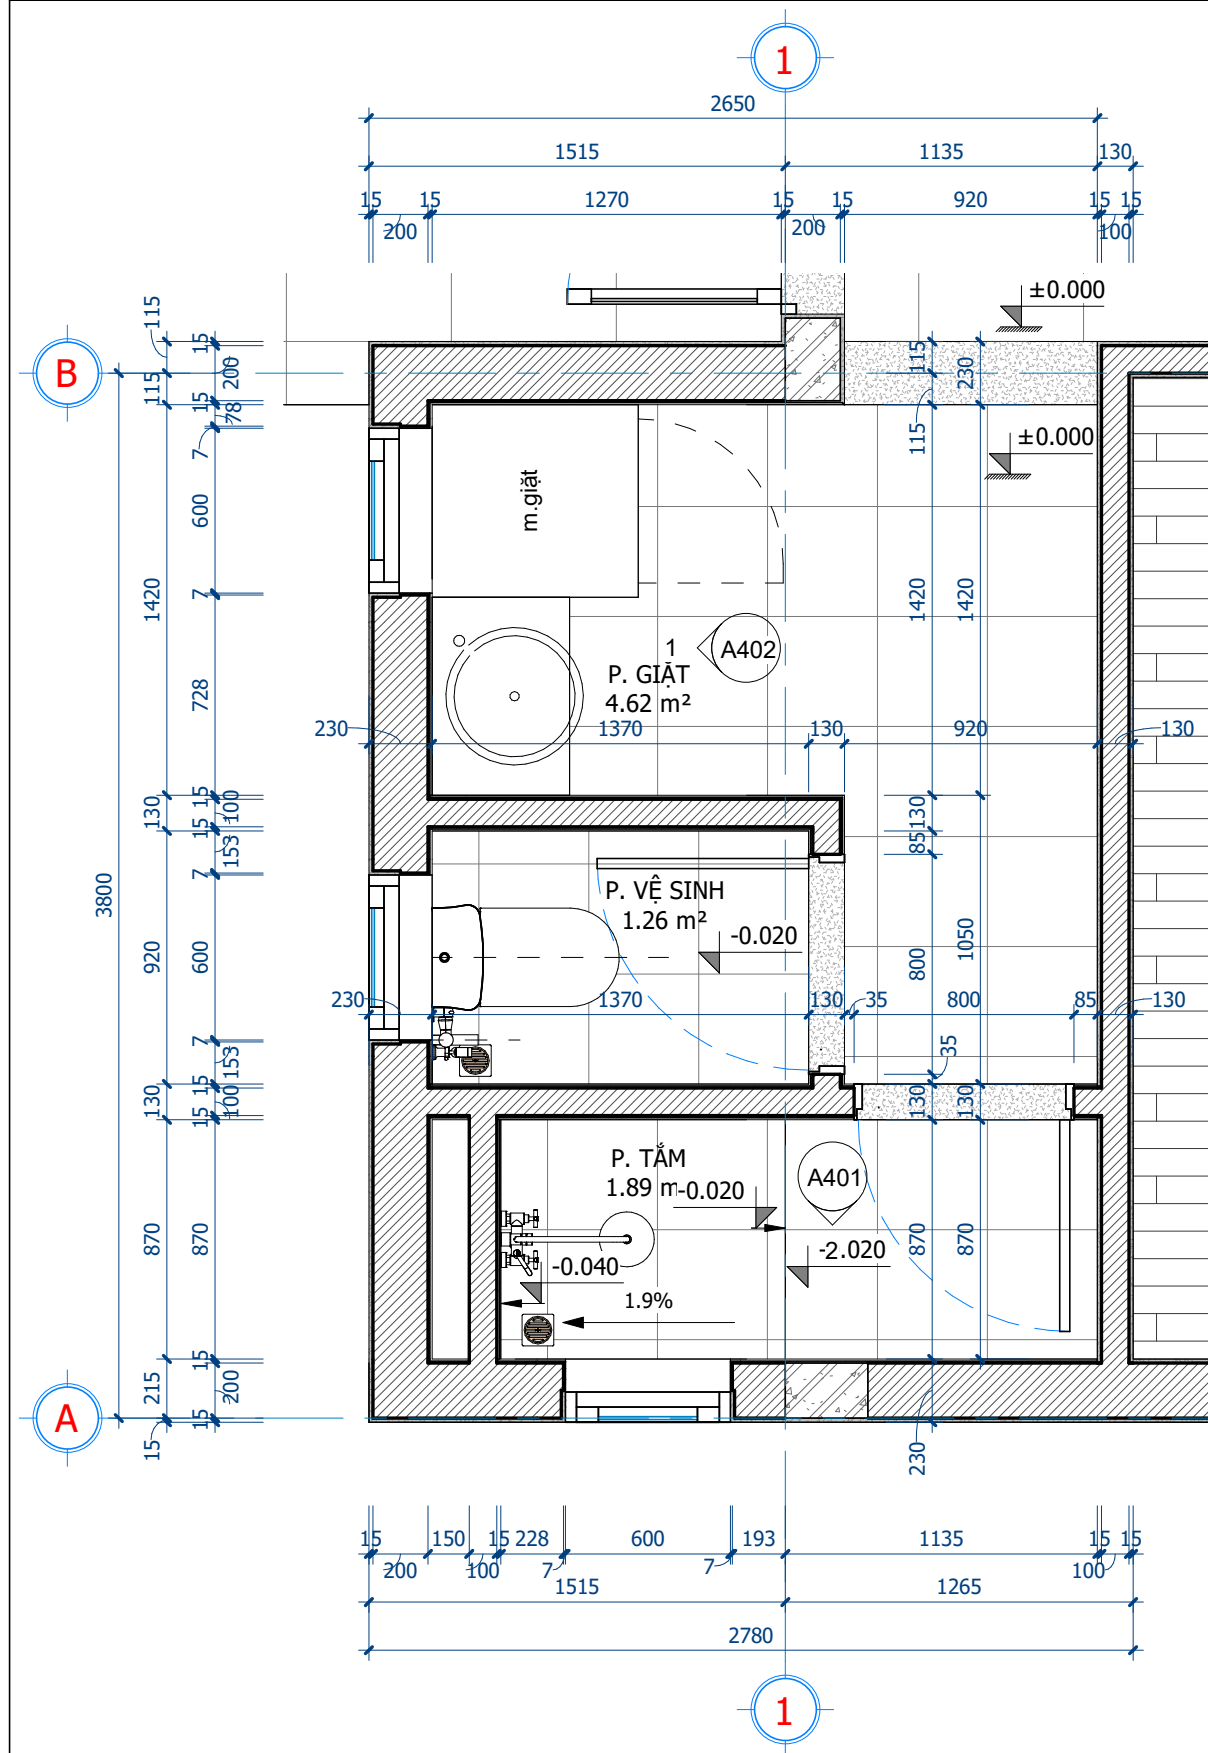


1 MẶT BẰNG PHÒNG VS 1
1 : 25

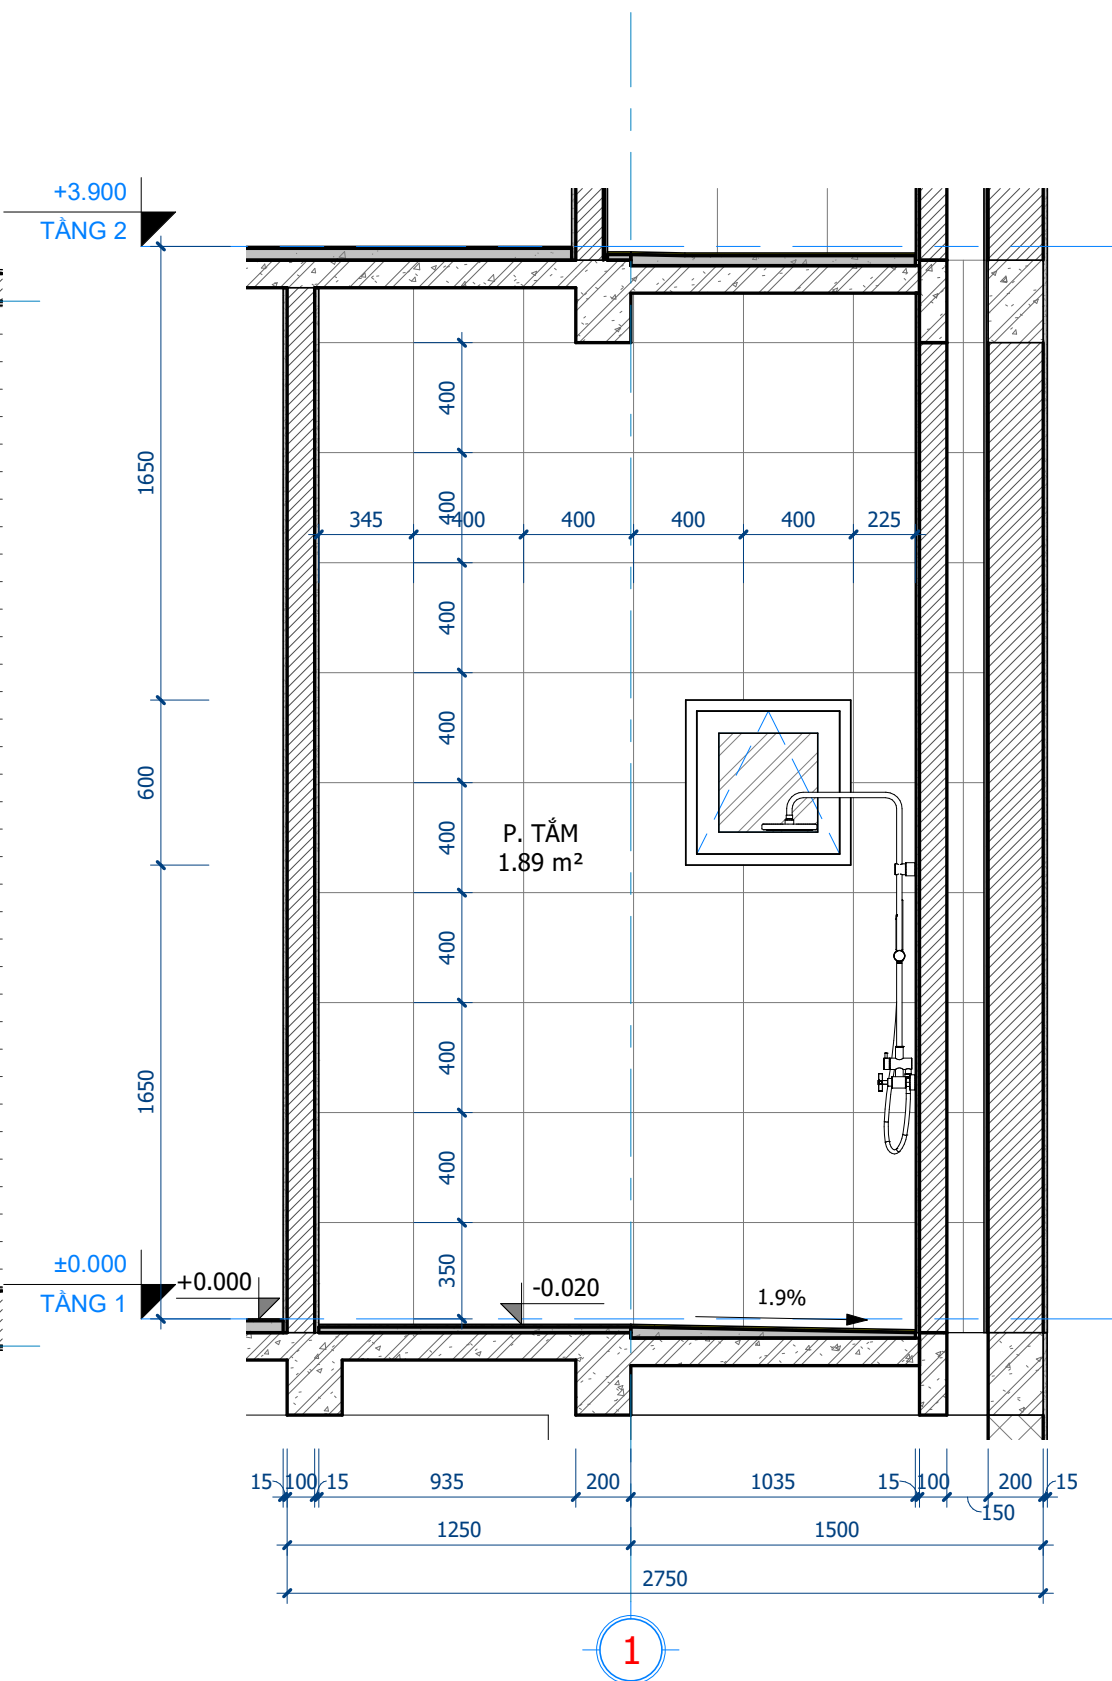


2 VS1- MẶT CẮT 2-2
1 : 25

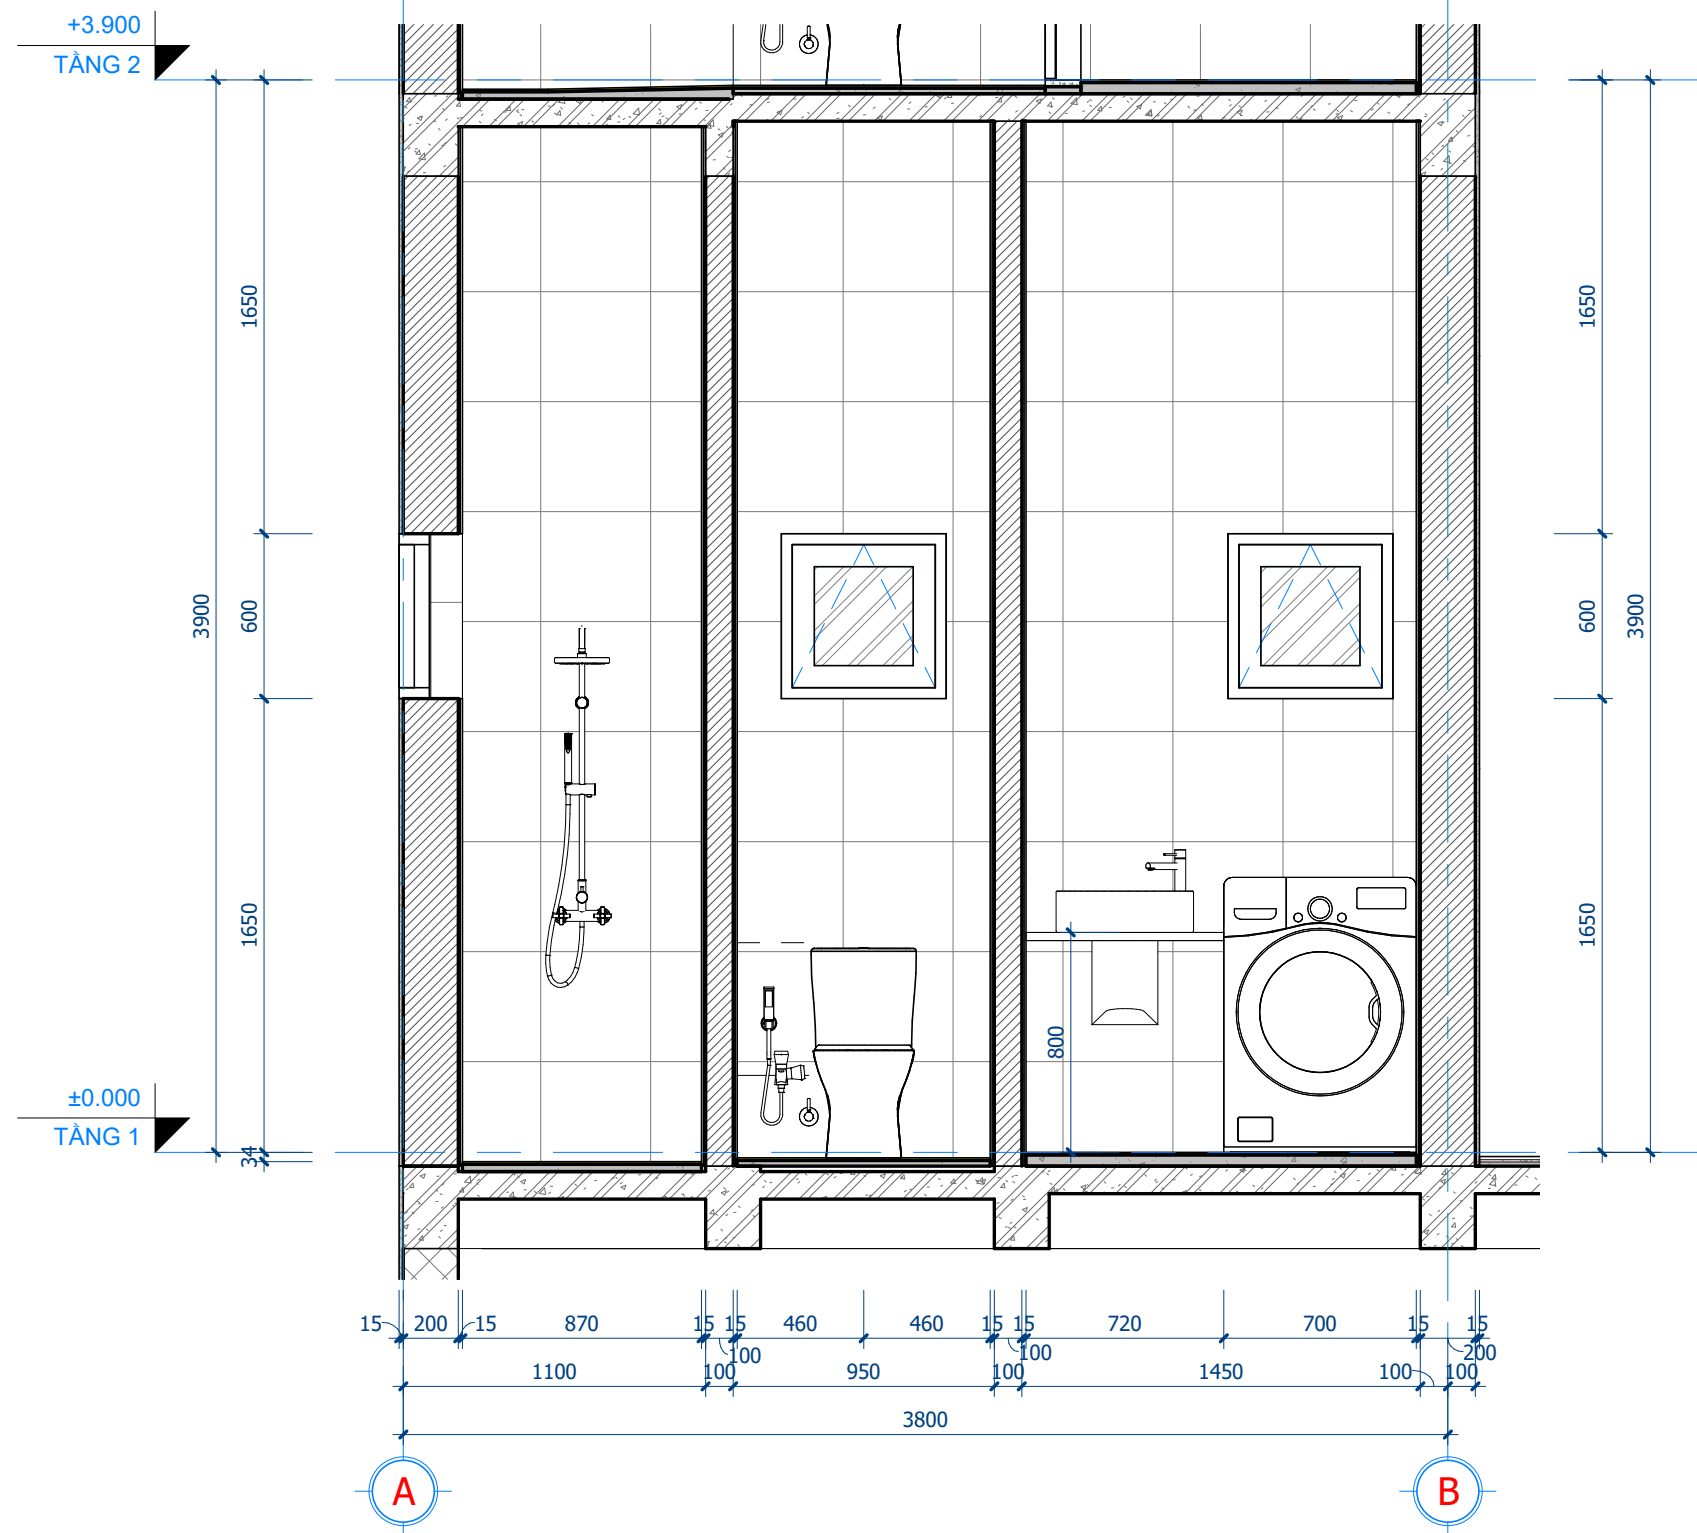


1 VS1-MẶT CẮT 1-1
1 : 25

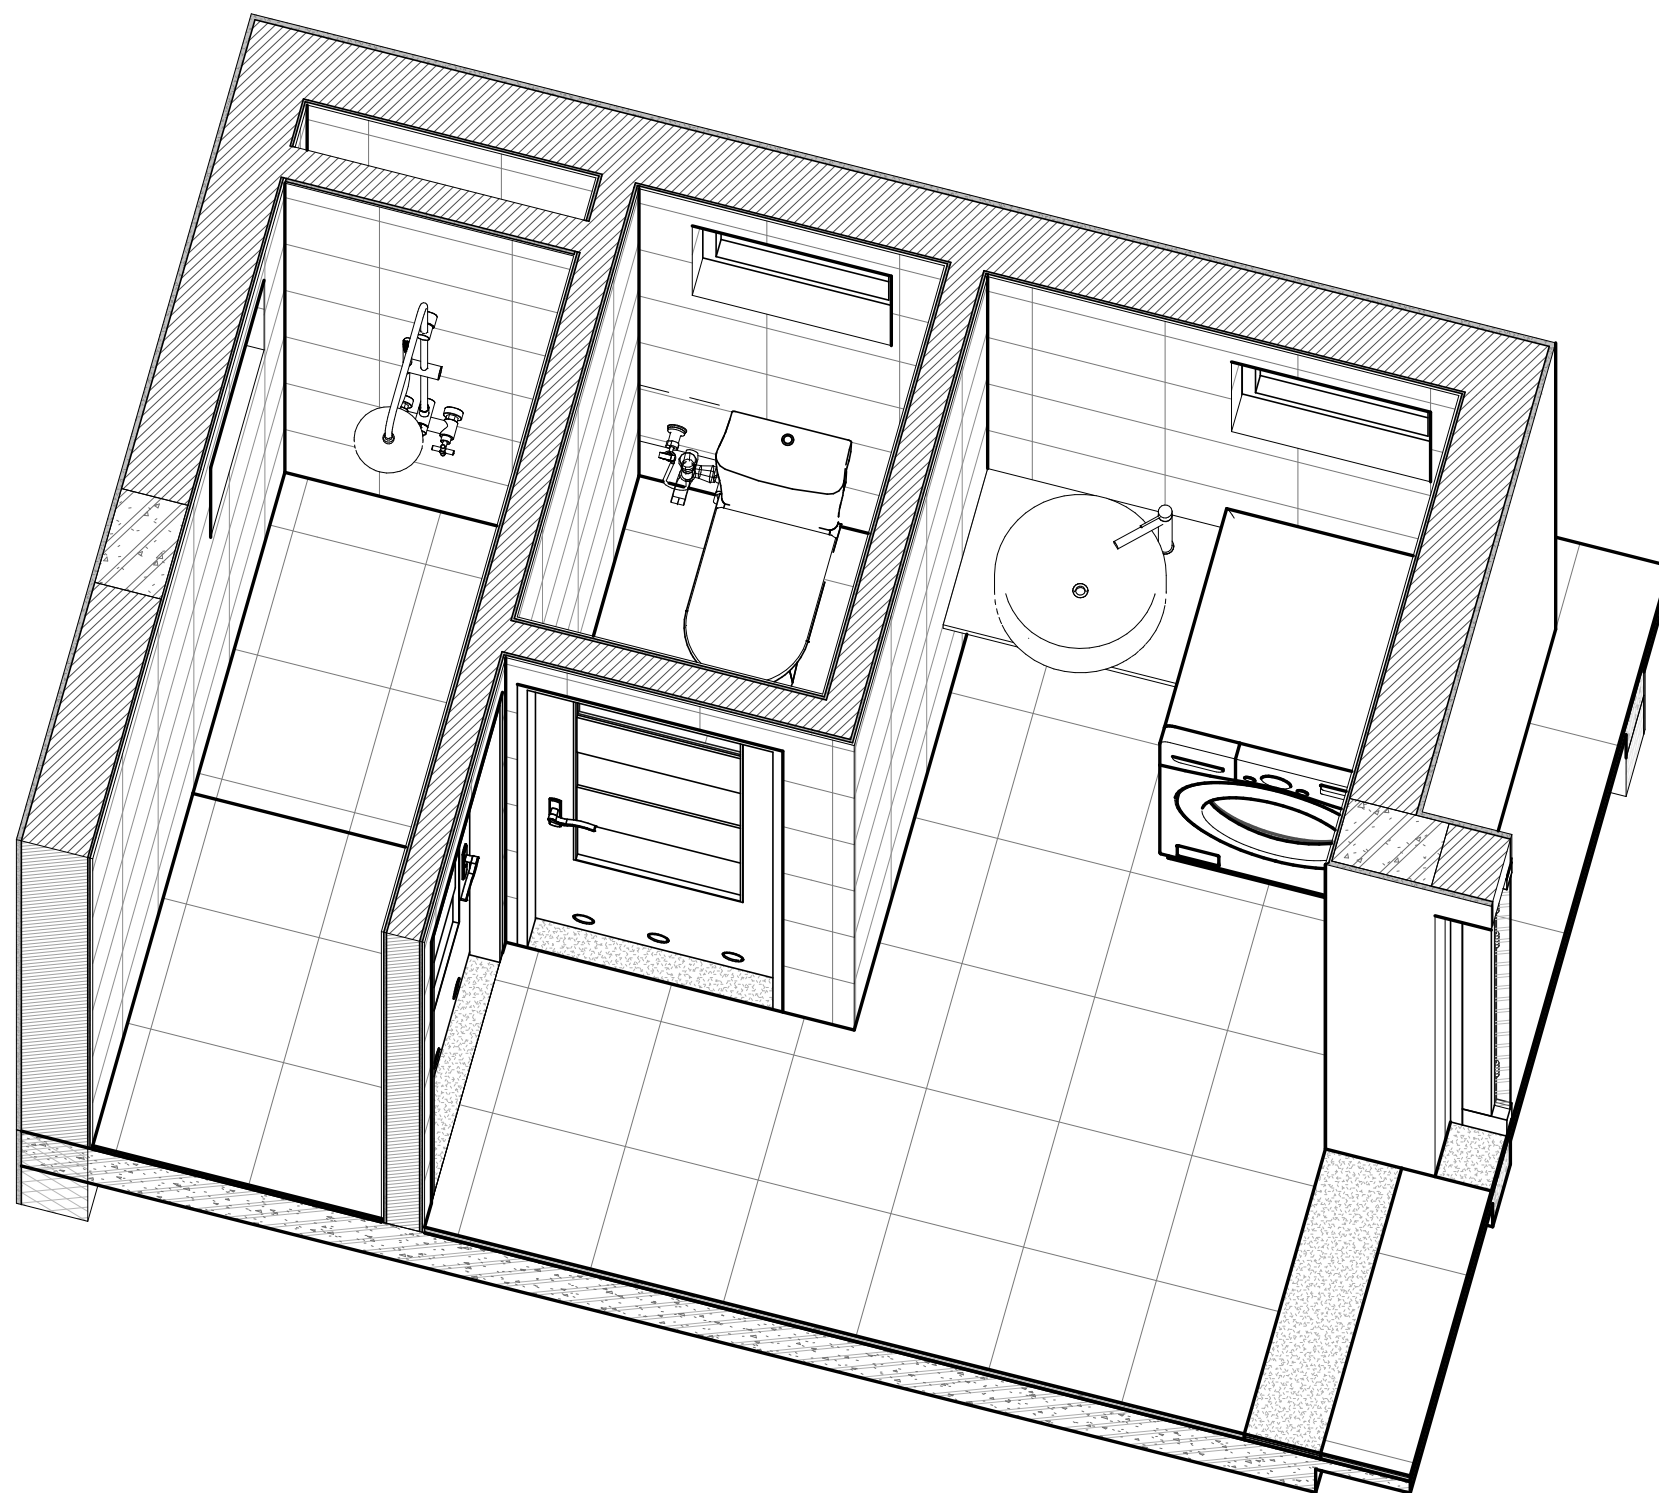


1 PHỐI CẢNH VS 1

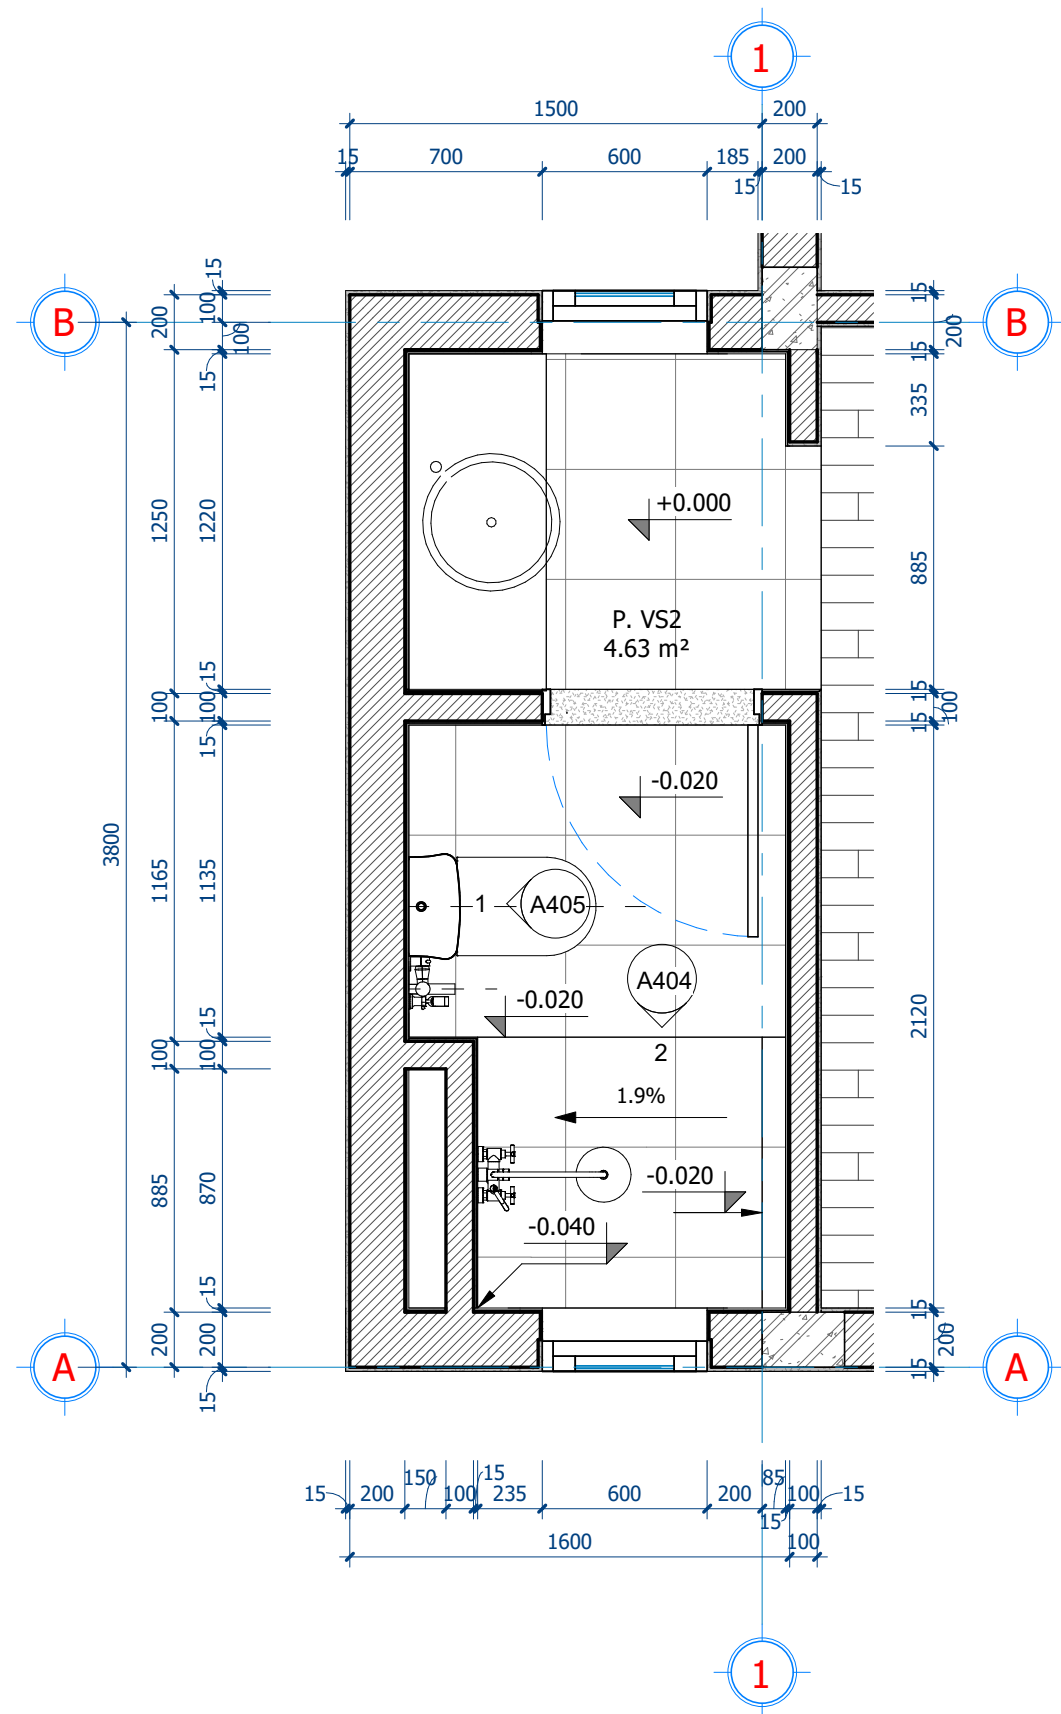


1 VS2- MẶT BẰNG CHI TIẾT
1 : 25

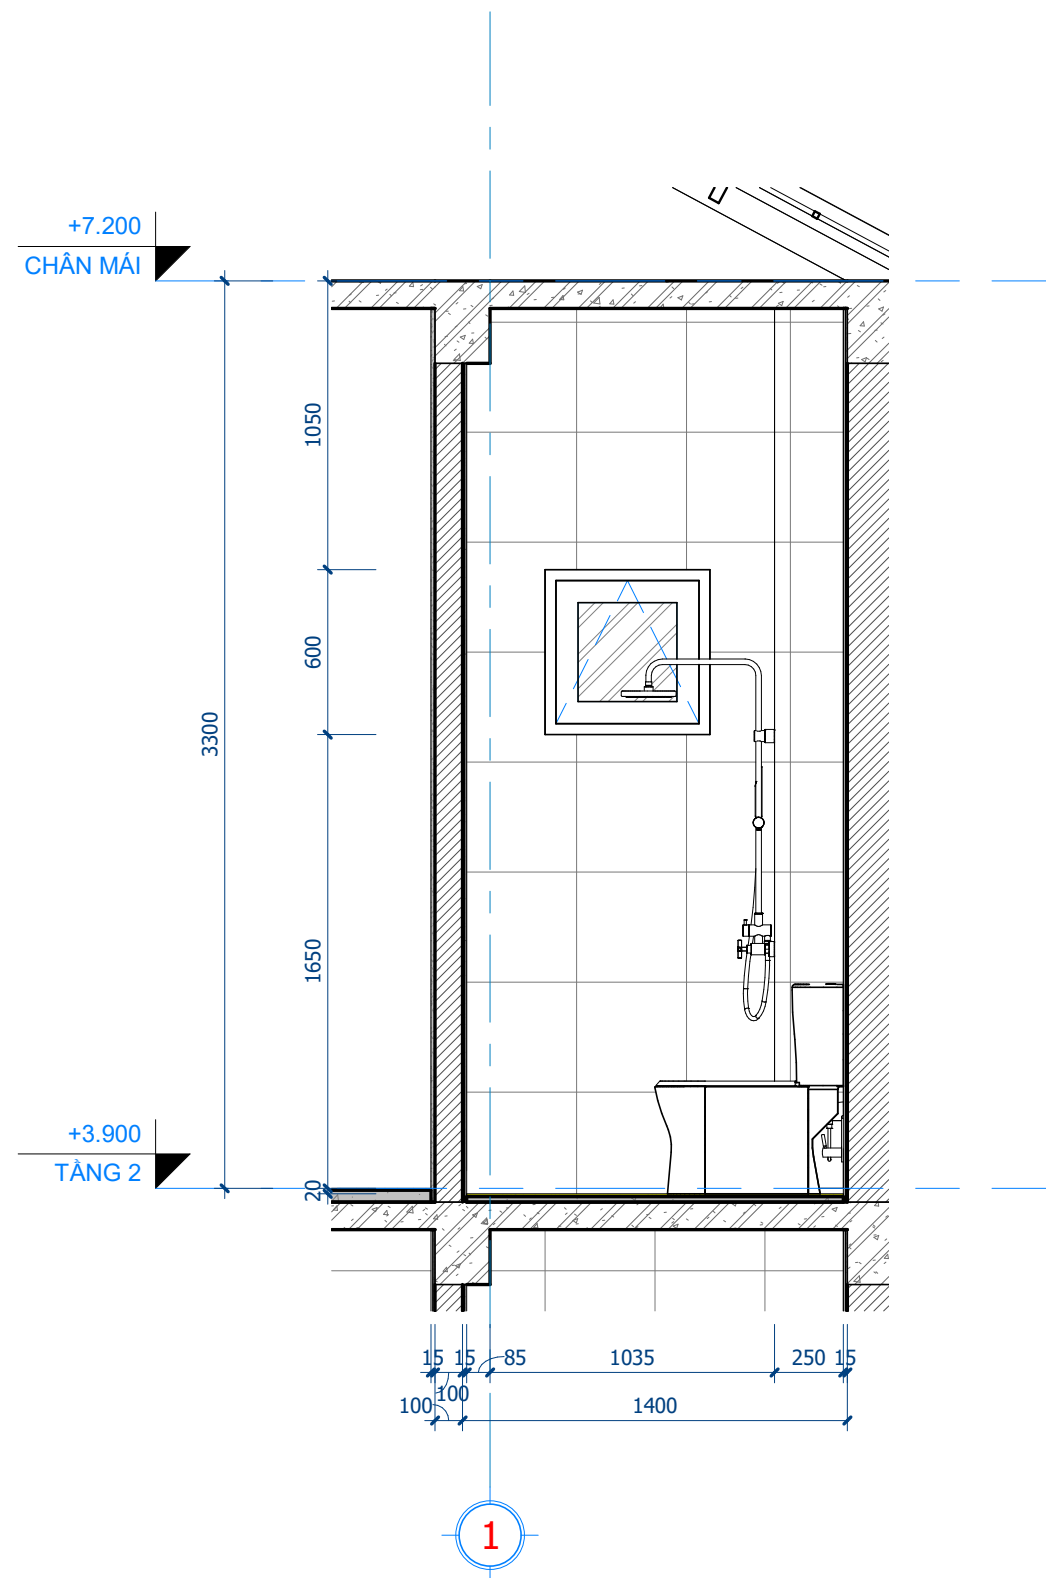


2 VS2- MẶT CẮT 2-2
1 : 25

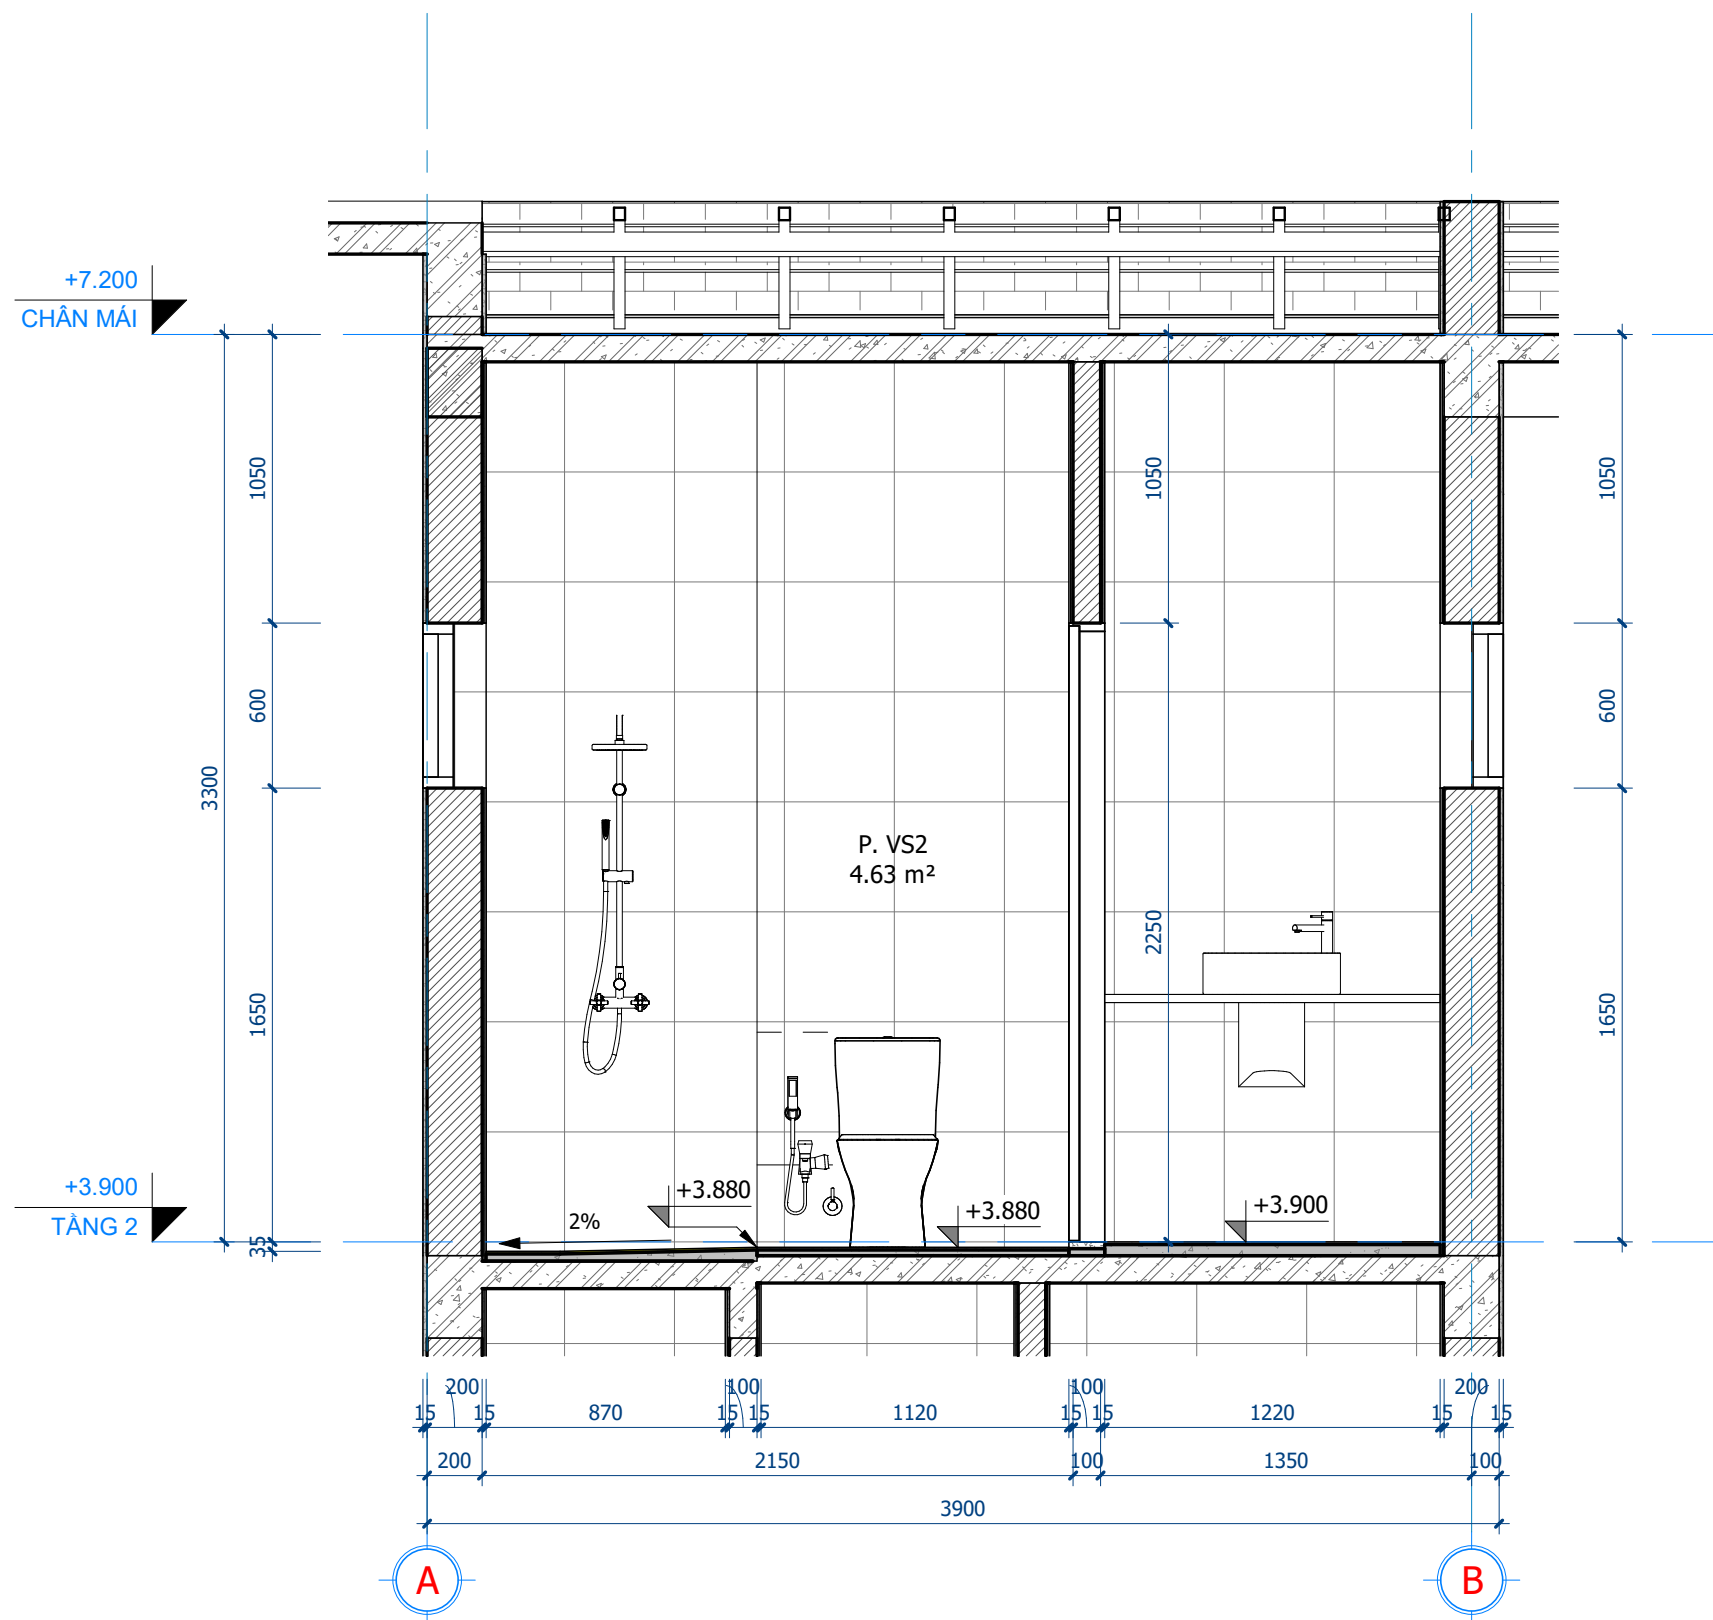


1 VS2- MẶT CẮT 1-1
1 : 25

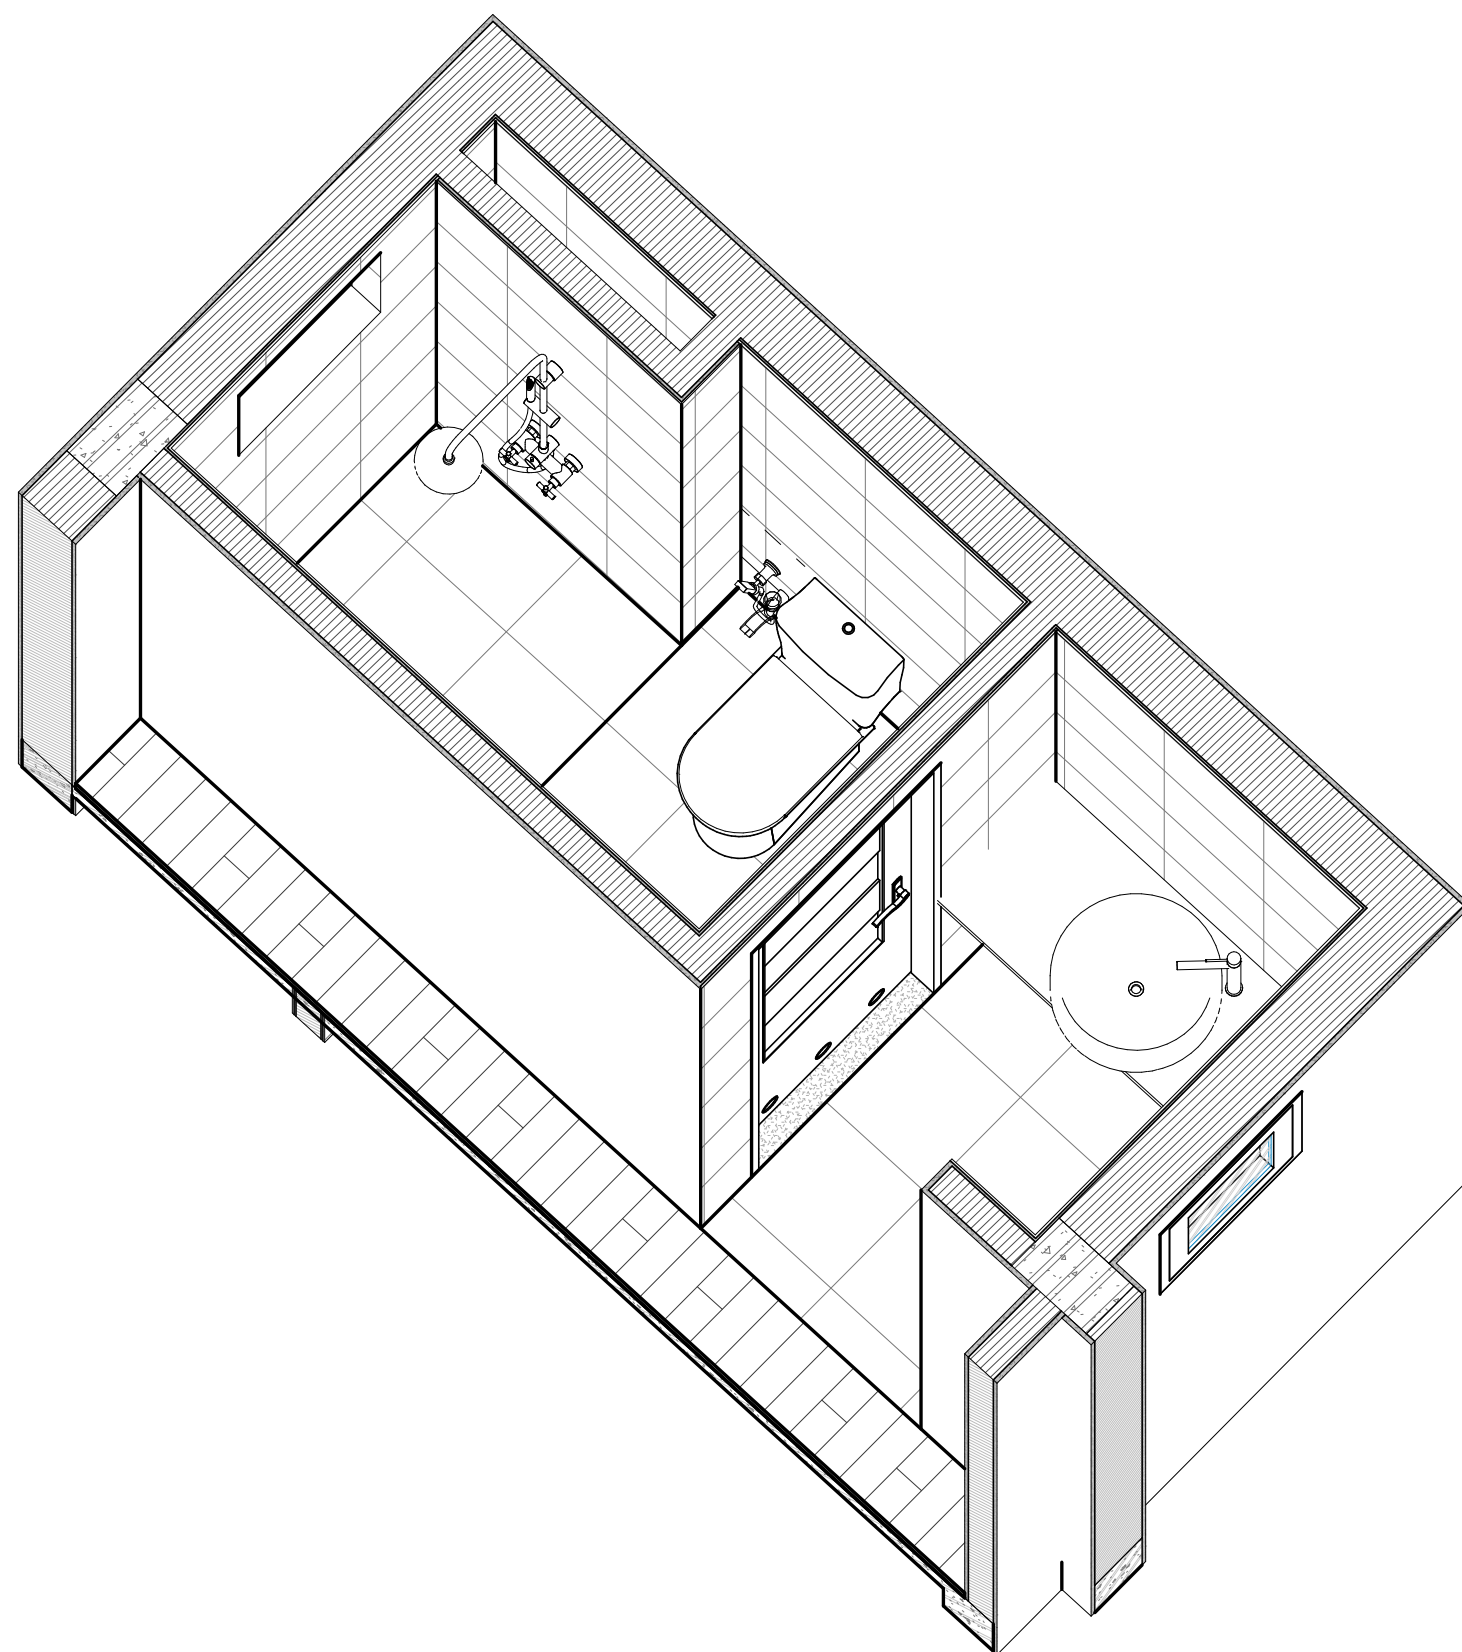


1 PHỐI CẢNH P. VỆ SINH 2

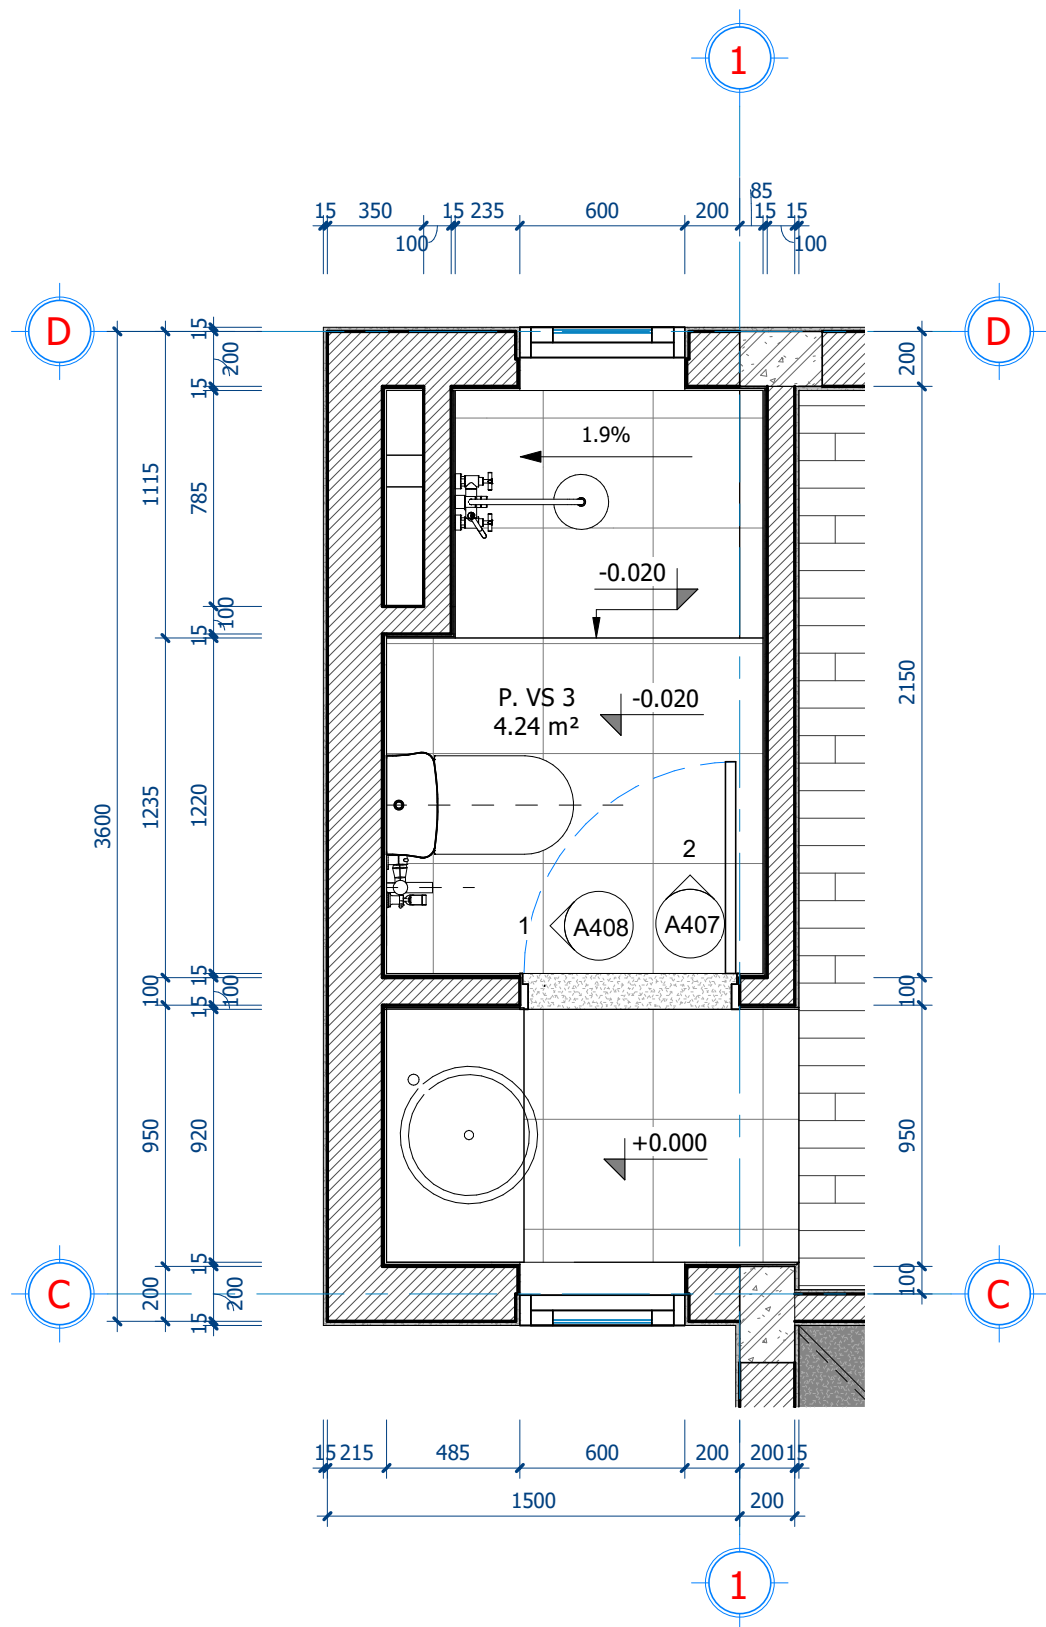

1 VS3- MẶT BẰNG
1 : 25

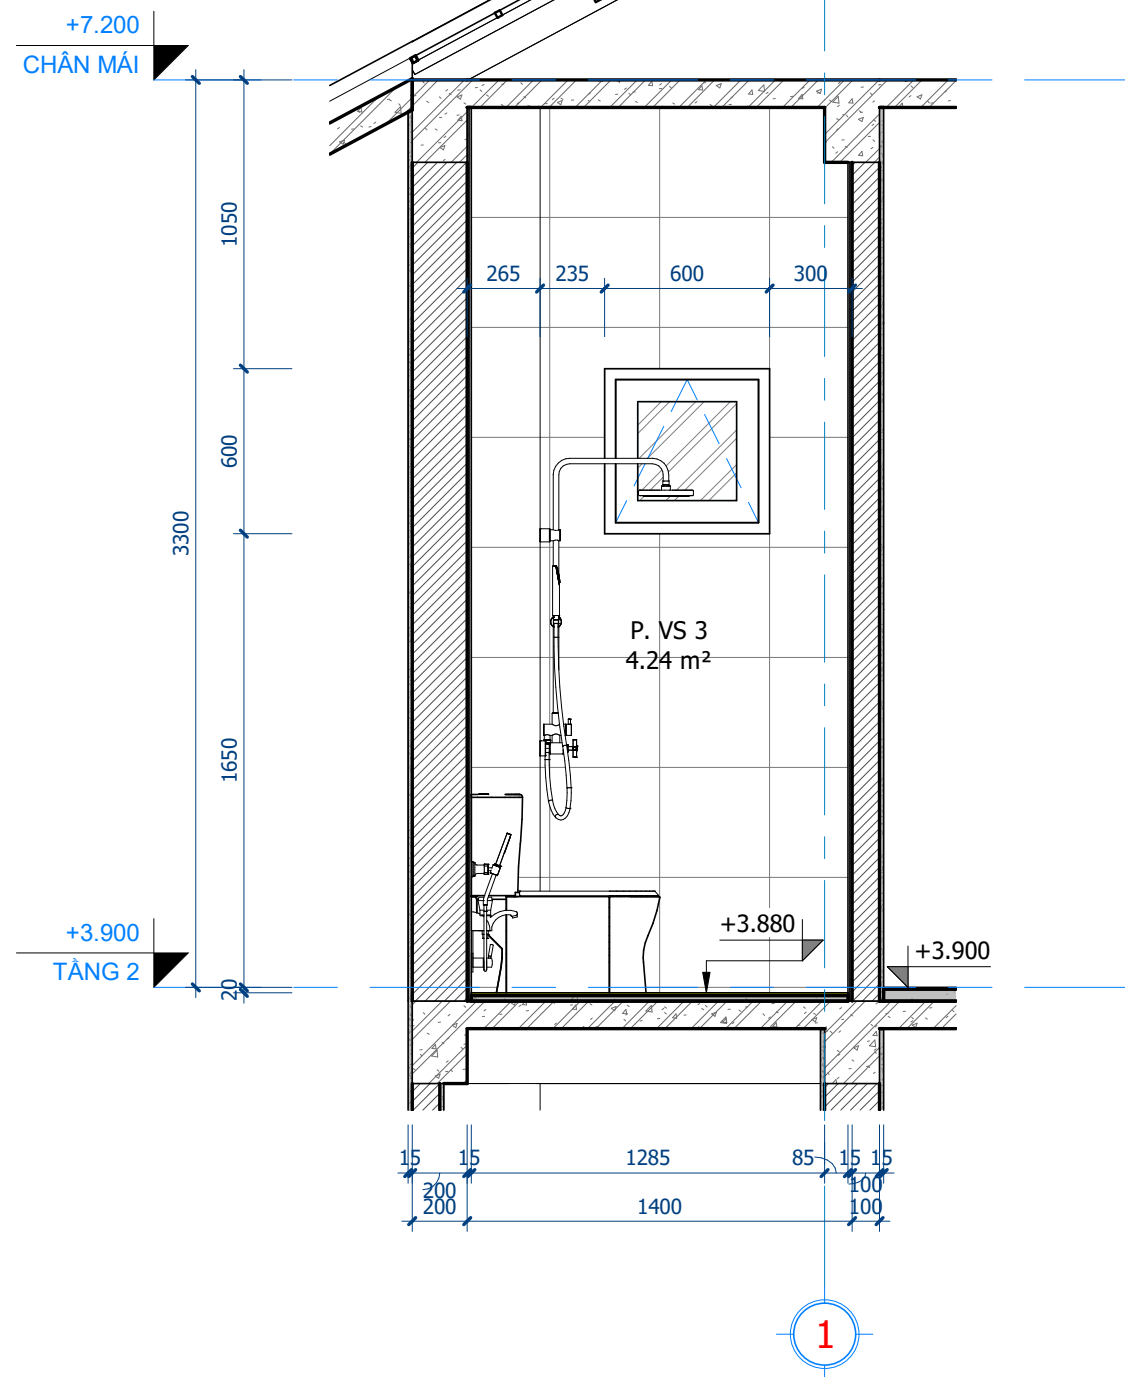


2 VS3- MẶT CẮT 2-2
1 : 25

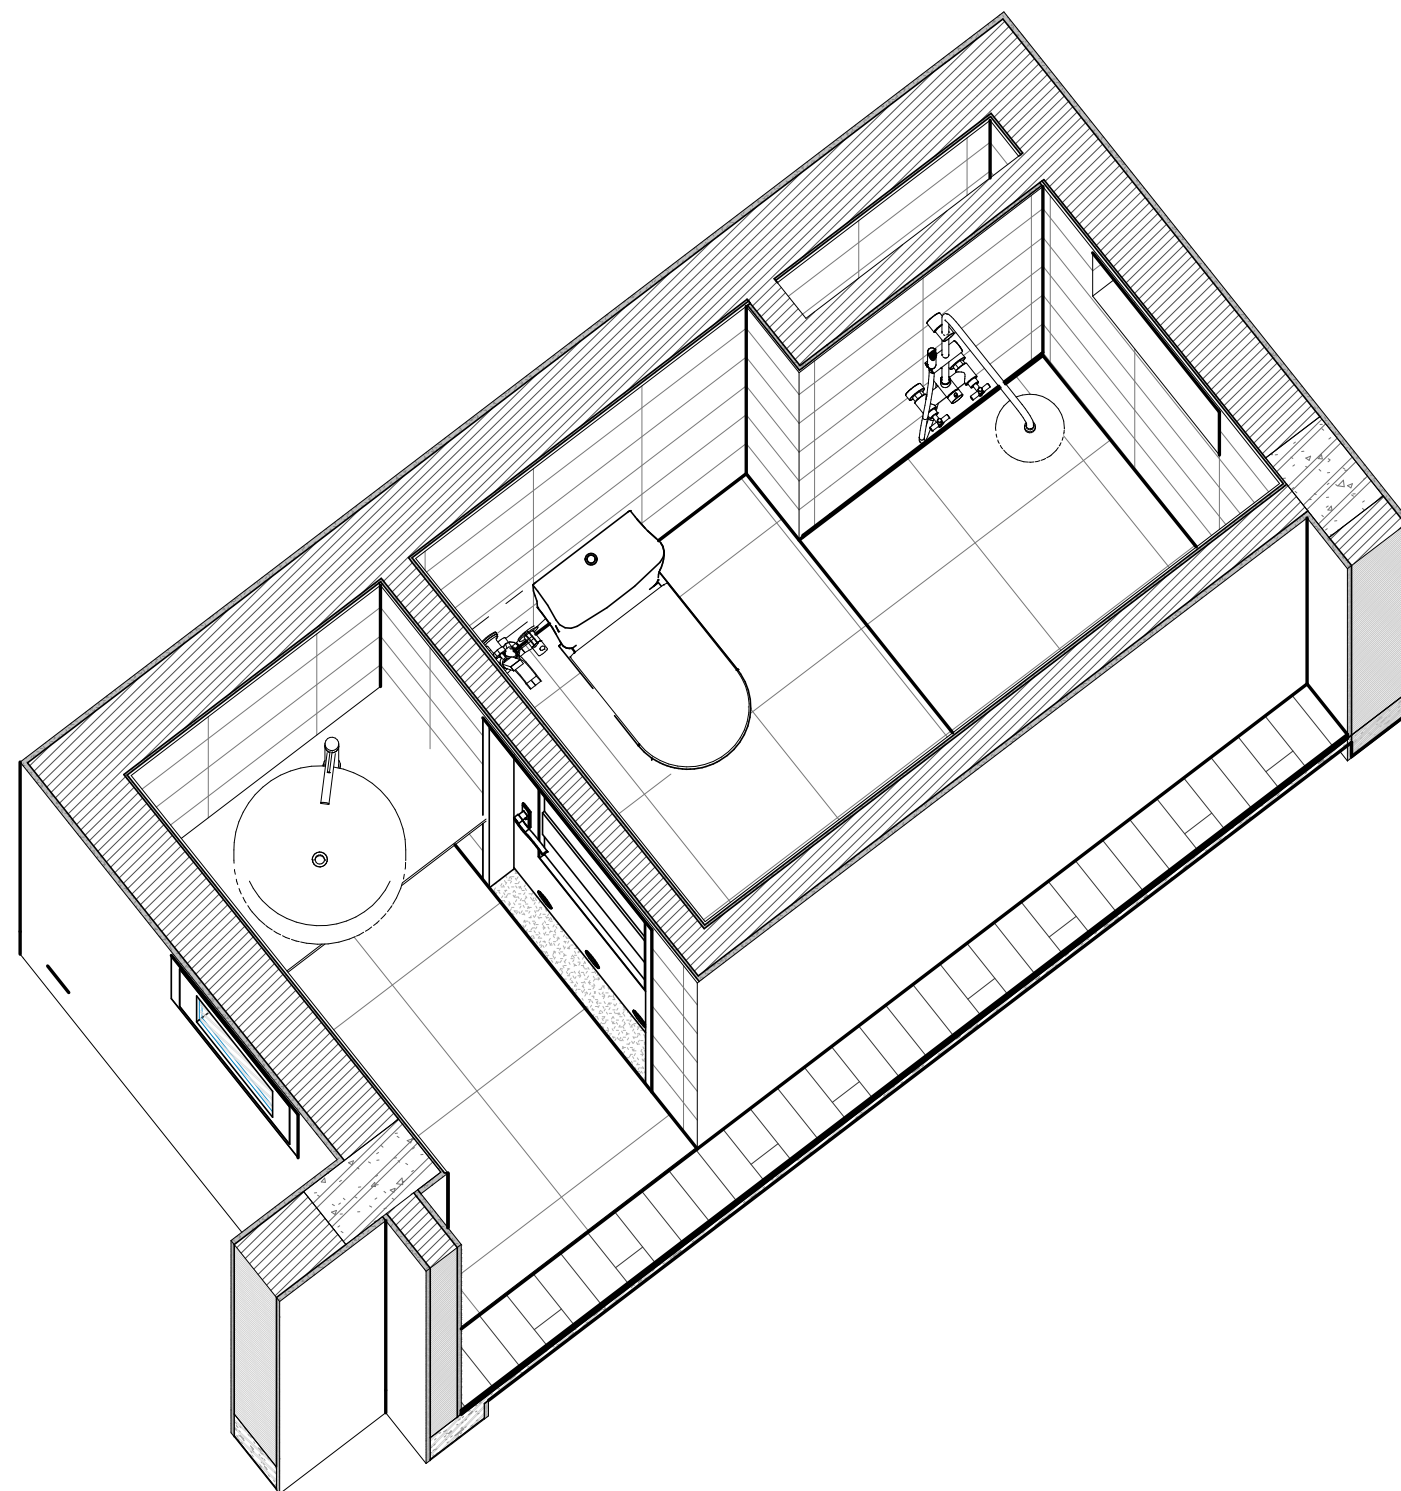


① PHỐI CẢNH P. VỆ SINH 3

THỐNG KÊ CỬA ĐI						
TẦNG	KÝ HIỆU	CHIỀU CAO	CHIỀU RỘNG	DIỄN GIẢI		SỐ LƯỢNG
SÂN VƯỜN	D12	2200	4000			1
TẦNG 1	D1	3000	3000	CỬA ĐI 4 CÁCH MỞ DẠNG GẤP, PHẦN LẤY SÁNG BÊN TRÊN CỐ ĐỊNH, VẬT LIỆU KHUNG NHÔM XINGFA, KÍNH TRONG SUỐT DÀY 10mm		1
TẦNG 1	D2	3000	1800	CỬA ĐI 1 CÁCH MỞ QUAY, PHẦN LẤY SÁNG CỐ ĐỊNH ĐẦU VÀ CẠNH CỬA, VẬT LIỆU KHUNG NHÔM XINGFA, KÍNH TRONG SUỐT DÀY 10mm		1
TẦNG 1	D3	3000	1800	CỬA ĐI 2 CÁCH MỞ TRƯỢT, KHUNG NHÔM XINGFA, KÍNH TRONG SUỐT DÀY 10mm		1
TẦNG 1	D4	3000	1400	CỬA ĐI 2 CÁCH MỞ TRƯỢT, KHUNG NHÔM XINGFA, KÍNH TRONG SUỐT DÀY 10mm		1
TẦNG 1	D5	2200	950	CỬA ĐI 1 CÁCH MỞ QUAY, KHUNG VÀ CÁCH GỖ, NỆP CHỈ TRANG TRÍ MẠ VÀNG		2
TẦNG 1	D6	2250	850	CỬA ĐI 1 CÁCH MỞ QUAY, KHUNG NHÔM XINGFA, KÍNH TRONG SUỐT DÀY 10mm		2
TẦNG 1	D7	2250	800	CỬA ĐI 1 CÁCH MỞ QUAY, KHUNG VÀ CÁCH GỖ, NỆP CHỈ TRANG TRÍ MẠ VÀNG		2
TẦNG 2	D5	2200	950	CỬA ĐI 1 CÁCH MỞ QUAY, KHUNG VÀ CÁCH GỖ, NỆP CHỈ TRANG TRÍ MẠ VÀNG		2
TẦNG 2	D7	2250	800	CỬA ĐI 1 CÁCH MỞ QUAY, KHUNG VÀ CÁCH GỖ, NỆP CHỈ TRANG TRÍ MẠ VÀNG		2
TẦNG 2	D8	2250	2500	CỬA ĐI 1 CÁCH MỞ QUAY, PHẦN LẤY SÁNG CỐ ĐỊNH CẠNH CỬA, VẬT LIỆU KHUNG NHÔM XINGFA, KÍNH TRONG SUỐT DÀY 10mm		1
TẦNG 2	D9	2250	1400	CỬA ĐI 2 CÁCH MỞ TRƯỢT, KHUNG NHÔM XINGFA, KÍNH TRONG SUỐT DÀY 10mm		1
TẦNG 2	D10	2750	1800	CỬA ĐI 2 CÁCH MỞ QUAY, KHUNG NHÔM XINGFA, KÍNH TRONG SUỐT DÀY 10mm		1
TẦNG 2	D11	2750	3000	CỬA ĐI 4 CÁCH MỞ DẠNG GẤP, PHẦN LẤY SÁNG BÊN TRÊN CỐ ĐỊNH, VẬT LIỆU KHUNG NHÔM XINGFA, KÍNH TRONG SUỐT DÀY 10mm		1



THỐNG KÊ CỬA SỔ						
Level	KÝ HIỆU	CHIỀU CAO	CHIỀU RỘNG	BỀ CỬA SỔ	DIỄN GIẢI	SỐ LƯỢNG
TẦNG 1	S1	2000	600	1000	CỬA SỔ 1 CÁCH MỞ LẬT LÊN TRÊN, PHẦN LẤY SÁNG BÊN TRÊN CỐ ĐỊNH, KHUNG NHÔM XINGFA, KÍNH TRONG SUỐT DÀY 10mm	1
TẦNG 1	S2	2000	800	1000	CỬA SỔ 1 CÁCH MỞ LẬT LÊN TRÊN, PHẦN LẤY SÁNG BÊN TRÊN CỐ ĐỊNH, KHUNG NHÔM XINGFA, KÍNH TRONG SUỐT DÀY 10mm	3
TẦNG 1	S3	600	600	1650	CỬA SỔ 1 CÁCH MỞ LẬT LÊN TRÊN, KHUNG NHÔM XINGFA, KÍNH TRONG SUỐT DÀY 10mm	3
TẦNG 2	S3	600	600	1650	CỬA SỔ 1 CÁCH MỞ LẬT LÊN TRÊN, KHUNG NHÔM XINGFA, KÍNH TRONG SUỐT DÀY 10mm	4
TẦNG 2	S4	1250	600	1000	CỬA SỔ 1 CÁCH MỞ LẬT LÊN TRÊN, KHUNG NHÔM XINGFA, KÍNH TRONG SUỐT DÀY 10mm	3
TẦNG 2	S5	1250	800	1000	CỬA SỔ 1 CÁCH MỞ LẬT LÊN TRÊN, KHUNG NHÔM XINGFA, KÍNH TRONG SUỐT DÀY 10mm	2

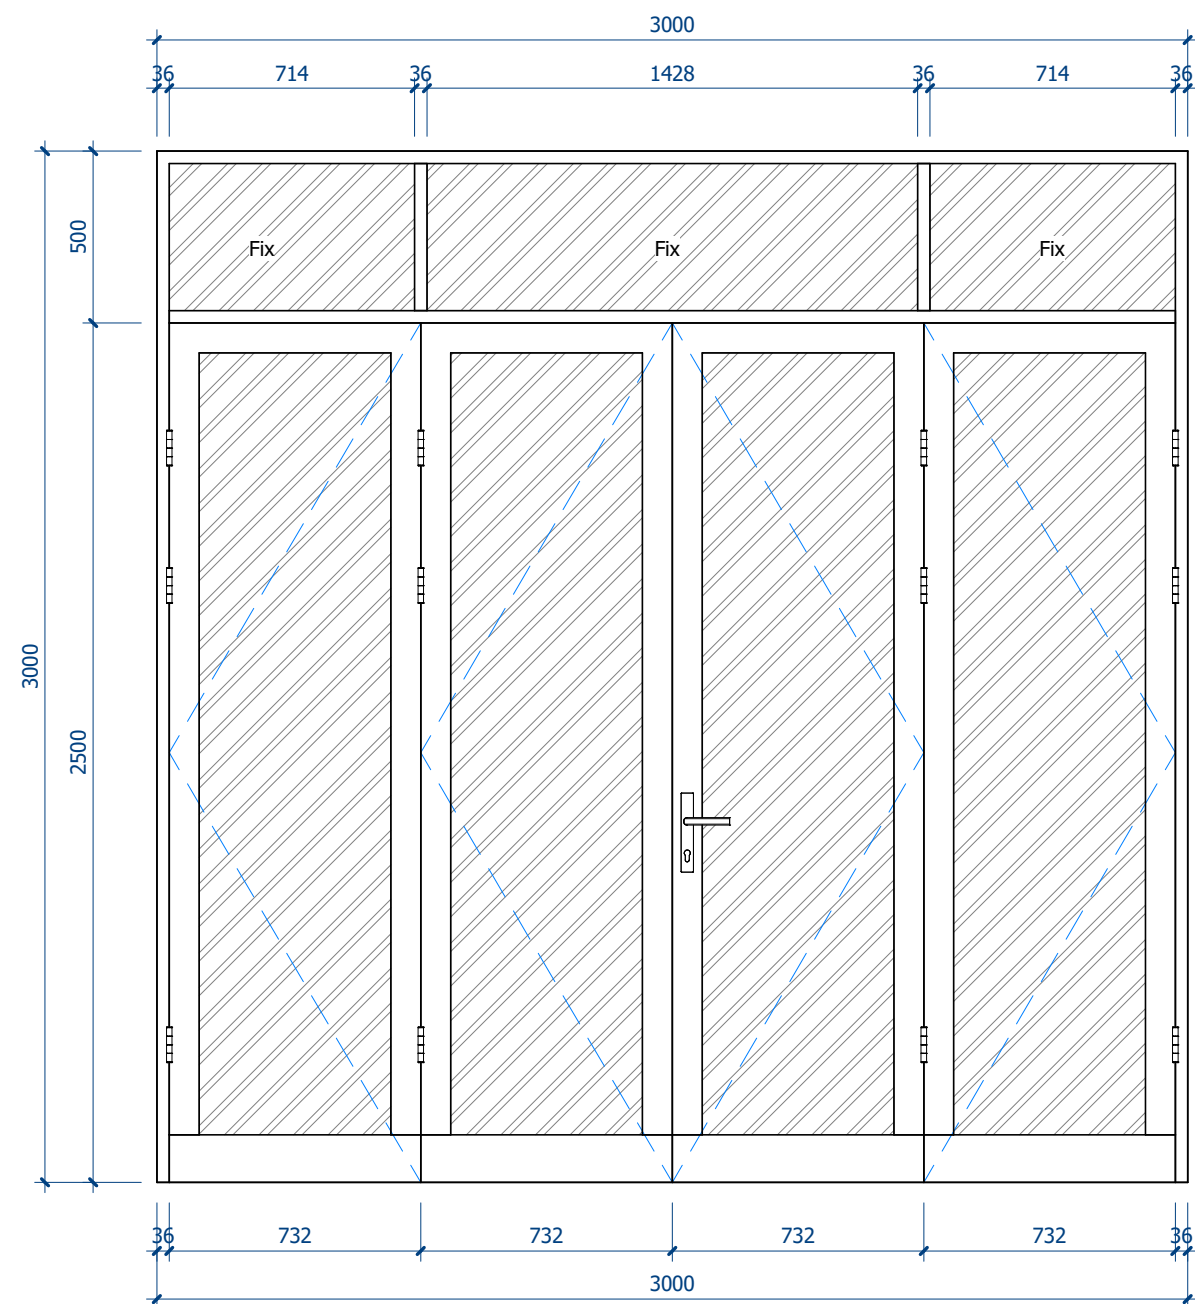



CỬA D1
1 : 20

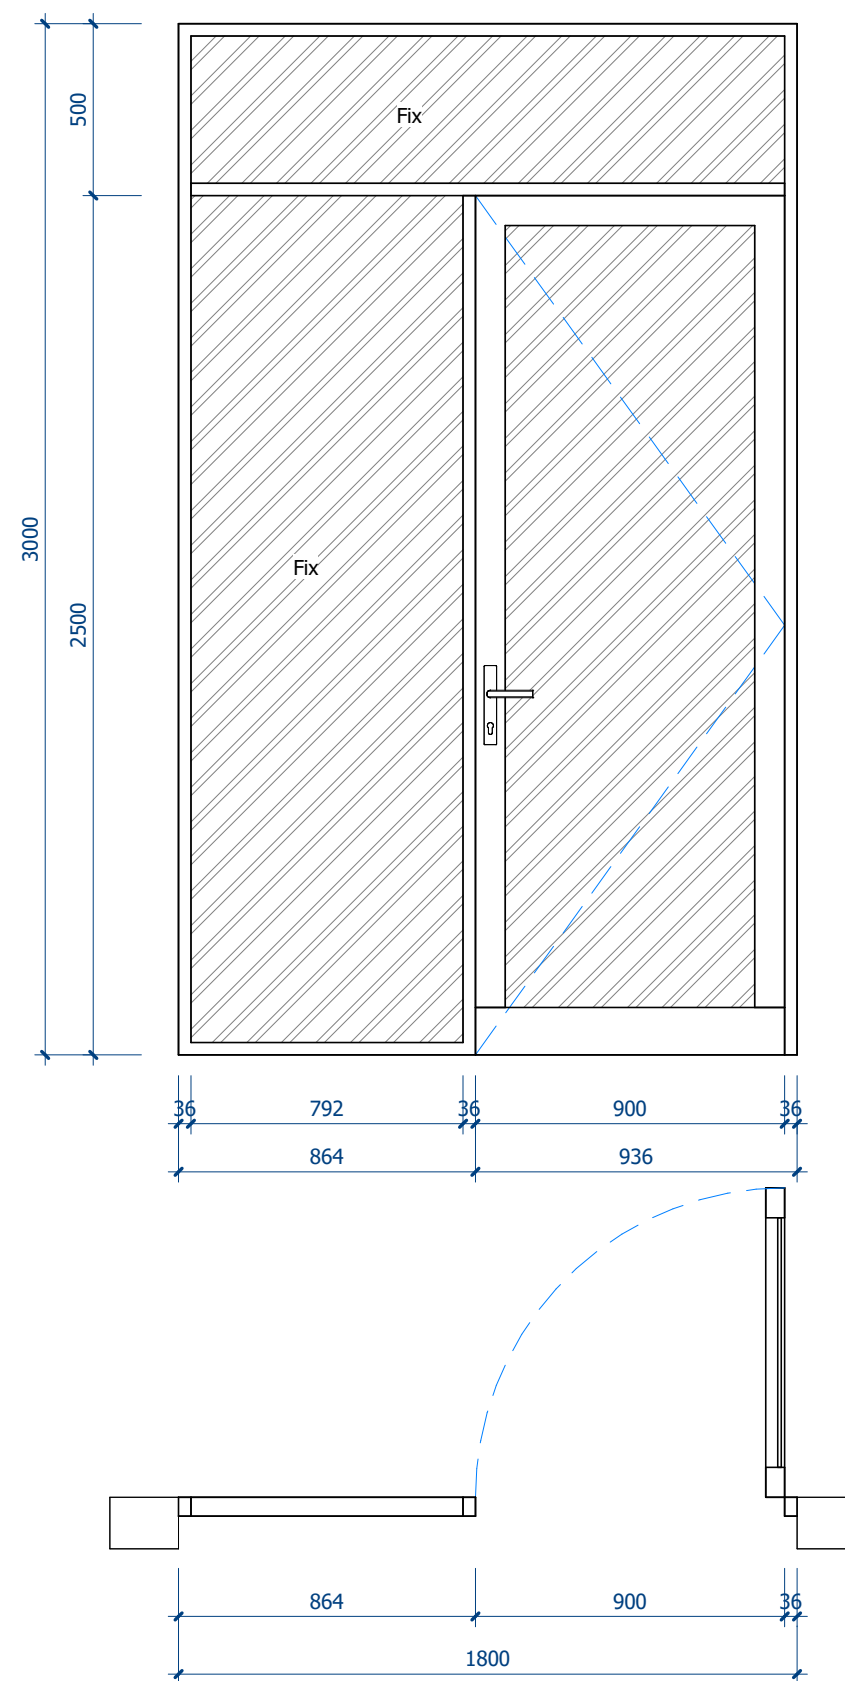



CỬA D2
1 : 20

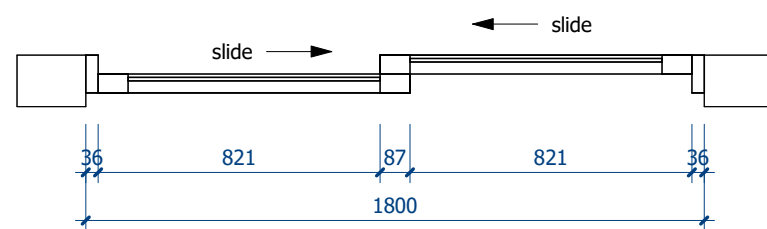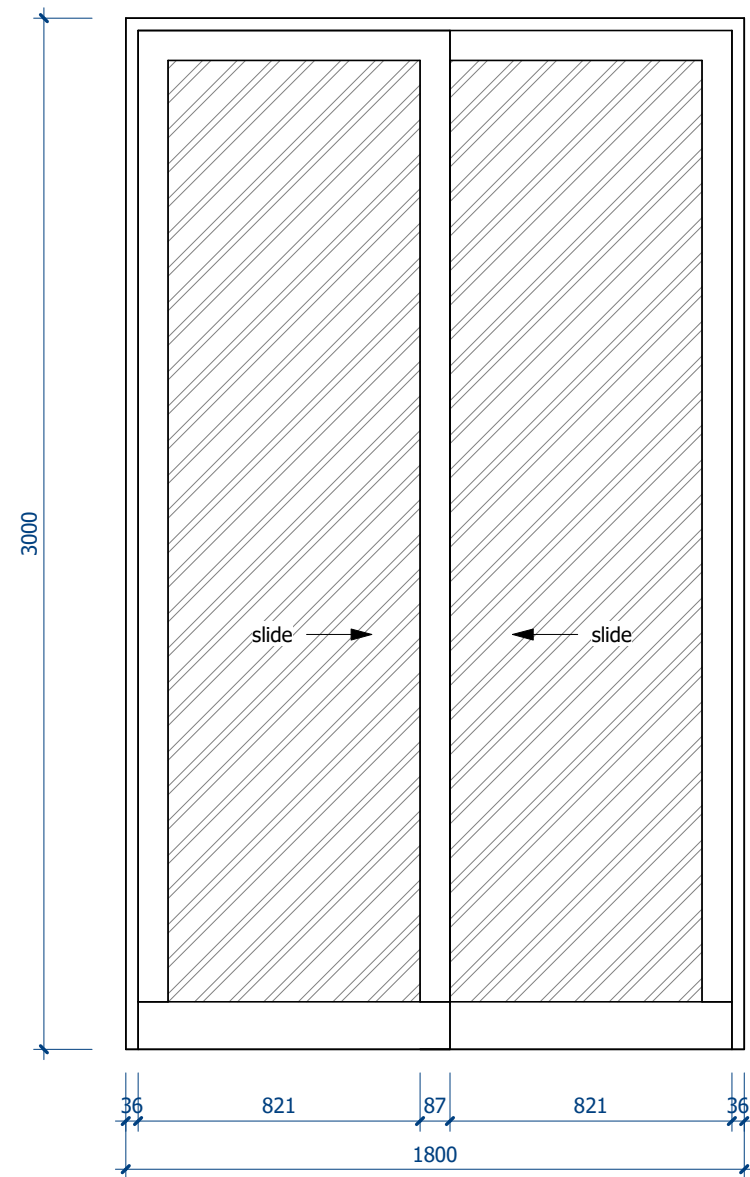



CỬA D3
1 : 20

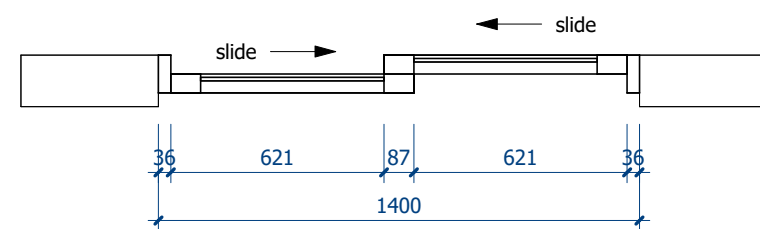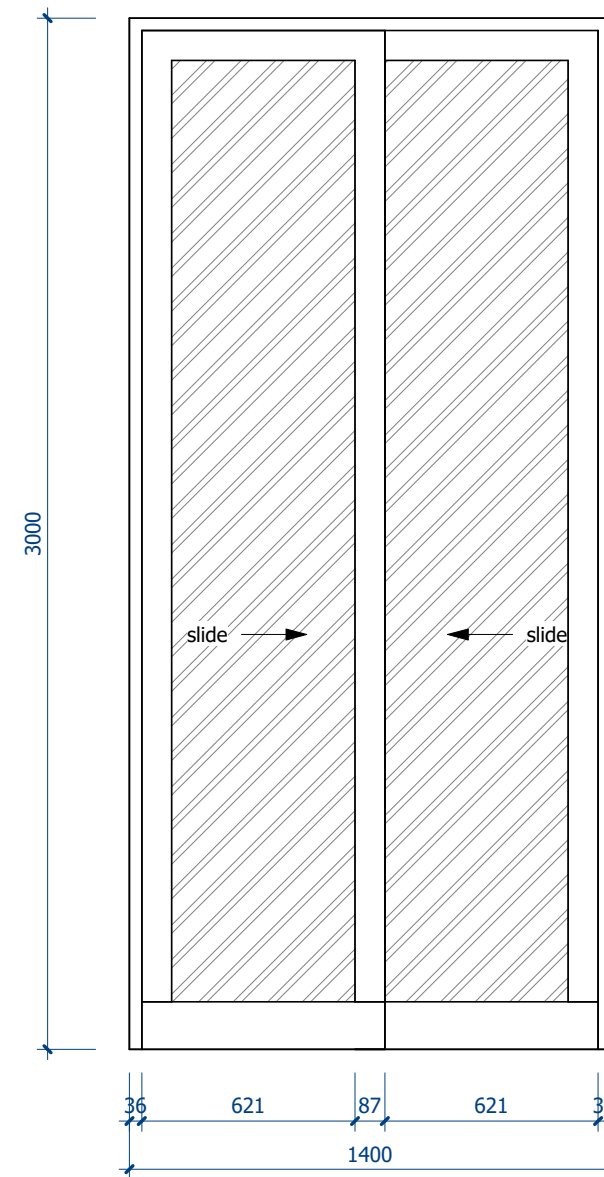



CỬA D4
1 : 20

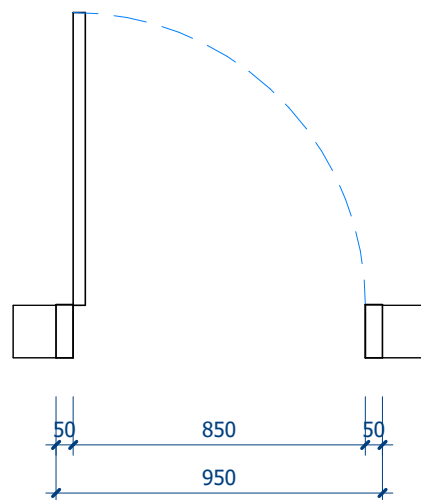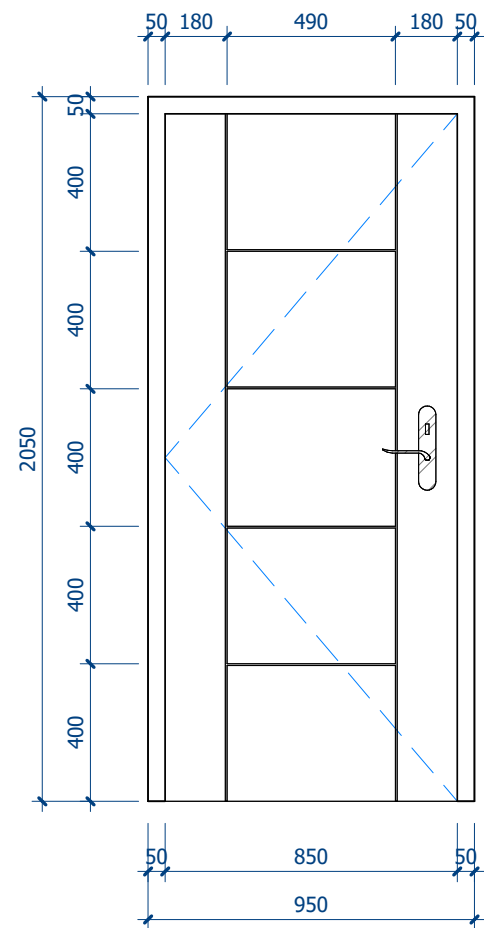



○ CỬA D5
1 : 20

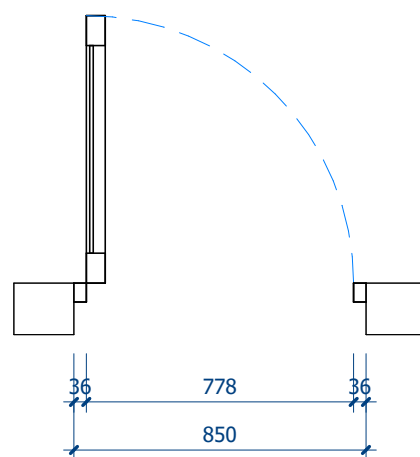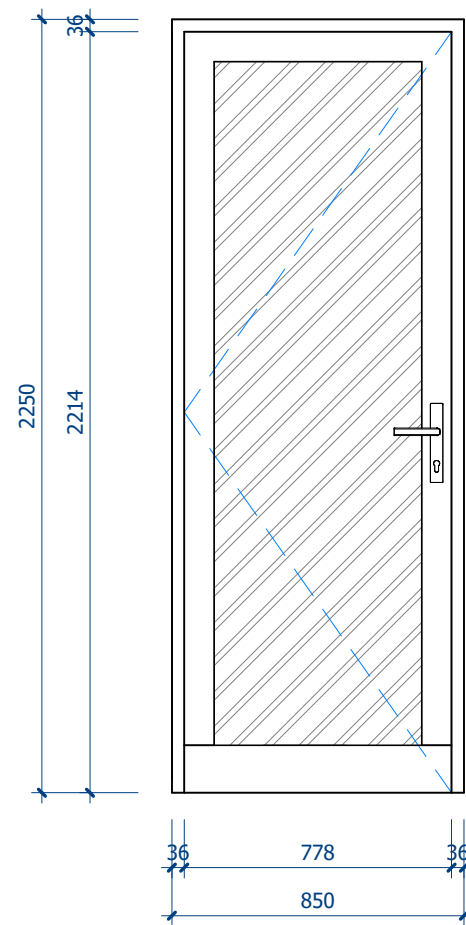



○ CỬA D6
1 : 20

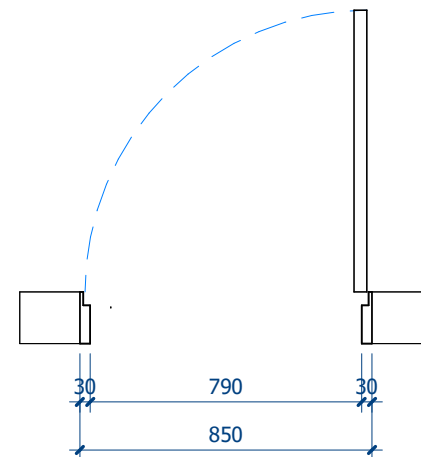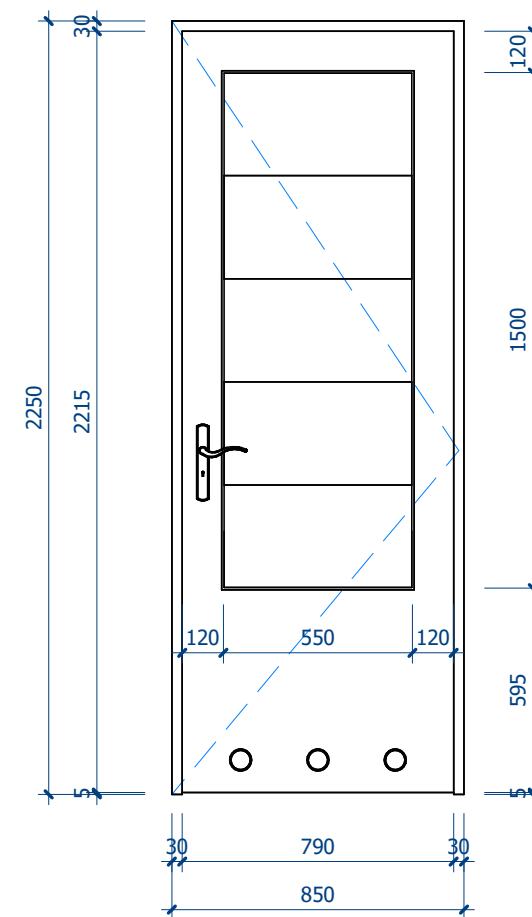


○ CỬA D7
1 : 20

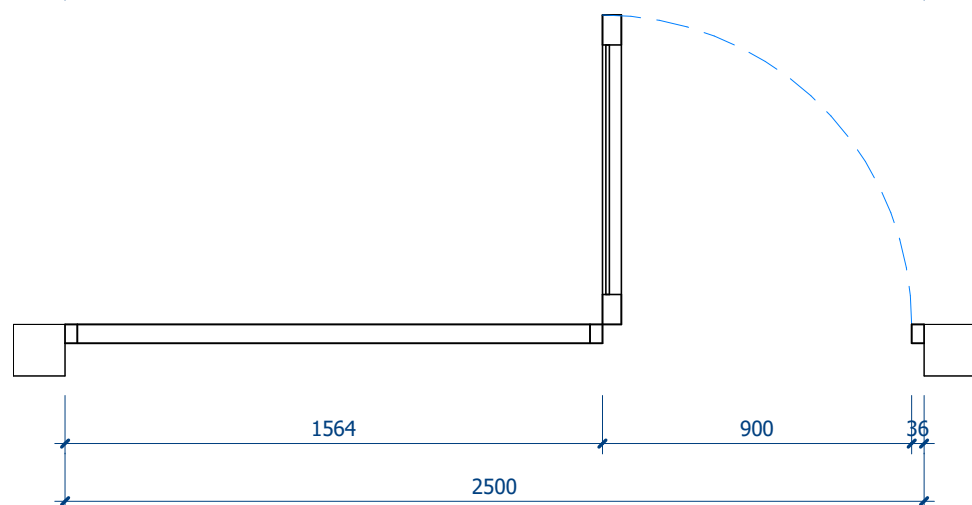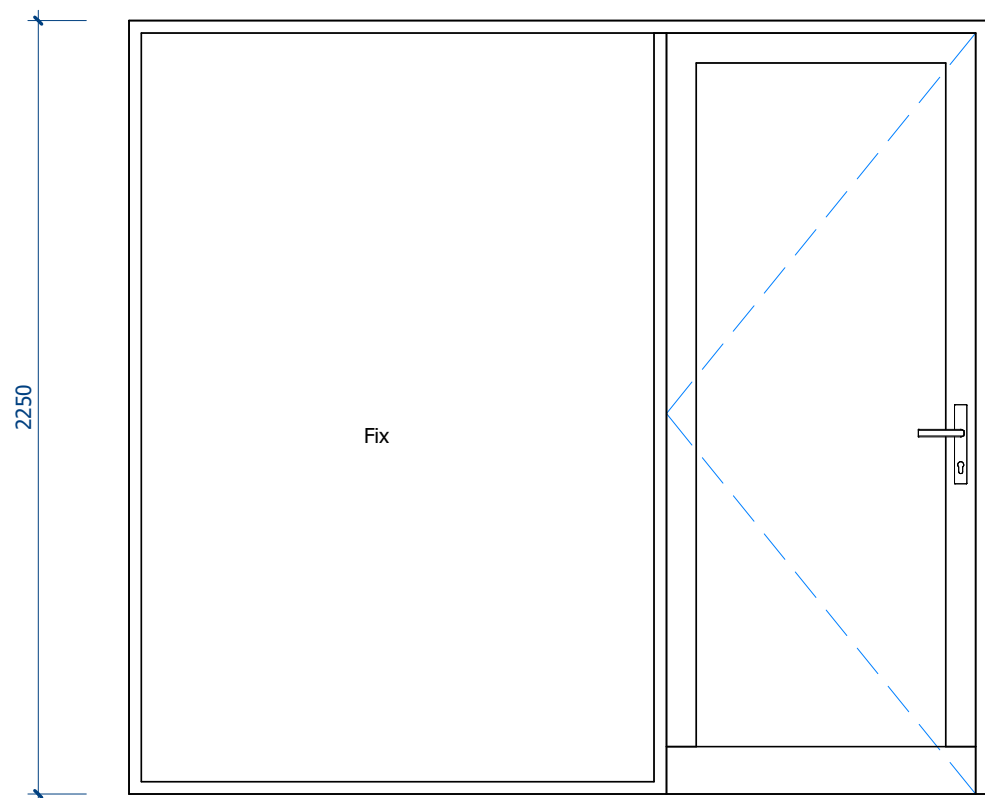


CỬA D8
1 : 20

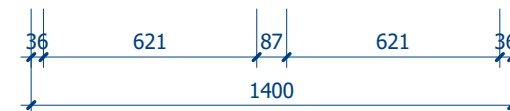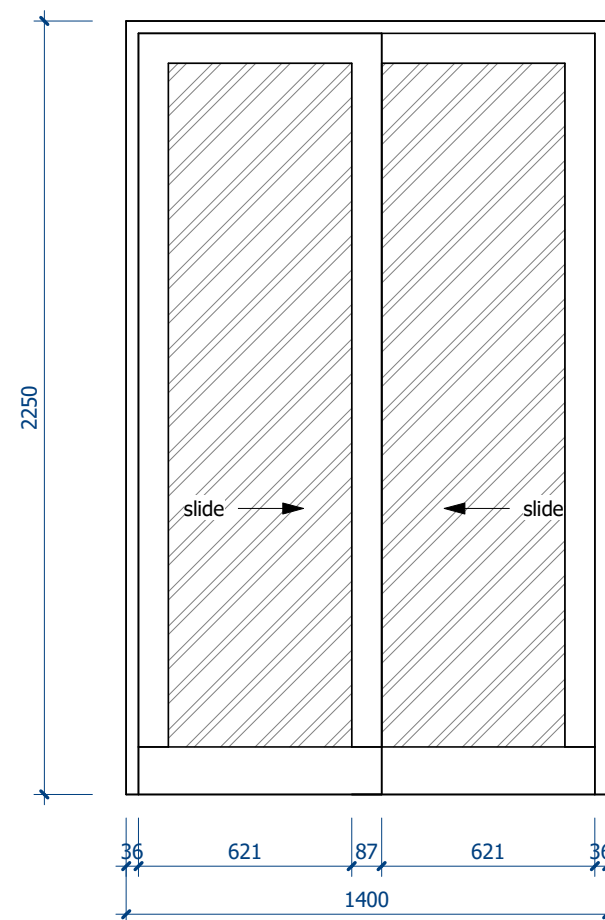



CỬA D9
1 : 20

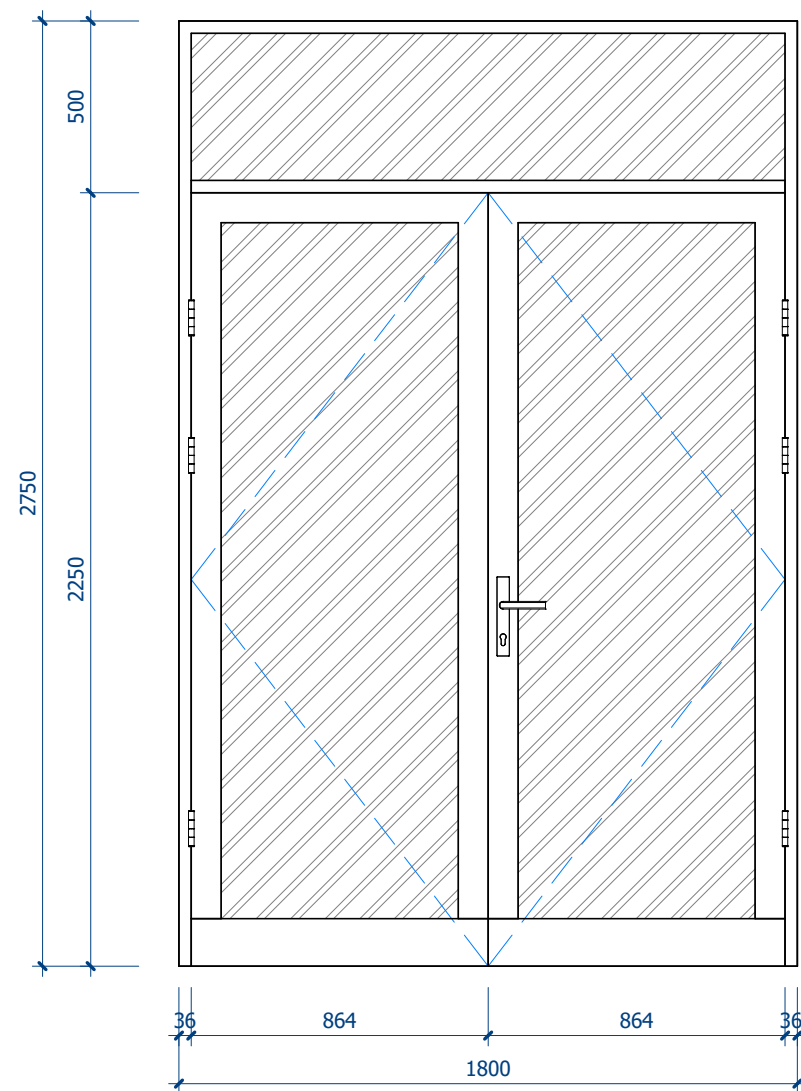



○ CỬA D10
1 : 20

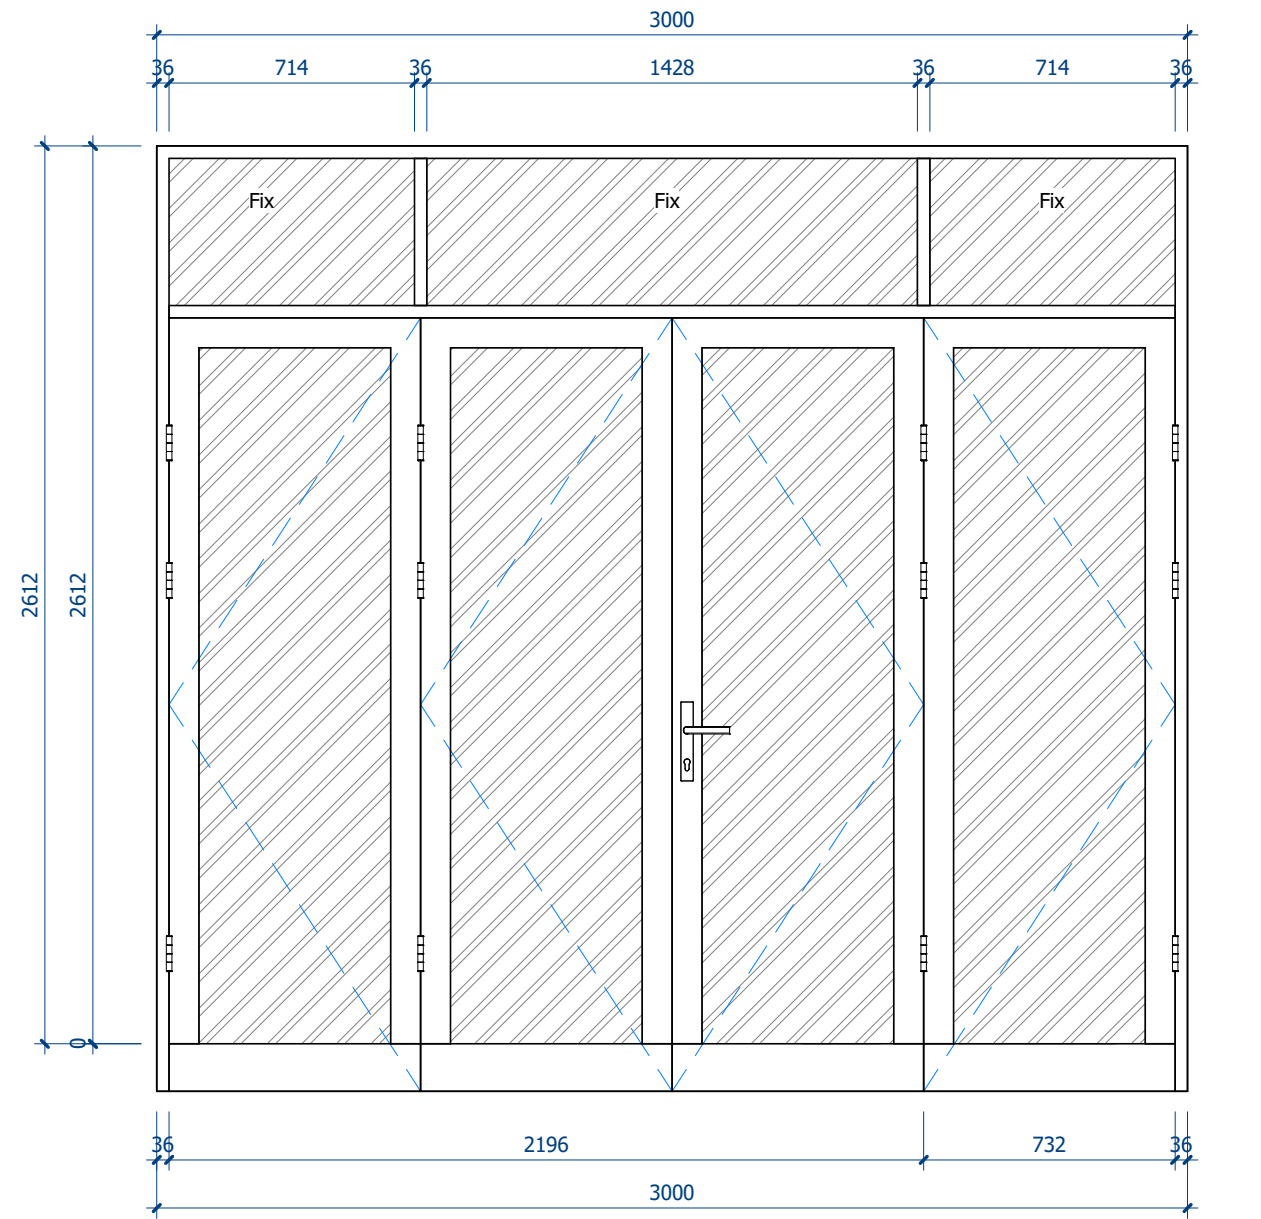



○ CỬA D11
1 : 20

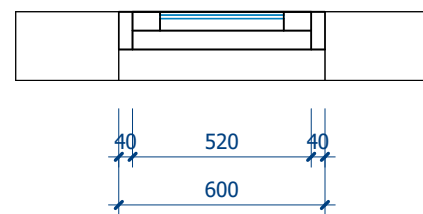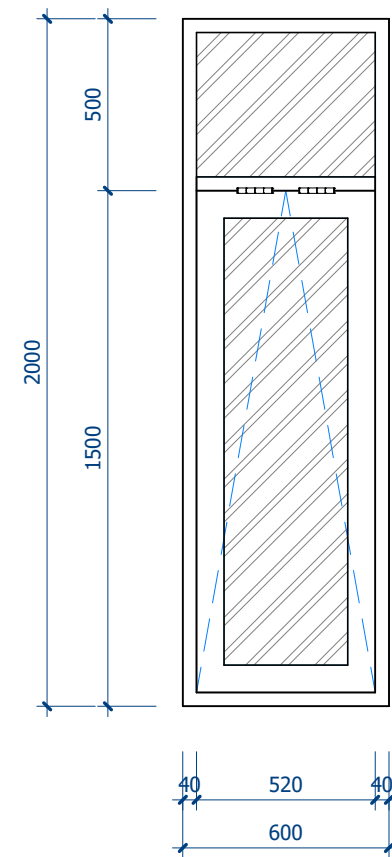



○ CỬA S1
1 : 20

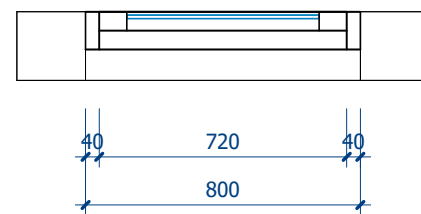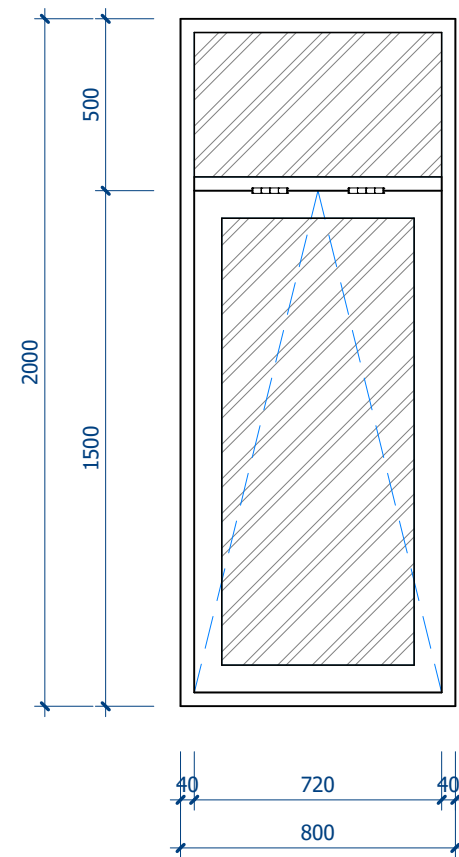



○ CỬA S2
1 : 20

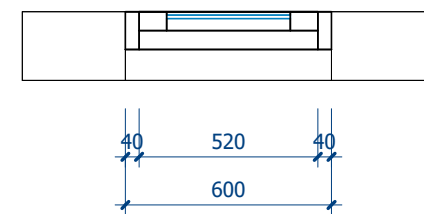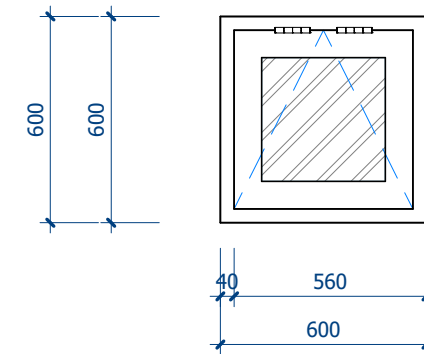



○ CỬA S3
1 : 20

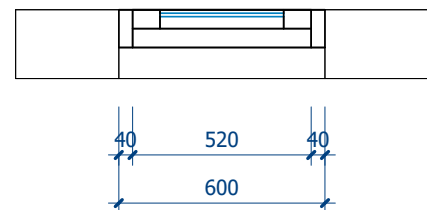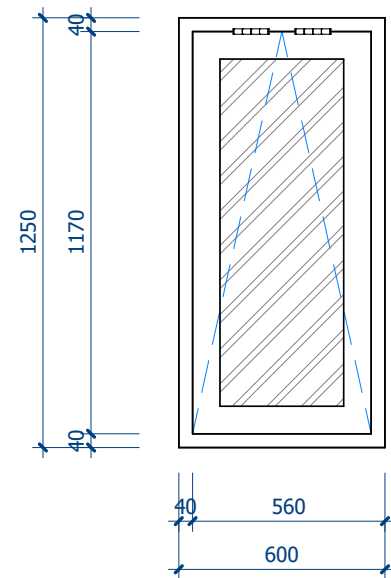

○ CỬA S4
1 : 20

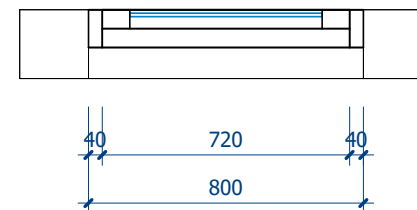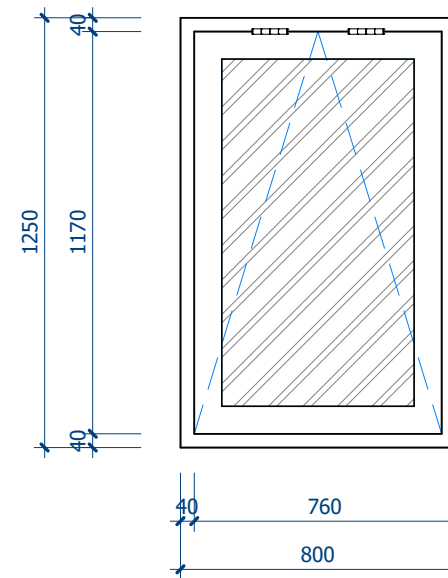


○ CỬA S5
1 : 20

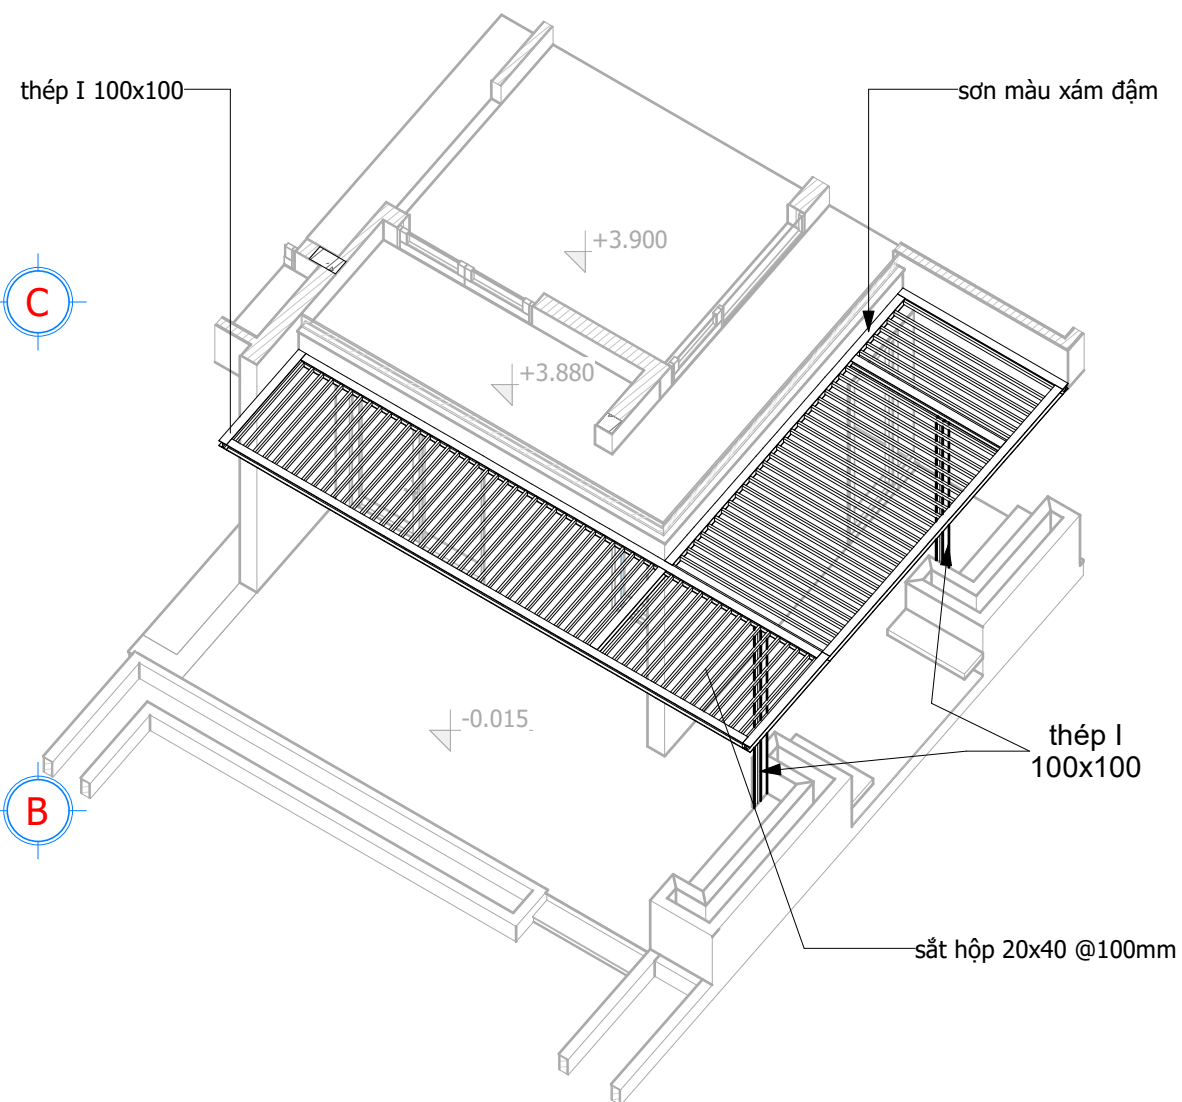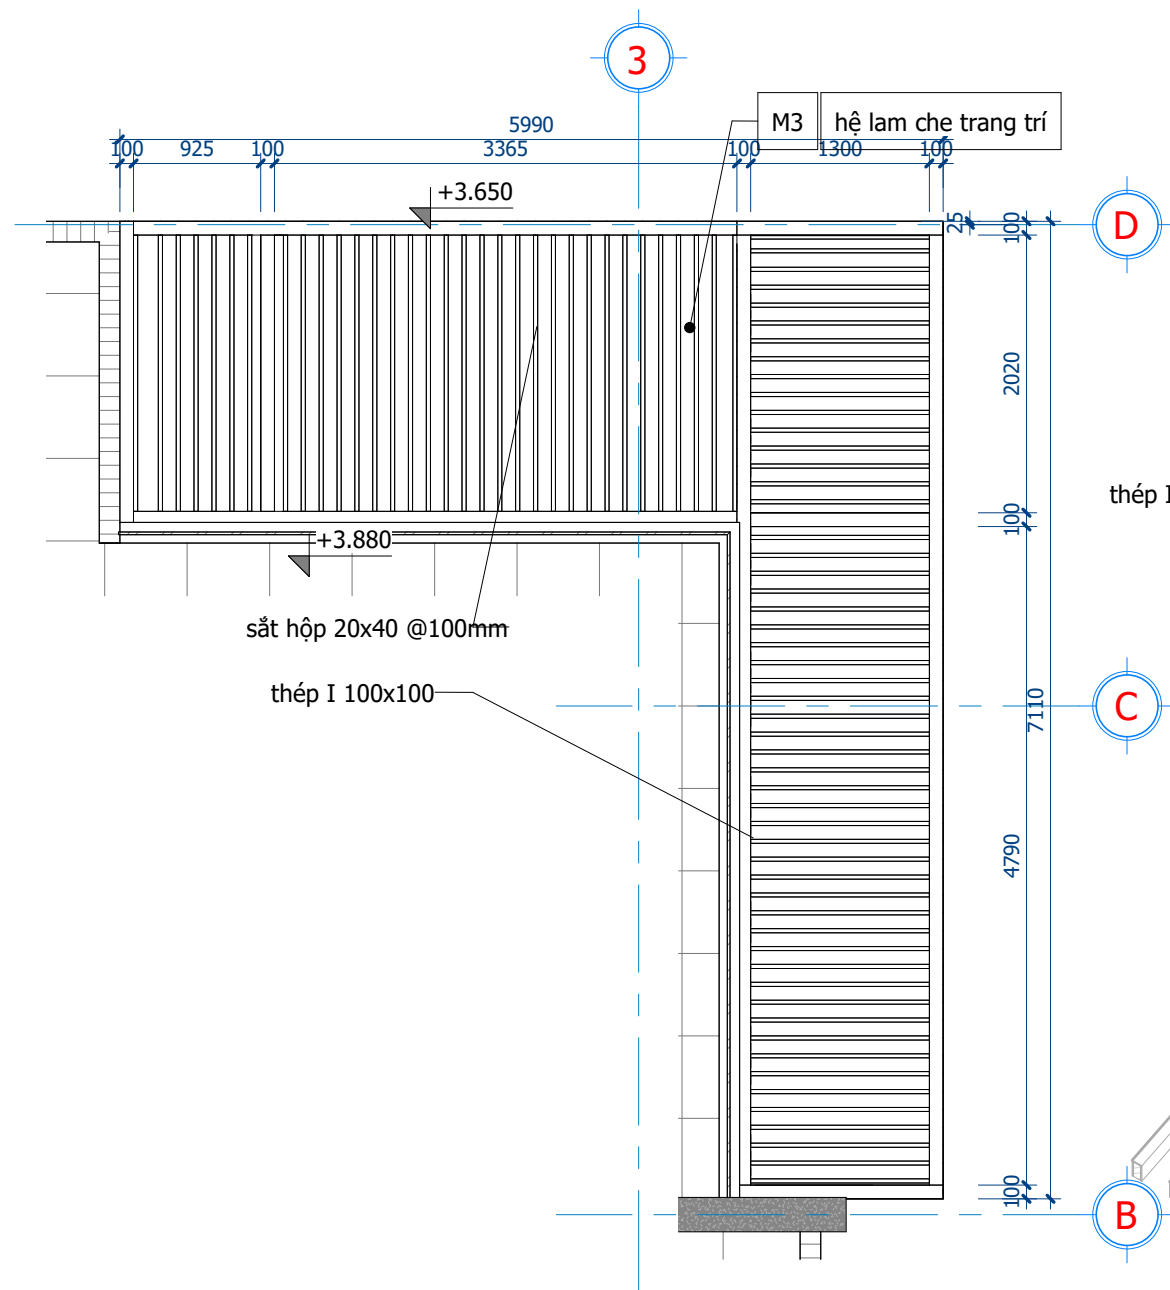


1 CHI TIẾT LAM TRANG TRÍ
1 : 50


2 PHỐI CẢNH HỆ LAM TRANG TRÍ

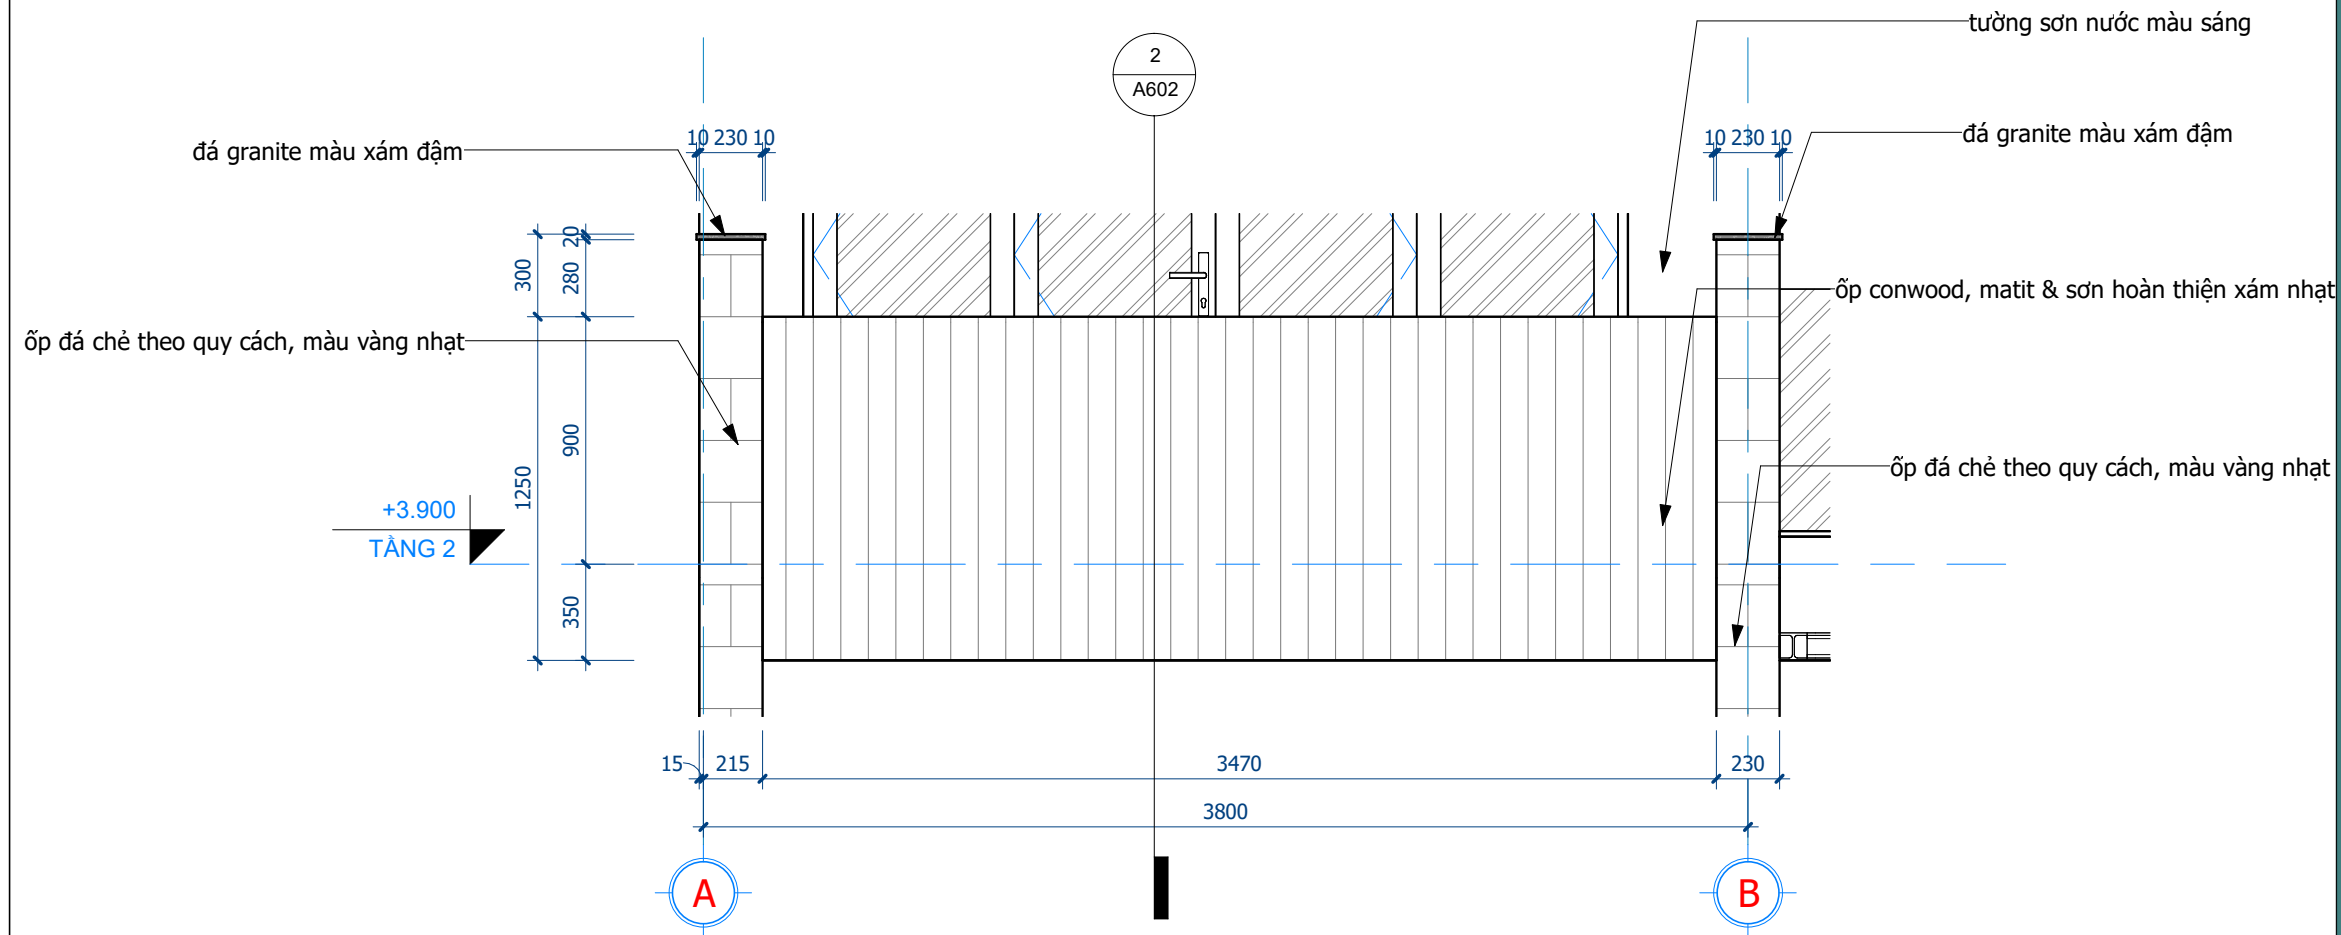


1 CHI TIẾT LAN CAN 01
1 : 25

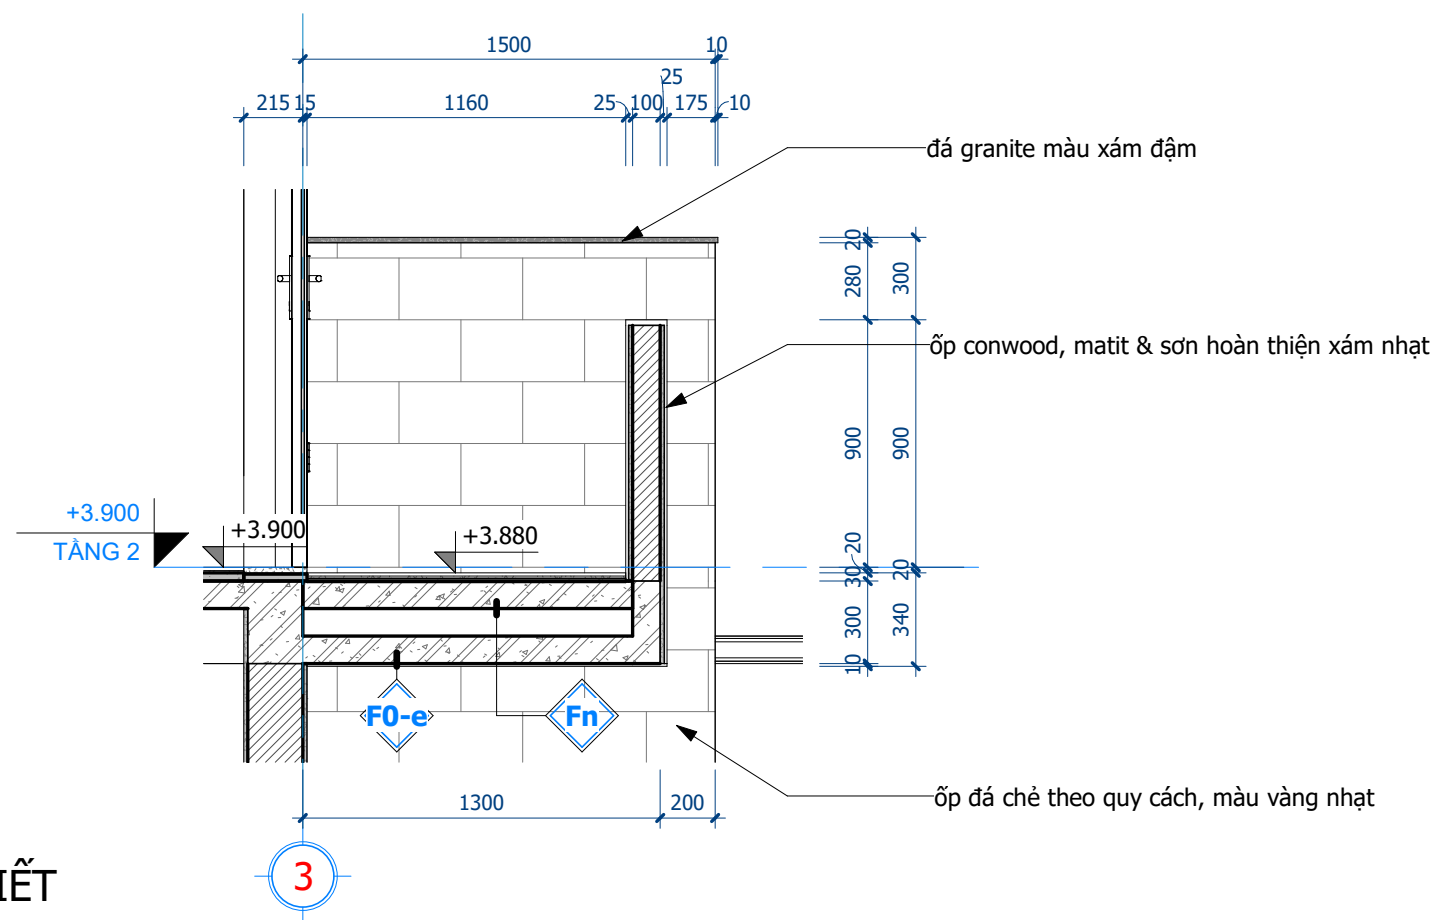


2 LAN CAN 01- MẶT CẮT CHI TIẾT
1 : 25

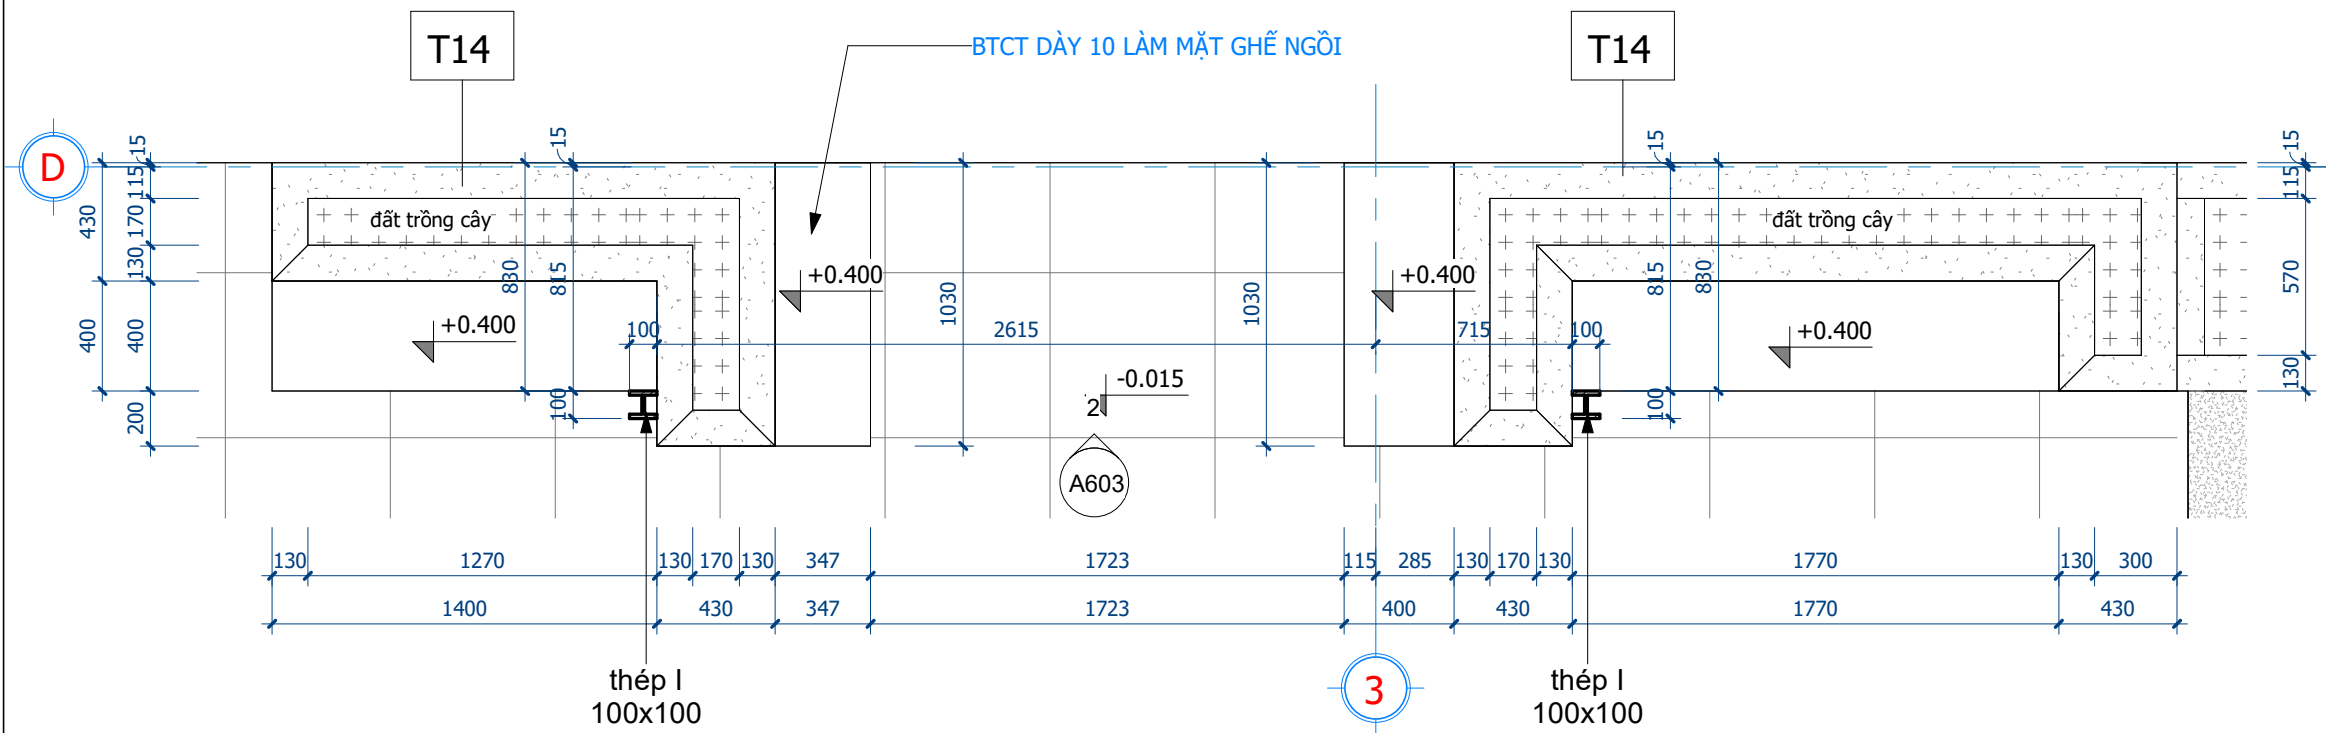

1 BỒN HOA- MẶT BẰNG CHI TIẾT
1 : 25

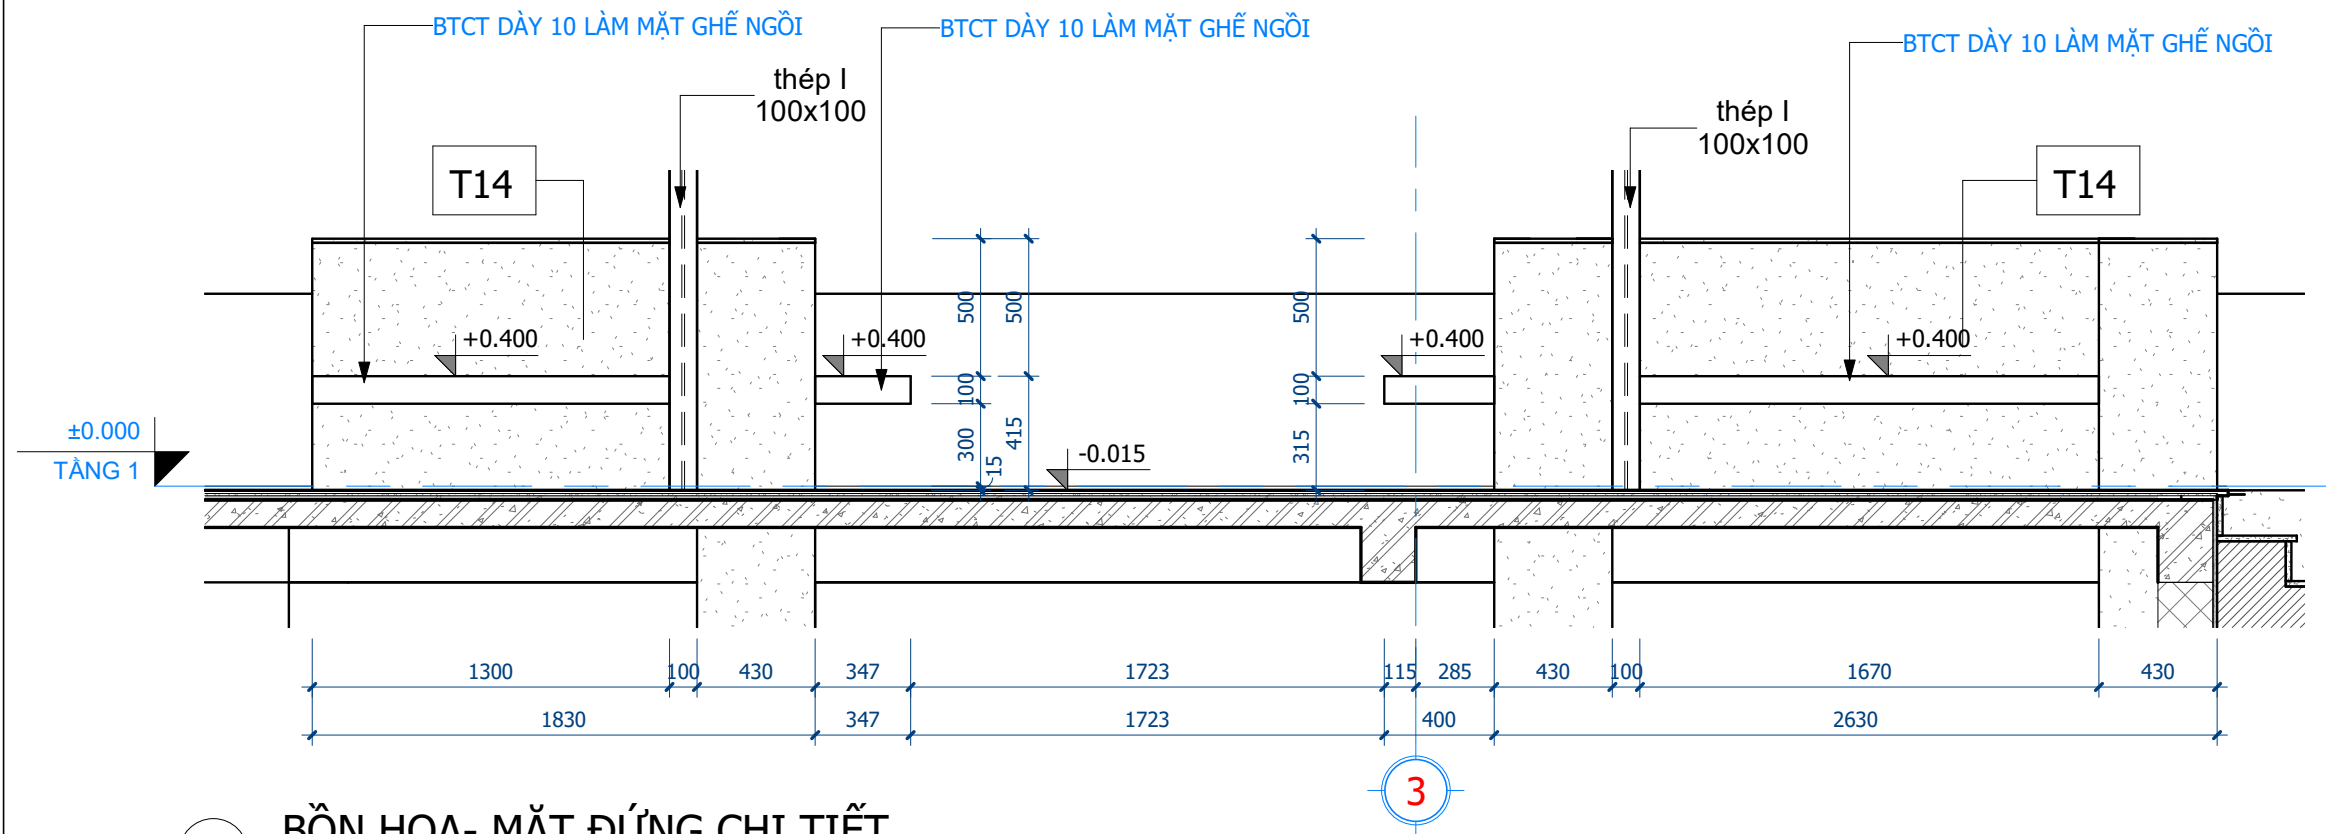

2 BỒN HOA- MẶT ĐỨNG CHI TIẾT
1 : 25

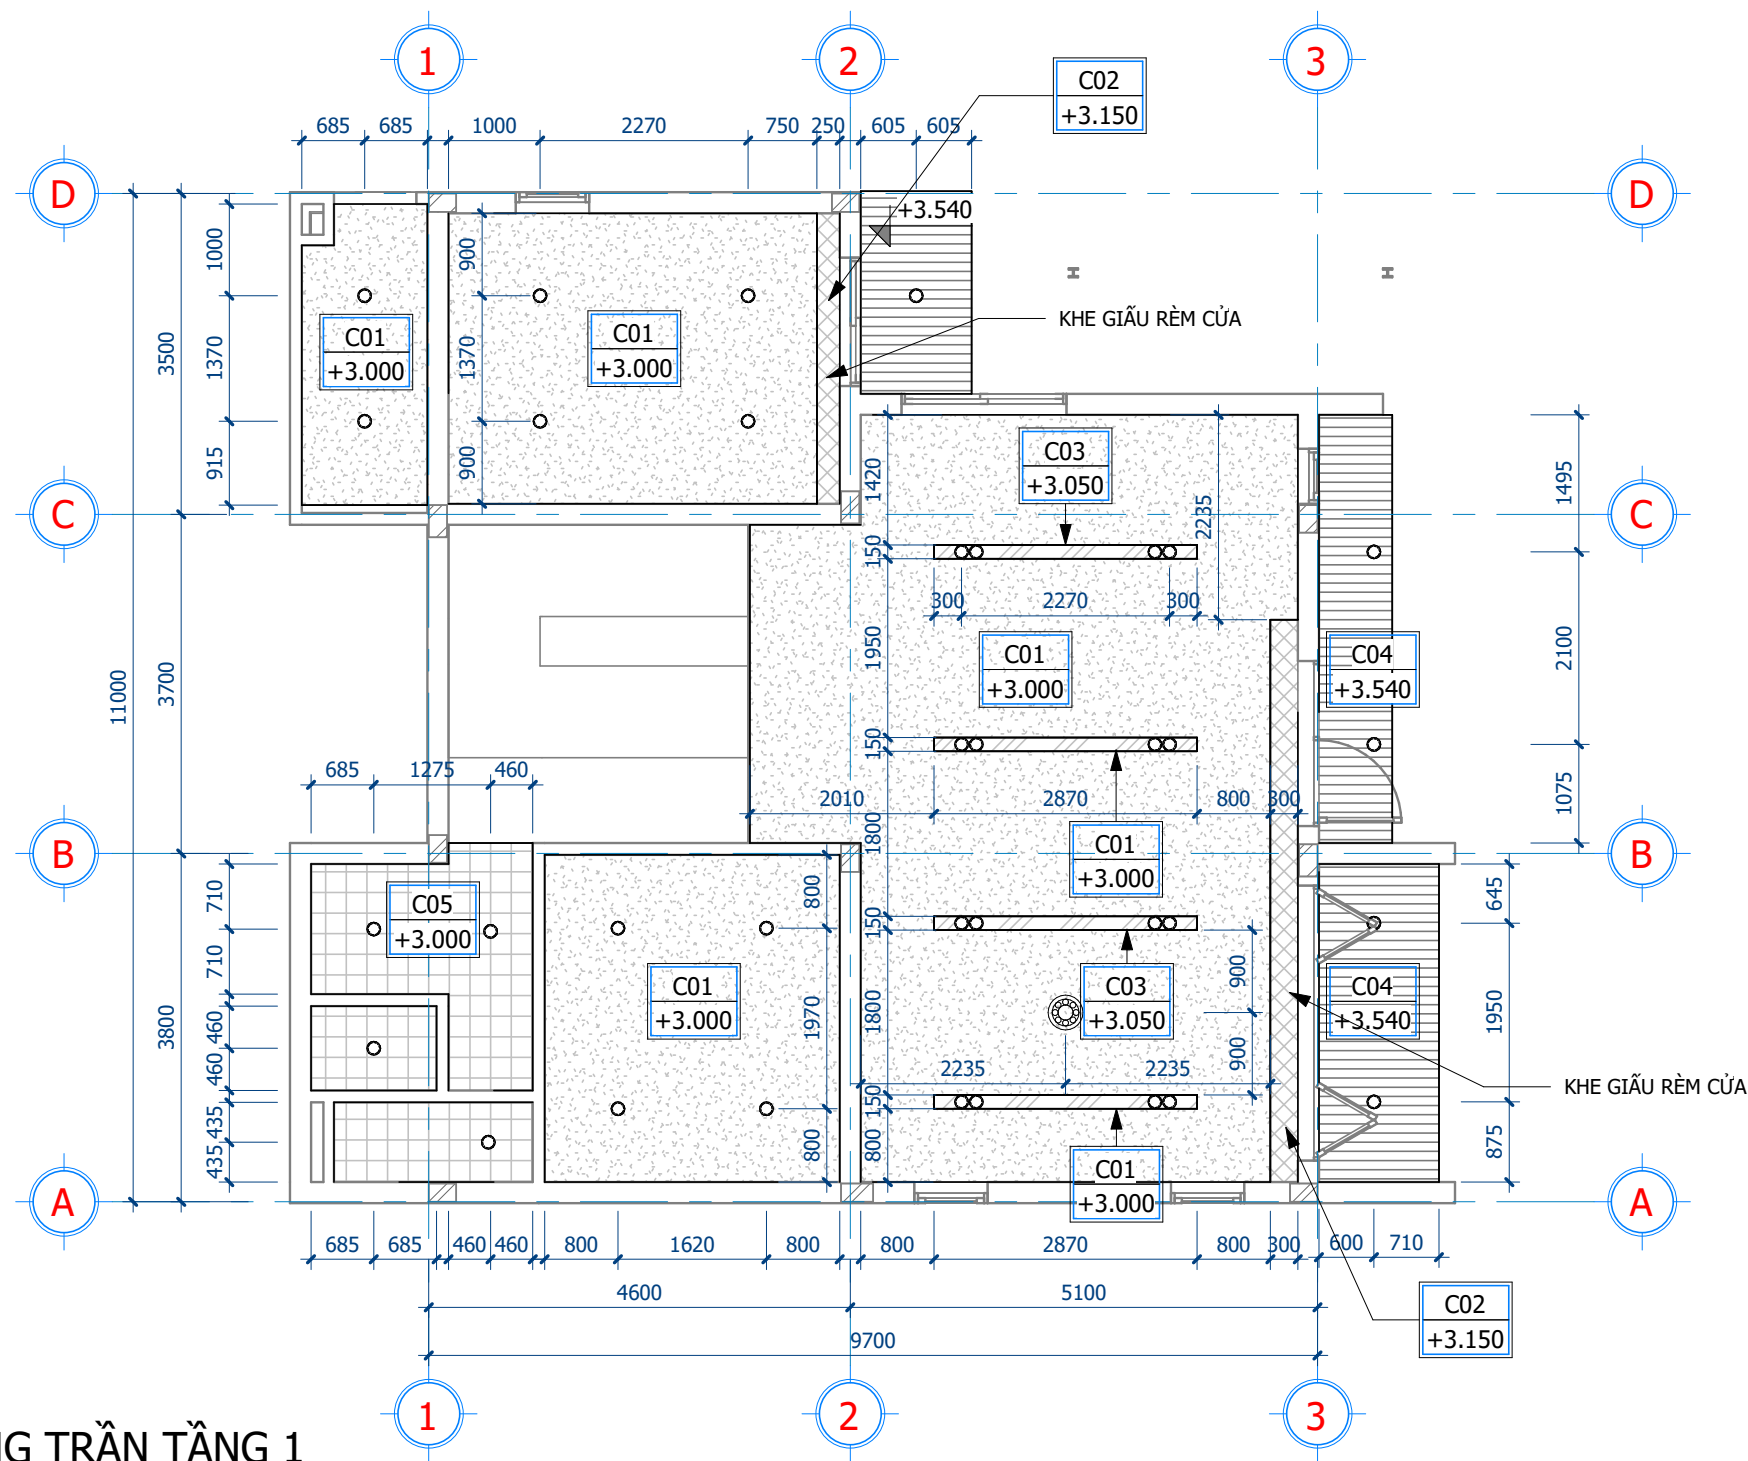

1 MẶT BẰNG TRẦN TẦNG 1
1 : 75


THỐNG KÊ TRẦN TẦNG 1

LOẠI TRẦN	DIỆN TÍCH	MÔ TẢ CHUNG
C01	69.14 m ²	TRẦN THẠCH CAO PHẪNG, MÀU TRẮNG
C02	2.63 m ²	TRẦN THẠCH CAO PHẪNG TẠI VỊ TRÍ KHE RÈM
C03	1.72 m ²	TRẦN THẠCH CAO PHẪNG, MÀU ĐEN
C04	10.96 m ²	TRẦN CONWOOD, ĐÓNG SẮT MẶT DƯỚI SÀN BAN CÔNG
C05	7.76 m ²	TRẦN THẠCH CAO CHỐNG ẨM, ĐÓNG PHẪNG, MÀU TRẮNG

*LƯU Ý: DIỆN TÍCH THỐNG KÊ TRẦN CHƯA BAO GỒM TẮM ĐỨNG TẠI CÁC KHE ẨM TRẦN

DIỄN GIẢI KÝ HIỆU ĐÈN TRẦN

	ĐÈN LED TRÒN ĐƠN D=150mm, ÁNH SÁNG TRẮNG, PHẪNG MẶT TRẦN
	ĐÈN LED TRÒN ĐÔI D=150mm, ÁNH SÁNG TRẮNG, PHẪNG MẶT TRẦN
	ĐÈN CHÙM TRANG TRÍ (THEO MẪU CHỈ ĐỊNH)
	ĐÈN LED DÂY ẨM TRẦN

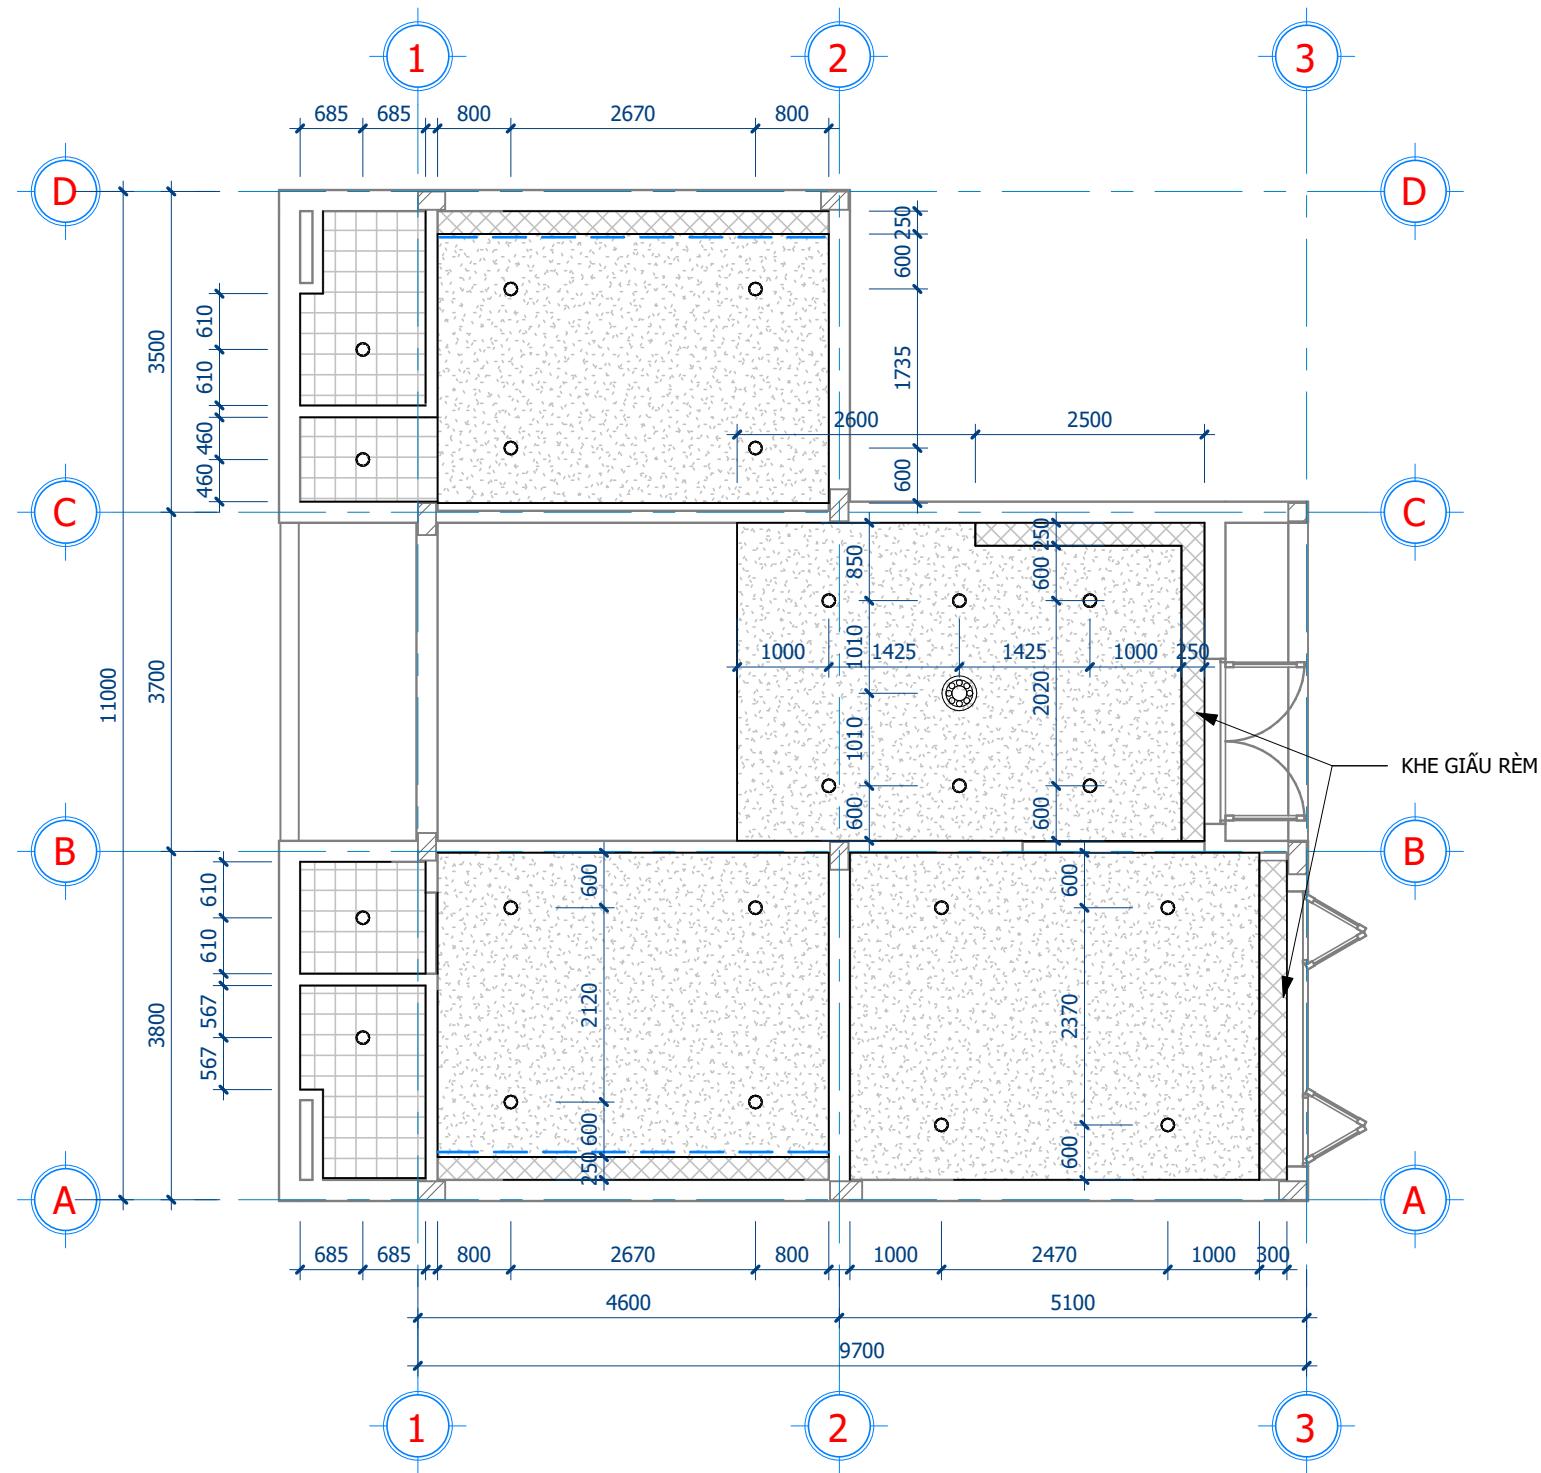

1 MẶT BẰNG TRẦN TẦNG 2
1 : 75

THỐNG KÊ TRẦN TẦNG 2


LOẠI TRẦN	DIỆN TÍCH	MÔ TẢ CHUNG
C01	58.93 m ²	TRẦN THẠCH CAO PHẪNG, MÀU TRẮNG
C02	4.64 m ²	TRẦN THẠCH CAO PHẪNG TẠI VỊ TRÍ KHE RÈM
C05	8.37 m ²	TRẦN THẠCH CAO CHỐNG ẨM, ĐÓNG PHẪNG, MÀU TRẮNG

*LƯU Ý: DIỆN TÍCH THỐNG KÊ TRẦN CHƯA BAO GỒM TẮM ĐÚNG TẠI CÁC KHE ẨM TRẦN


DIỄN GIẢI KÝ HIỆU ĐÈN TRẦN

	ĐÈN LED TRÒN ĐƠN D=150mm, ÁNH SÁNG TRẮNG, PHẪNG MẶT TRẦN
	ĐÈN LED TRÒN ĐÔI D=150mm, ÁNH SÁNG TRẮNG, PHẪNG MẶT TRẦN
	ĐÈN CHÙM TRANG TRÍ (THEO MẪU CHỈ ĐỊNH)
	ĐÈN LED DÂY ẨM TRẦN


KIẾN TRÚC
A702
01/02/22

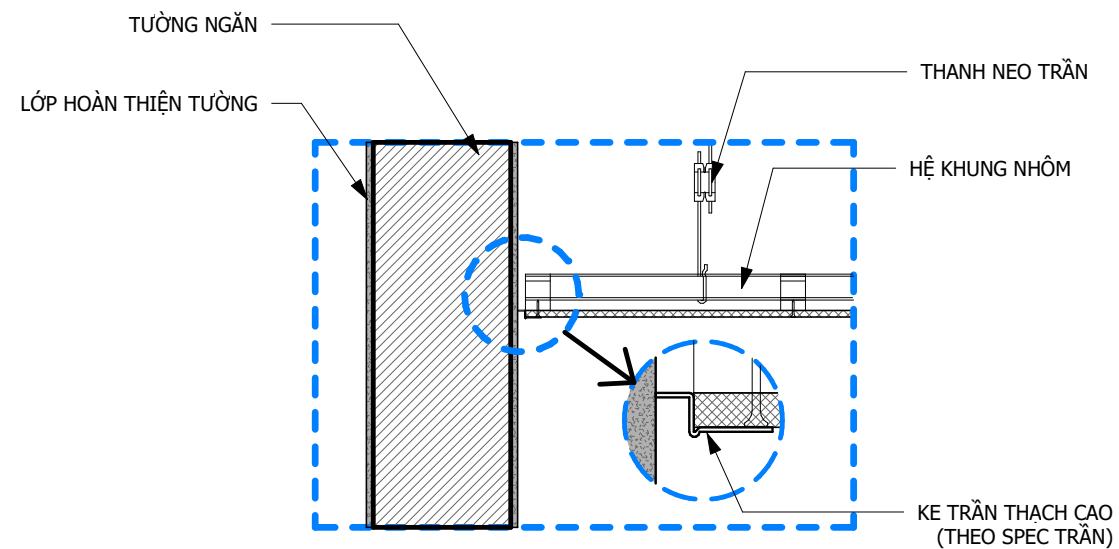


CT TRẦN TẠI VỊ TRÍ TIẾP GIÁP TƯỜNG

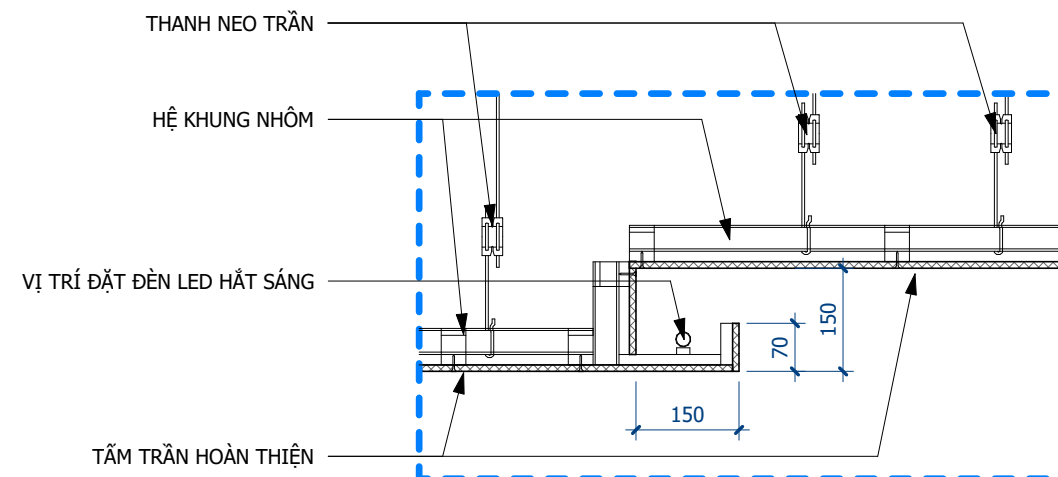


CT TRẦN TẠI VỊ TRÍ KHE HẮT SÁNG TRẦN PHẪNG

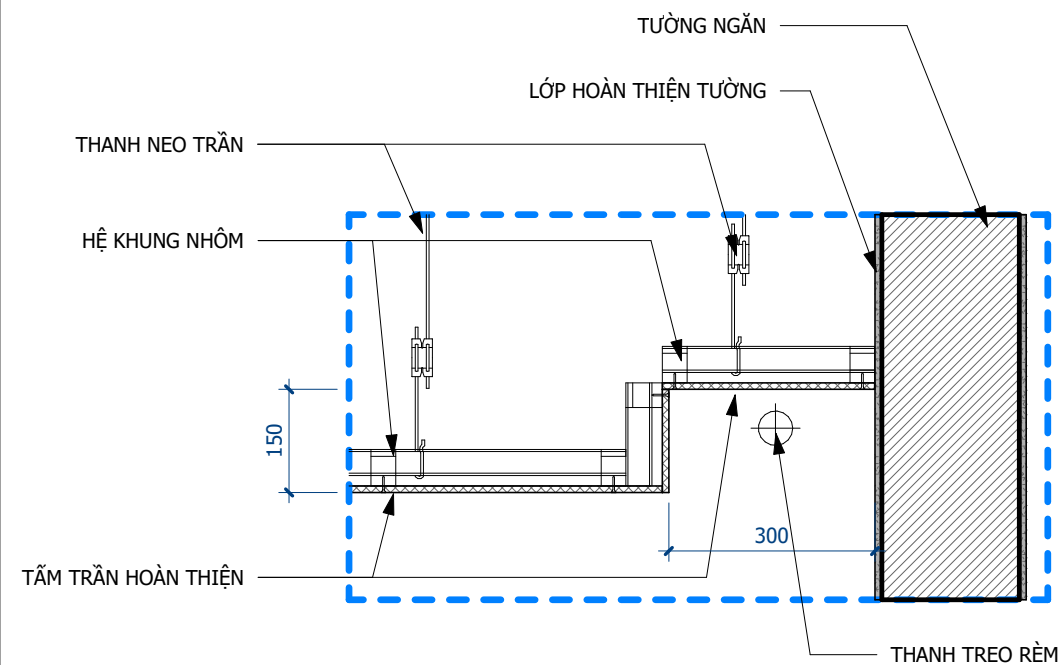


CT TRẦN TẠI VỊ TRÍ KHE GIẤU THANH RÈM

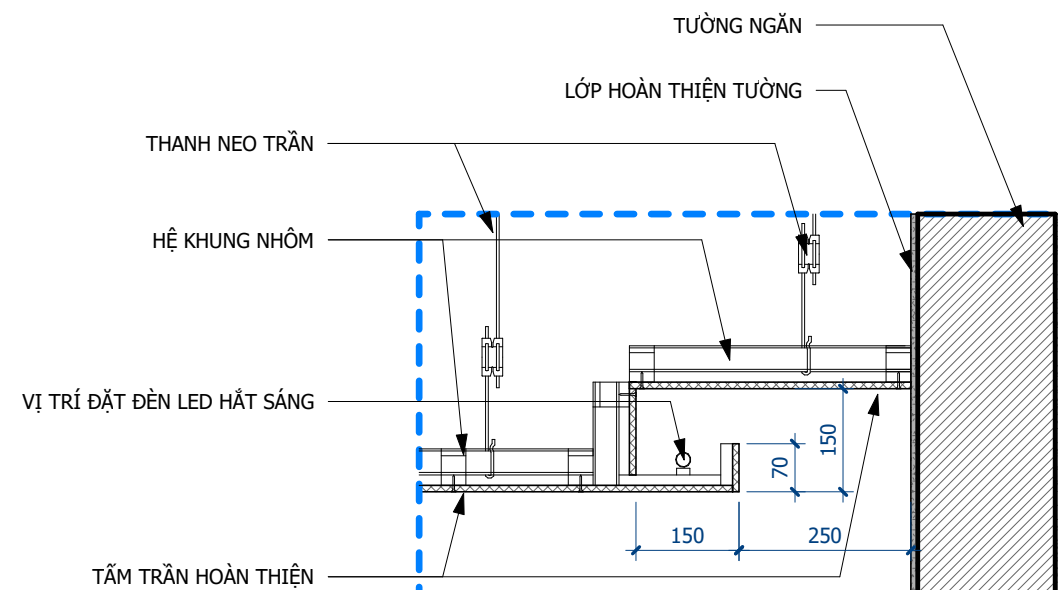


CT TRẦN TẠI VỊ TRÍ KHE HẮT SÁNG TIẾP GIÁP TƯỜNG

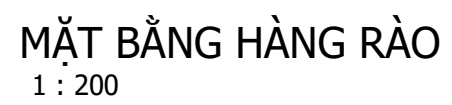


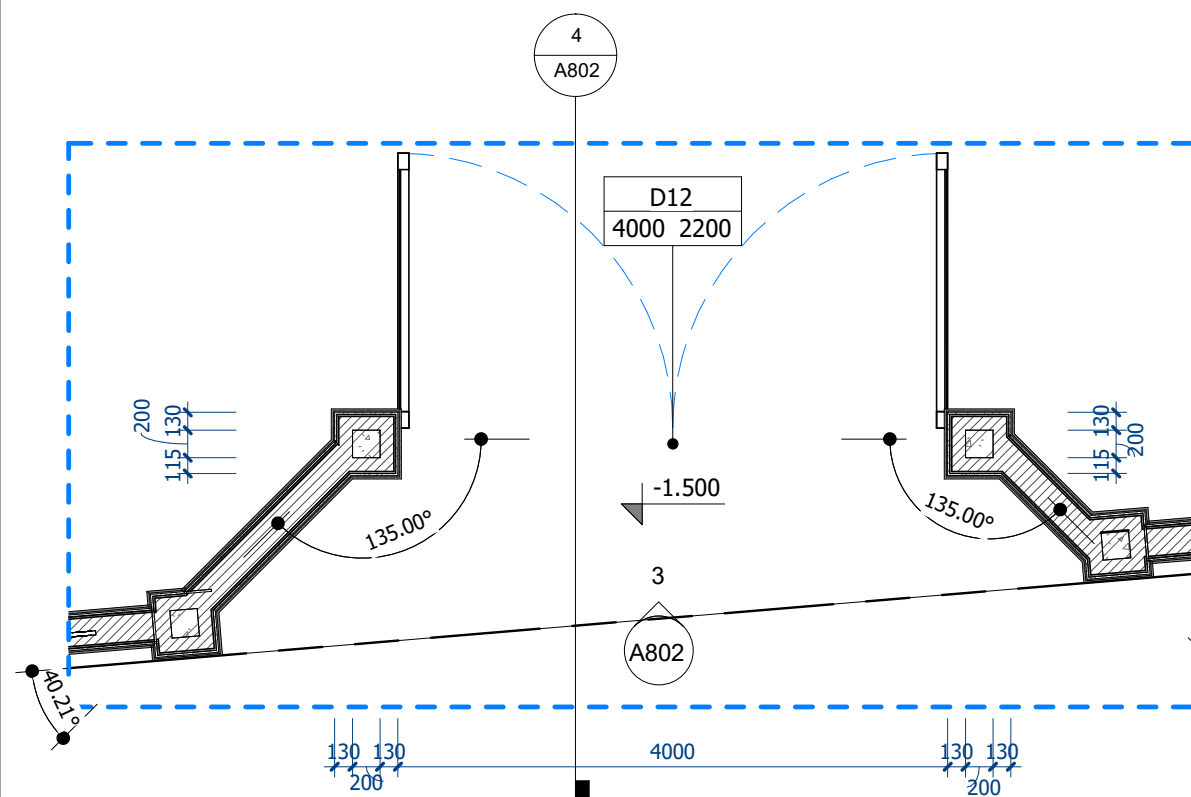


1 MẶT BẰNG CỔNG CHÍNH
1 : 50

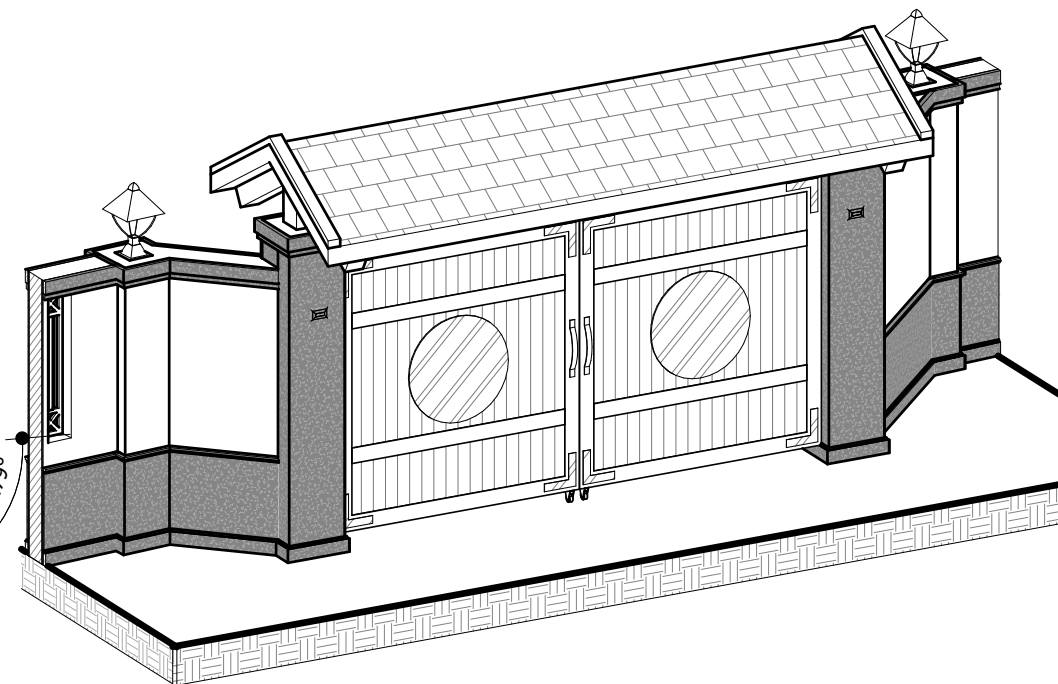


2 PHỐI CẢNH CỔNG CHÍNH

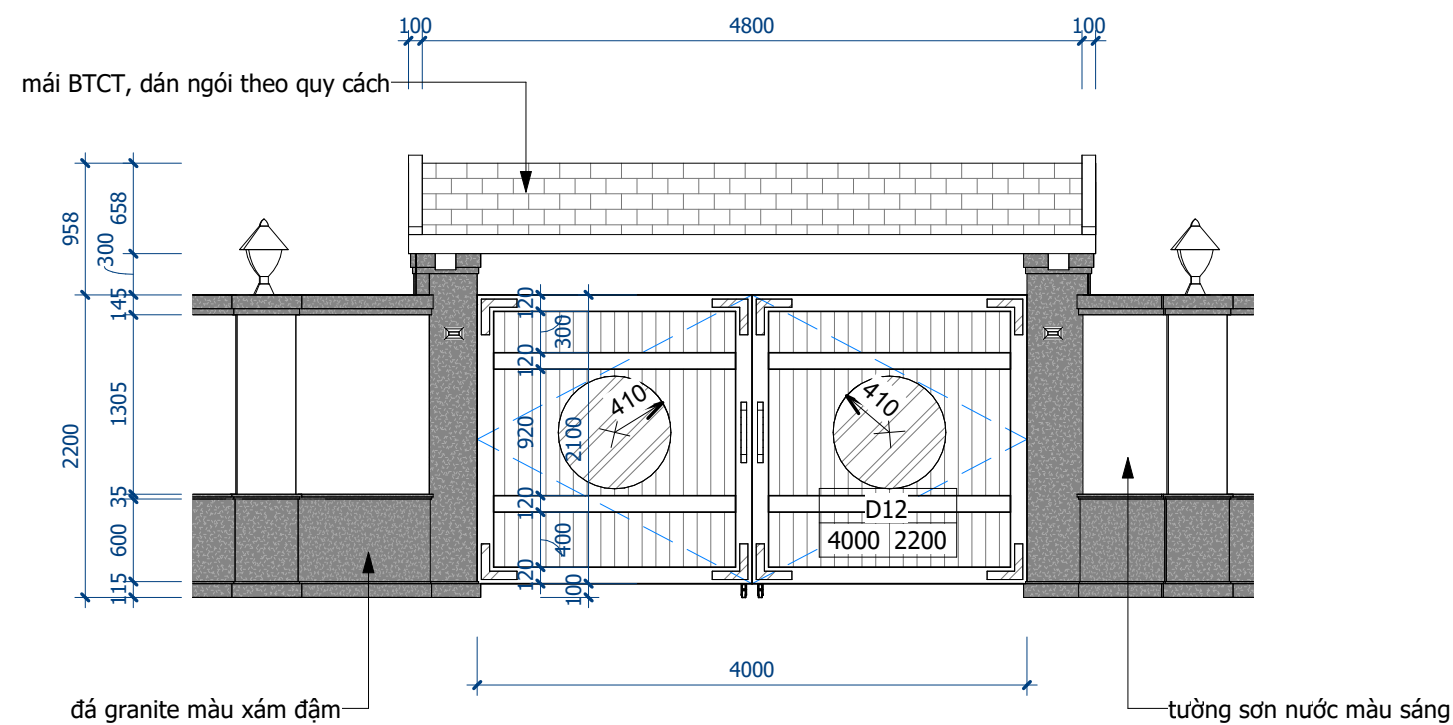


3 MẶT ĐỨNG CỔNG CHÍNH
1 : 50

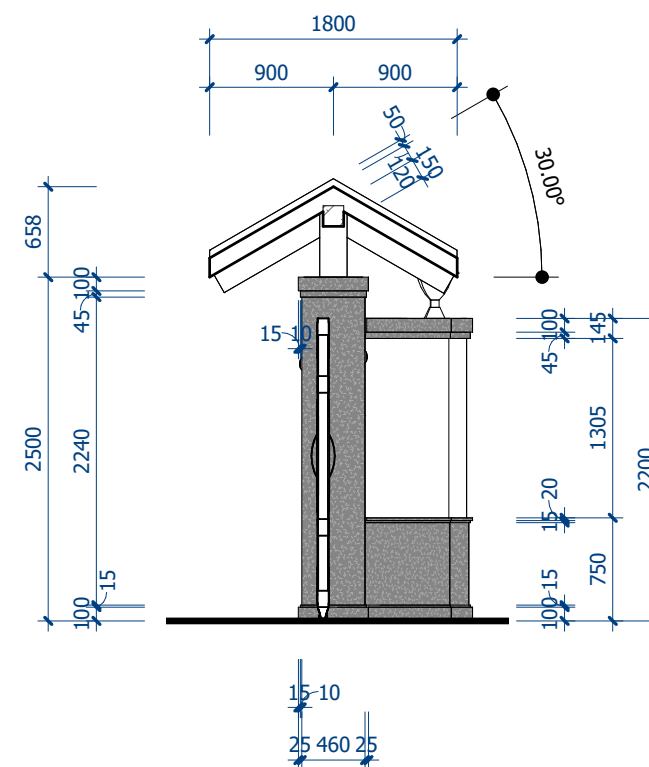


4 MC CỔNG CHÍNH
1 : 50

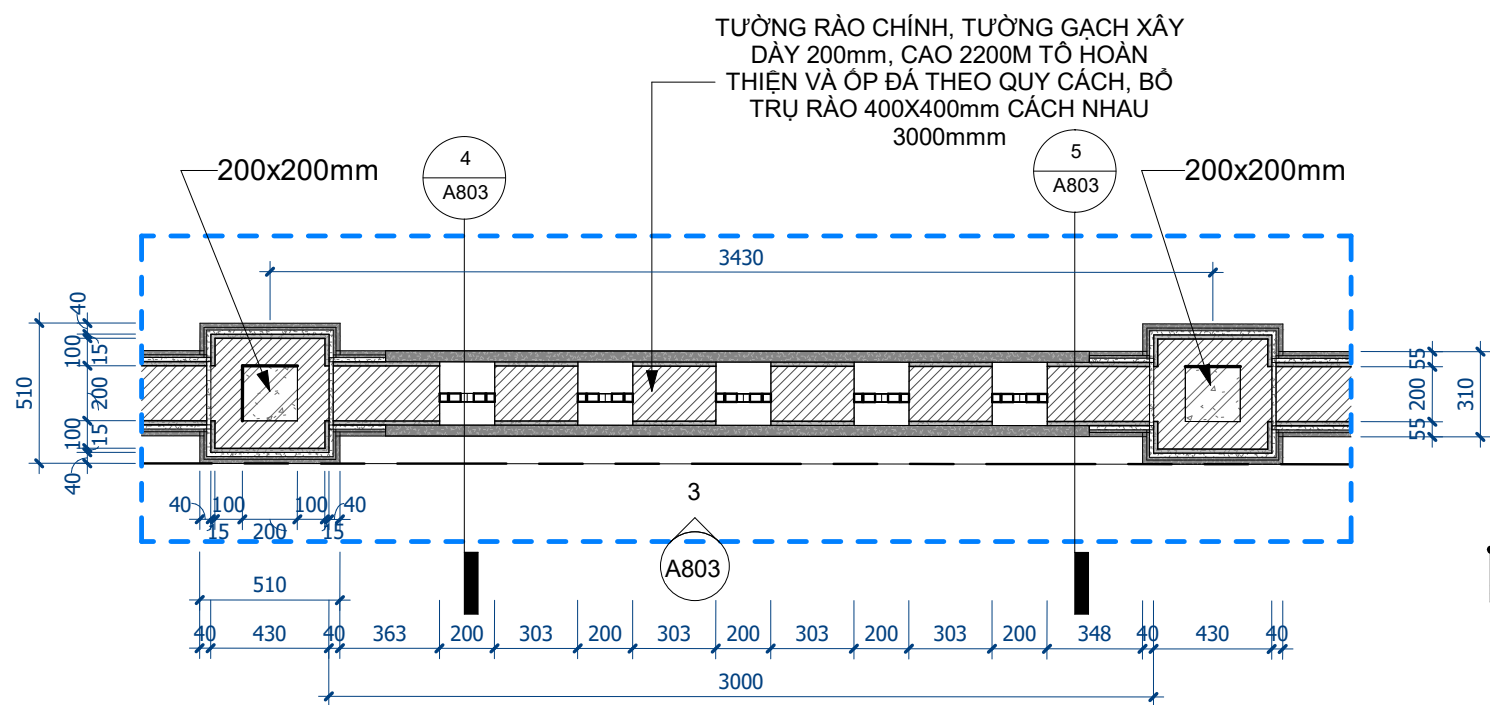


1 MB TRÍCH ĐOẠN HÀNG RÀO CHÍNH
1 : 25

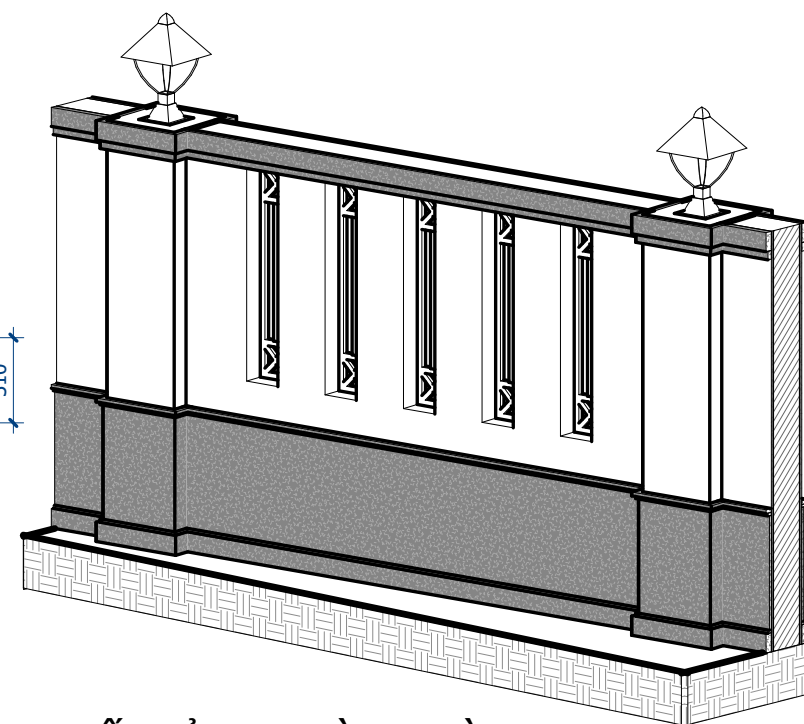

2 PHỐI CẢNH TƯỜNG RÀO

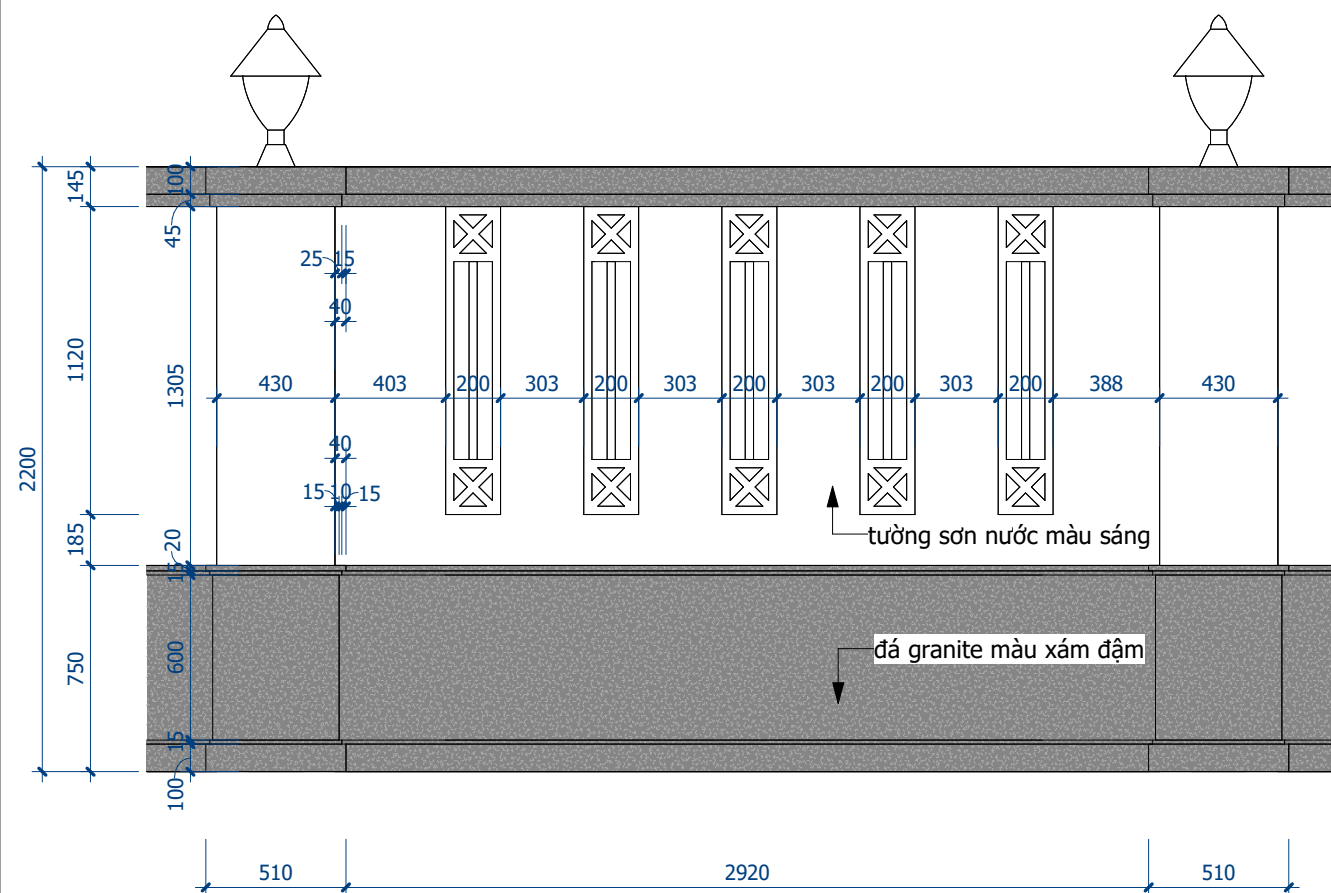

3 MẶT ĐỨNG TƯỜNG RÀO CHÍNH
1 : 25

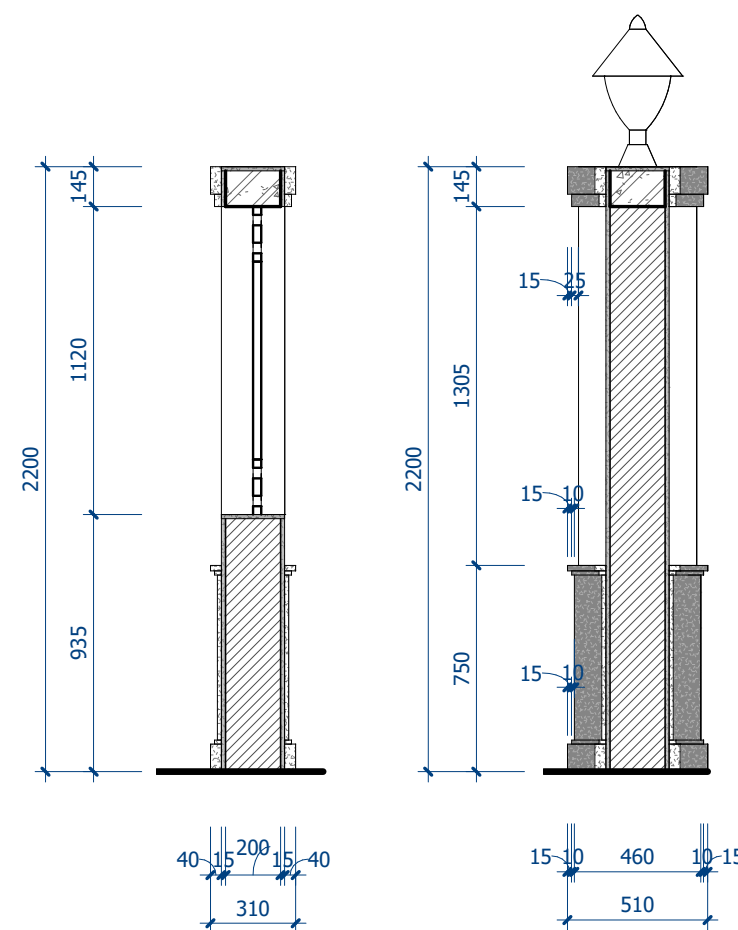

4 MC 1
1 : 25

5 MC 2
1 : 25